
La referencia, leída por partes

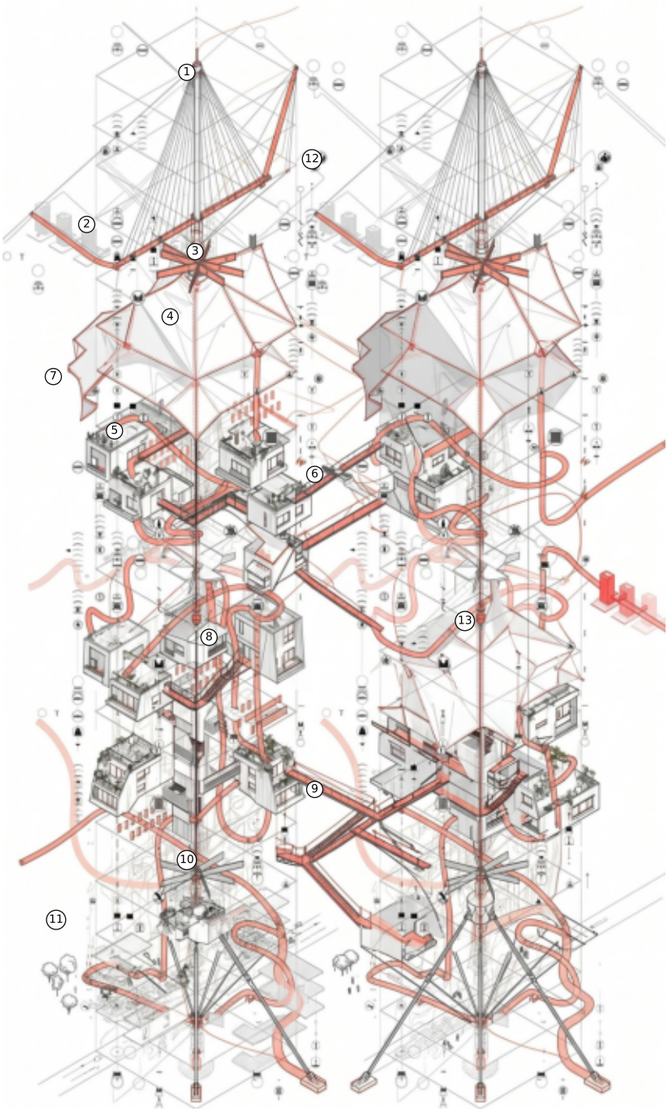

1. Mástil atirantado: un único soporte que llega al suelo en un punto · Engel p. 66–67
2. Coronación: los cables bajan de la cabeza del mástil a un plano de anclaje · p. 72–73
3. Crucetas: abren los cables y arriostran el mástil, como en un velero · p. 74
4. Carpa: membrana radial con el punto alto en el mástil; cubre un racimo de casas · p. 88–89
5. Racimo de 4–6 casas bajo cada carpa, cada una a su altura y con su orientación
6. Pasarela alta entre las dos torres
7. Tubos rojos: recorridos e instalaciones que bajan hasta el suelo
8. Escalera abierta enroscada al mástil, que llega a cada casa
9. Pasarela baja con escaleras: segundo cruce entre torres
10. Crucetas bajas y trípode: el mástil se ata al suelo con tirantes
11. Suelo libre con árboles
12. Columnas de símbolos: cada altura tiene su uso
13. Membrana a media altura sobre un espacio común · neumáticas p. 97–105

Cómo se reparten 40 personas: cada columna es una posición alrededor de un mástil, cada fila una altura




Tu lista, punto por punto


Espacio grande para cada uno	módulo propio de 5,00 × 4,50 (22,5 m²) + terraza-huerto en su cubierta
Común dentro de la estructura	plataformas abiertas entre los dos mástiles, una por planta
…para un número de personas	cocina y trabajo por barrio (10–12 personas), azotea para 40
…sobre todo para trabajar	plantas +8, +14, +20 y +23 de la columna común
Cocinas separadas y/o conjuntas	las dos: cocina pequeña en cada módulo y cocina grande por barrio
Elegante · luz ajustable	cortina doble (opaca y translúcida) y toldo textil exterior en cada ventanal
Ventanales grandes	toda la fachada exterior del módulo; en lo común, sin fachada
Descanso natural	parque en la azotea, árboles en planta baja, huerto en cada cubierta
Ascensor abierto con ventanales	cabina acristalada en cada mástil, para en cada rellano cada 3 m
Escaleras abiertas que conectan privados	escalera enroscada al mástil + pasarela a cada puerta
Cada casa a su altura y orientación	Galápagos: ver la hoja 2
Plantas abiertas, solo la cubierta colectiva	nada cierra la planta: los módulos son lo único cerrado

Cuentas para 40 personas (tanteo)


Módulos	42 posiciones: 40 personas + 2 libres
Privado	40 × 22,5 m² = 900 m²
Terraza-huerto privada	≈ 10 m² sobre cada módulo
Común entre mástiles	7 plataformas × ≈ 30 m² ≈ 210 m²
Módulos libres	2 × 22,5 m² = 45 m² (huéspedes, taller)
Mástiles	2 núcleos abiertos ≈ 160 m² computables
Azotea	lavandería 25 m² + parque ≈ 250 m² abierto
Planta baja	portal, bicis y taller ≈ 120 m²
Total construido	≈ 1.460 m² (enunciado ≈ 1.500 m²)
Altura	último módulo a +23,00, azotea a +26,00 = medianera sur

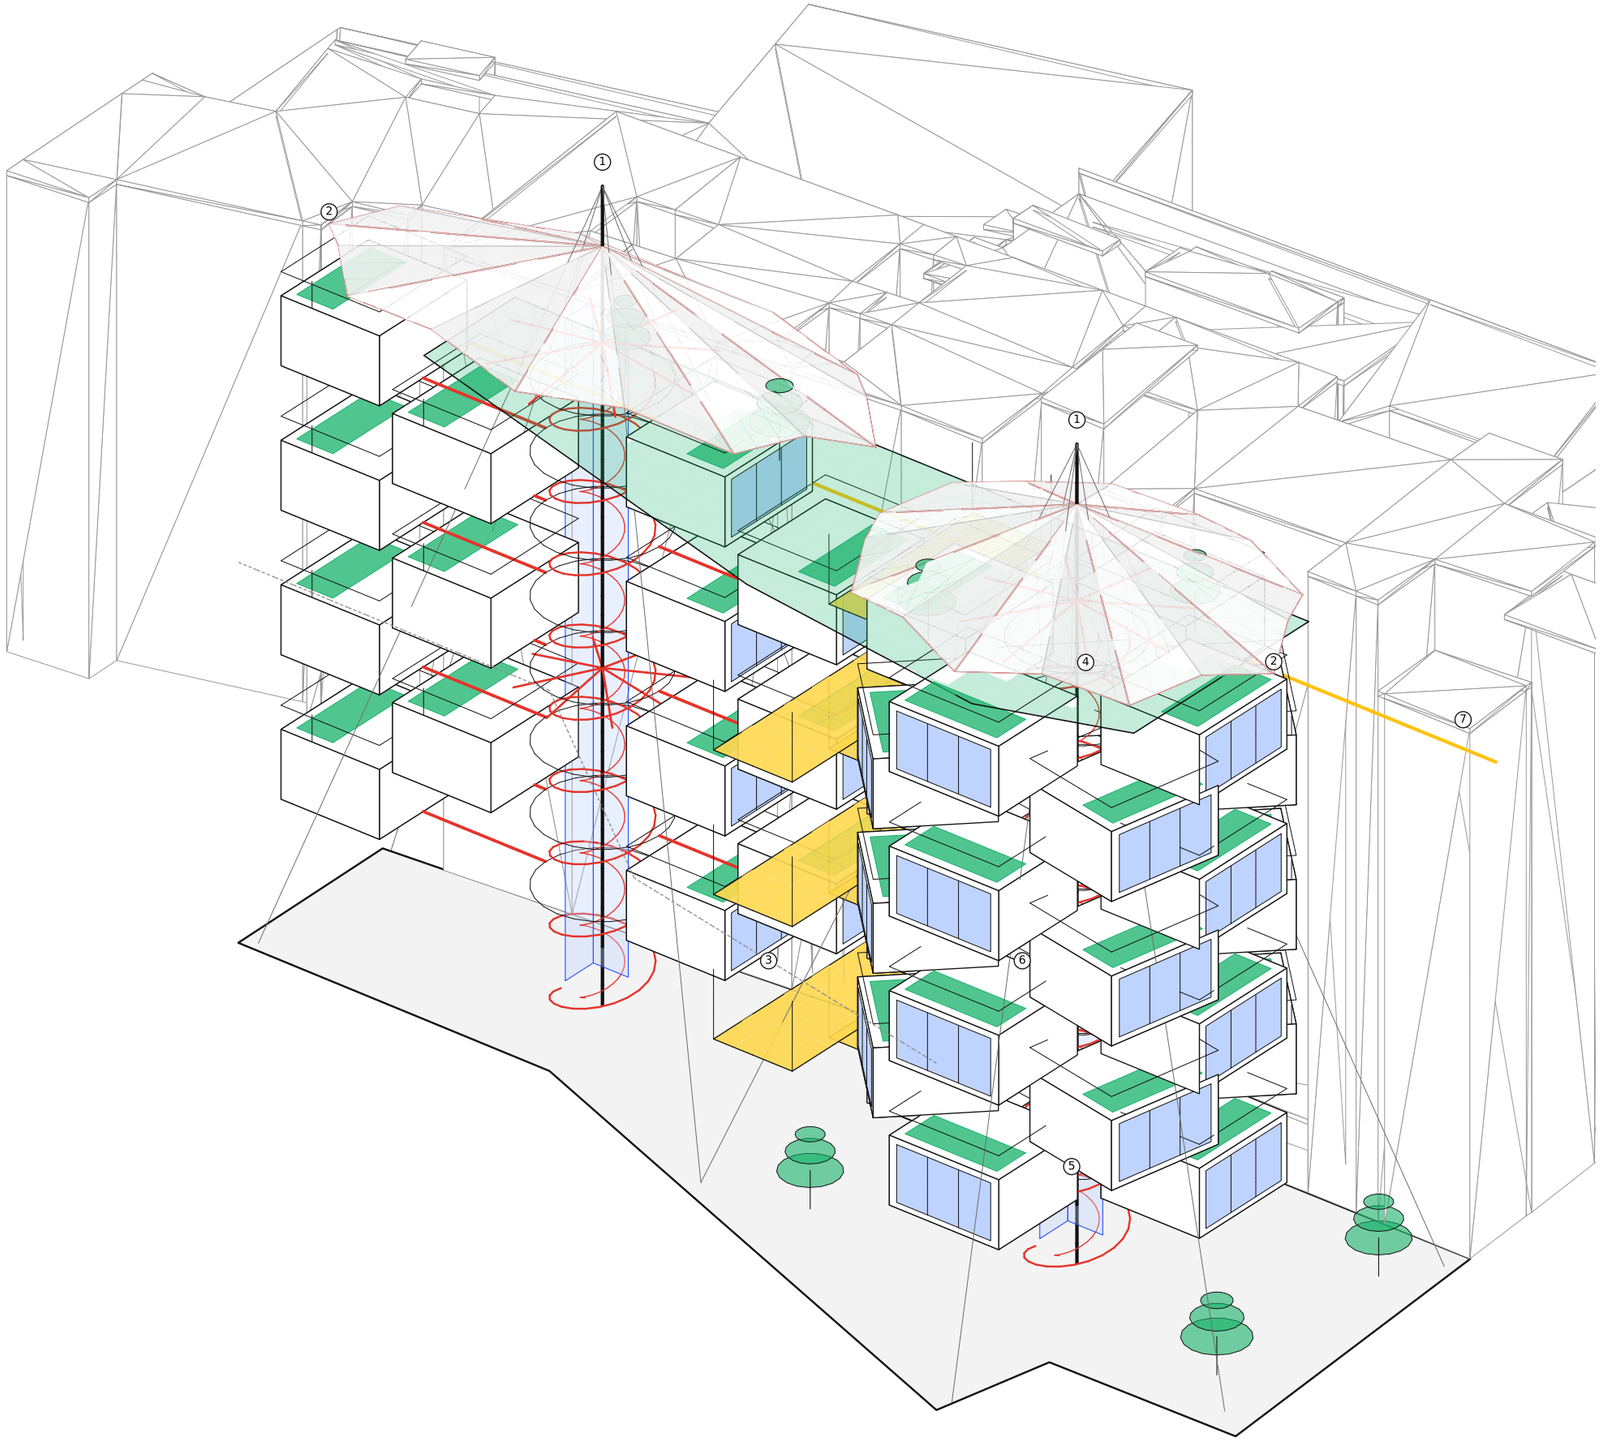


Planta 1:500 · +5,00 en color, +8,00 en discontinua · anillo de 8 en A, línea de 4 en B

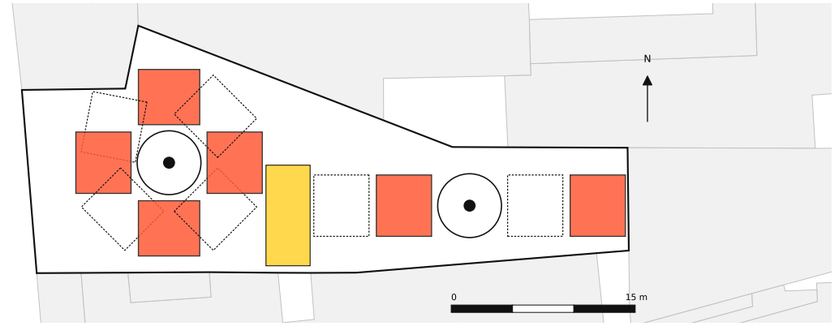

Módulo · planta 1:50 · 22,5 m² · cocina propia, baño junto a la pasarela del mástil

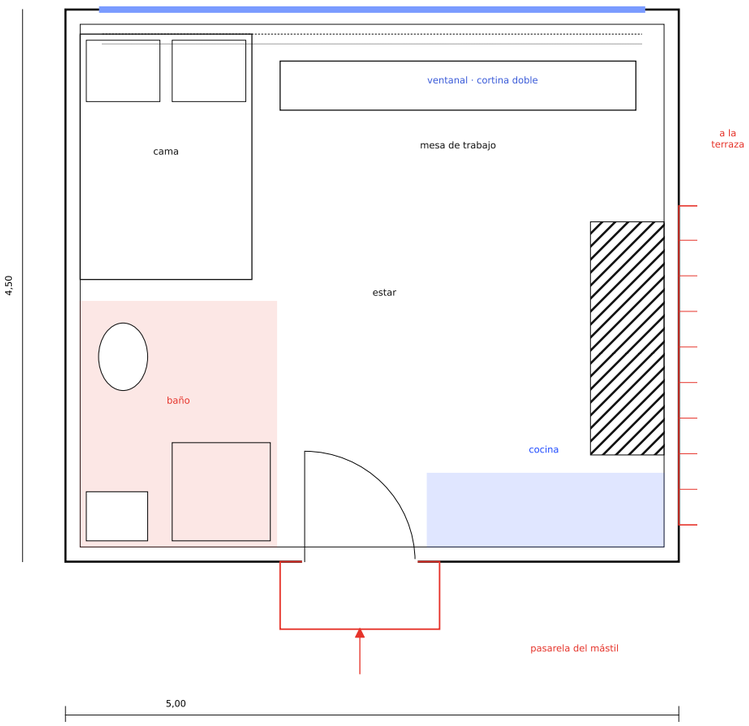

Módulo · sección 1:100

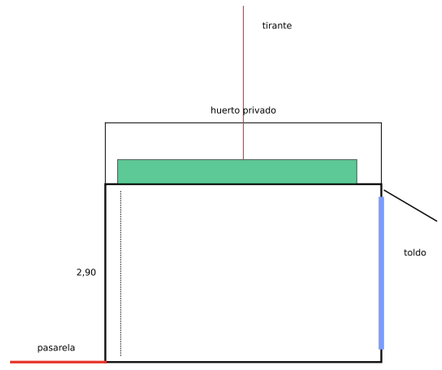

Para Galápagos: qué varía y qué se mide

Genes, por módulo	posición en el anillo (±15°), radio (5,4–6,5 m), medio nivel (0 / +1,50), giro del ventanal (±25°)
Se maximiza	horas de sol en el ventanal (Ladybug, 21 dic y 21 jun), cielo visto desde la terraza, distancia de vista
Se penaliza	choques, salir de la parcela, ventanales enfrentados a menos de 6 m, terraza tapada, pasarela > 3 m
Fijo	2 mástiles, rellanos cada 3 m, 40 módulos
Este tanteo	colocación a mano con las reglas; sin optimizar

1. mástil atirantado con escalera abierta y ascensor acristalado
2. carpa: el único techo colectivo
3. plataforma común de cada planta (cocina o trabajo)
4. parque en la azotea, +26,00
5. ascensor acristalado
6. pasarela abierta del mástil a la puerta de cada módulo
7. sol de invierno desde +21,10