
# *Megaestructura macarra · planta general*

*PLANTA · E 1:200 · tableros vistos desde arriba · malla de troncos · recorridos*

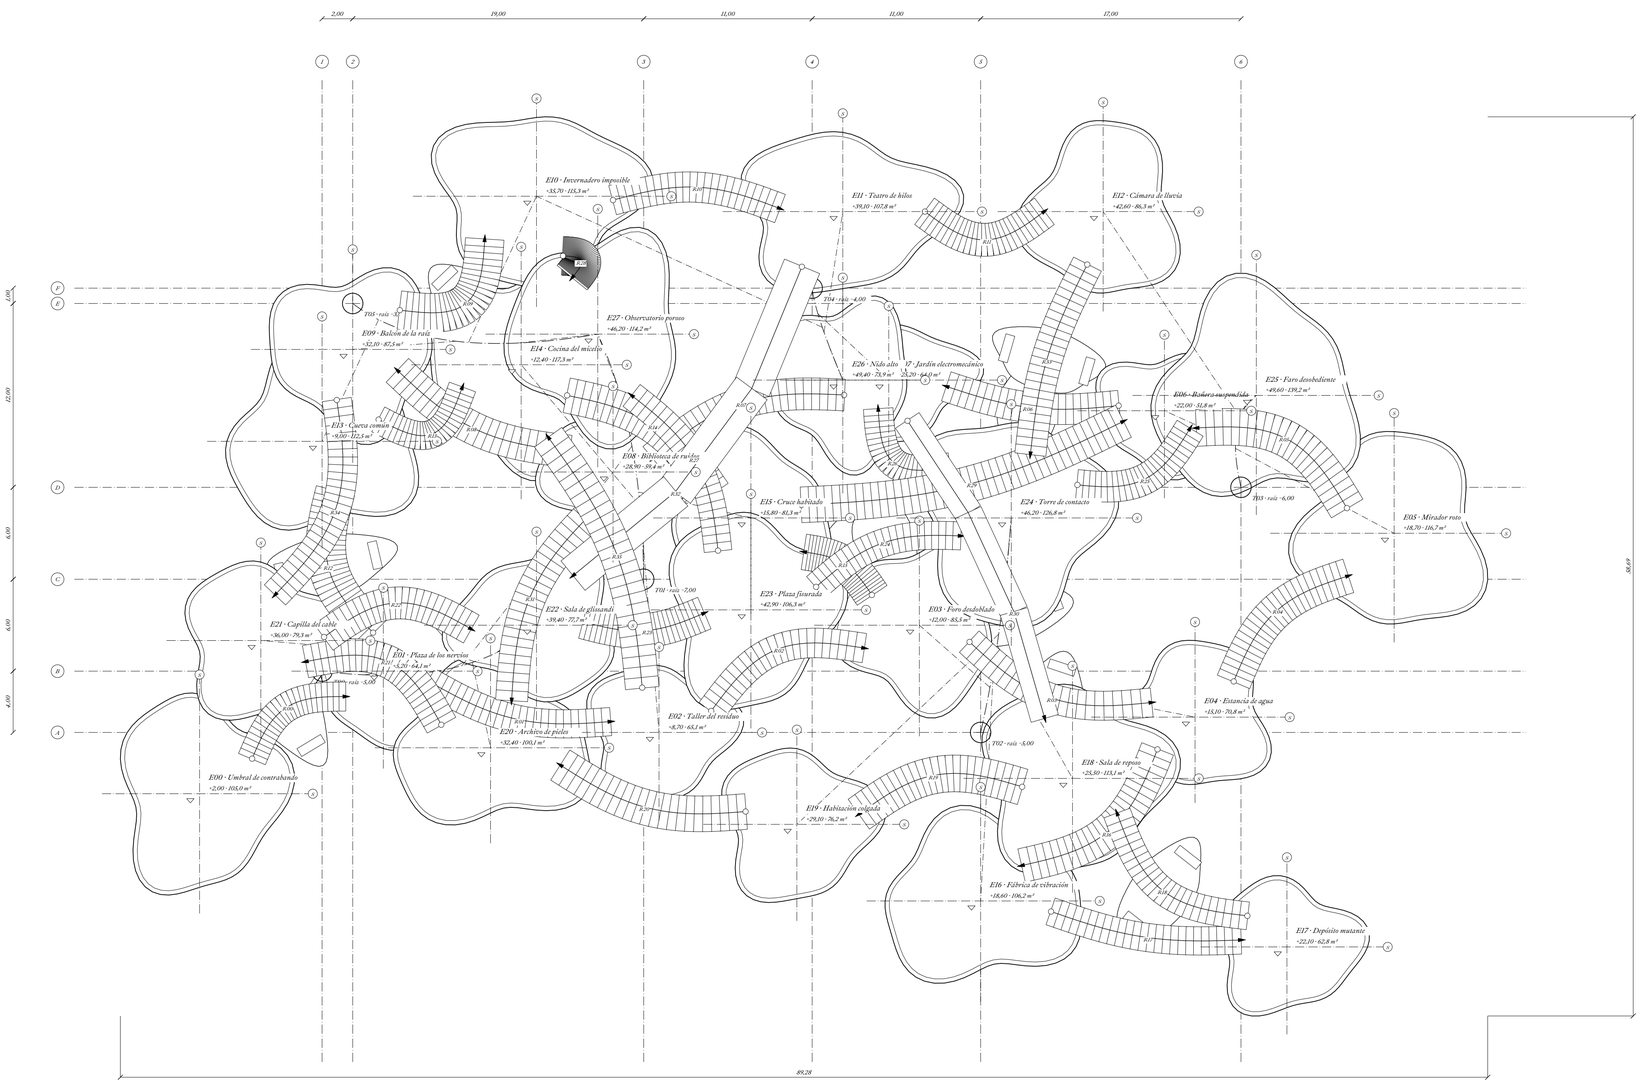


## *ESTRUCTURA*

*T00 · raíz · 5,00 · copa +39,40 · 5 ramas*
*a E01 · E08 · E20 · E21 · E22*

*T01 · raíz · 7,00 · copa +46,20 · 5 ramas*
*a E02 · E08 · E14 · E33 · E27*

*T02 · raíz · 5,00 · copa +46,20 · 6 ramas*
*a E03 · E04 · E16 · E18 · E19 · E24*

*T03 · raíz · 6,00 · copa +49,60 · 4 ramas*
*a E05 · E06 · E12 · E25*

*T04 · raíz · 4,00 · copa +49,40 · 4 ramas*
*a E07 · E10 · E11 · E26*

*T05 · raíz · 5,00 · copa +46,20 · 4 ramas*
*a E09 · E10 · E33 · E27*

## *RECORRIDOS*

*36 escaleras entre 28 estancias*
*903 peldaños · contrahuella máx. 16,4 cm*
*Anchos de 1,81 a 2,57 m*
*12 descansillos habitados con bancos*
*Cada escalera: dos tramos y meseta central*

## *LECTURA DEL DIBUJO*

*Negro sólido: material cortado a +1,20 m*
*0,25 mm: borde del tablero*
*0,18 mm: mobiliario y línea de huella*
*0,13 mm: peldaños vistos*
*Discontinua larga: velas y luces sobre el corte*
*Discontinua corta: máquinas bajo el tablero*
*Trazo-punto grueso: eje del tronco portante*
*Trazo-punto fino: ejes de rama y de la malla 1-6 / A-F*
*Sí: eje de simetría del ático generador*
*Círculo blanco: arranque · triángulo: llegada*

*Tableros dibujados desde arriba: el más alto tapa al más bajo. Cotas de tablero acabado medidas en Rhino.*


*Malla 1-6 / A-F: ejes por las raíces de los seis troncos. Las ramas no siguen la malla: cada una busca su estancia.*

*Geometría de malla del modelo MEGAESTRUCTURA_MACARRA.3dm (967 mallas, 1,93 M triángulos), sin redibujar.*

*0 2 4 10 m*

# *Megaestructura macarra · nivel 01 · +2,00*

*PLANTA · E 1:200 · corte horizontal a +3,20 m · todo lo cortado en negro · lo que queda debajo en proyección*

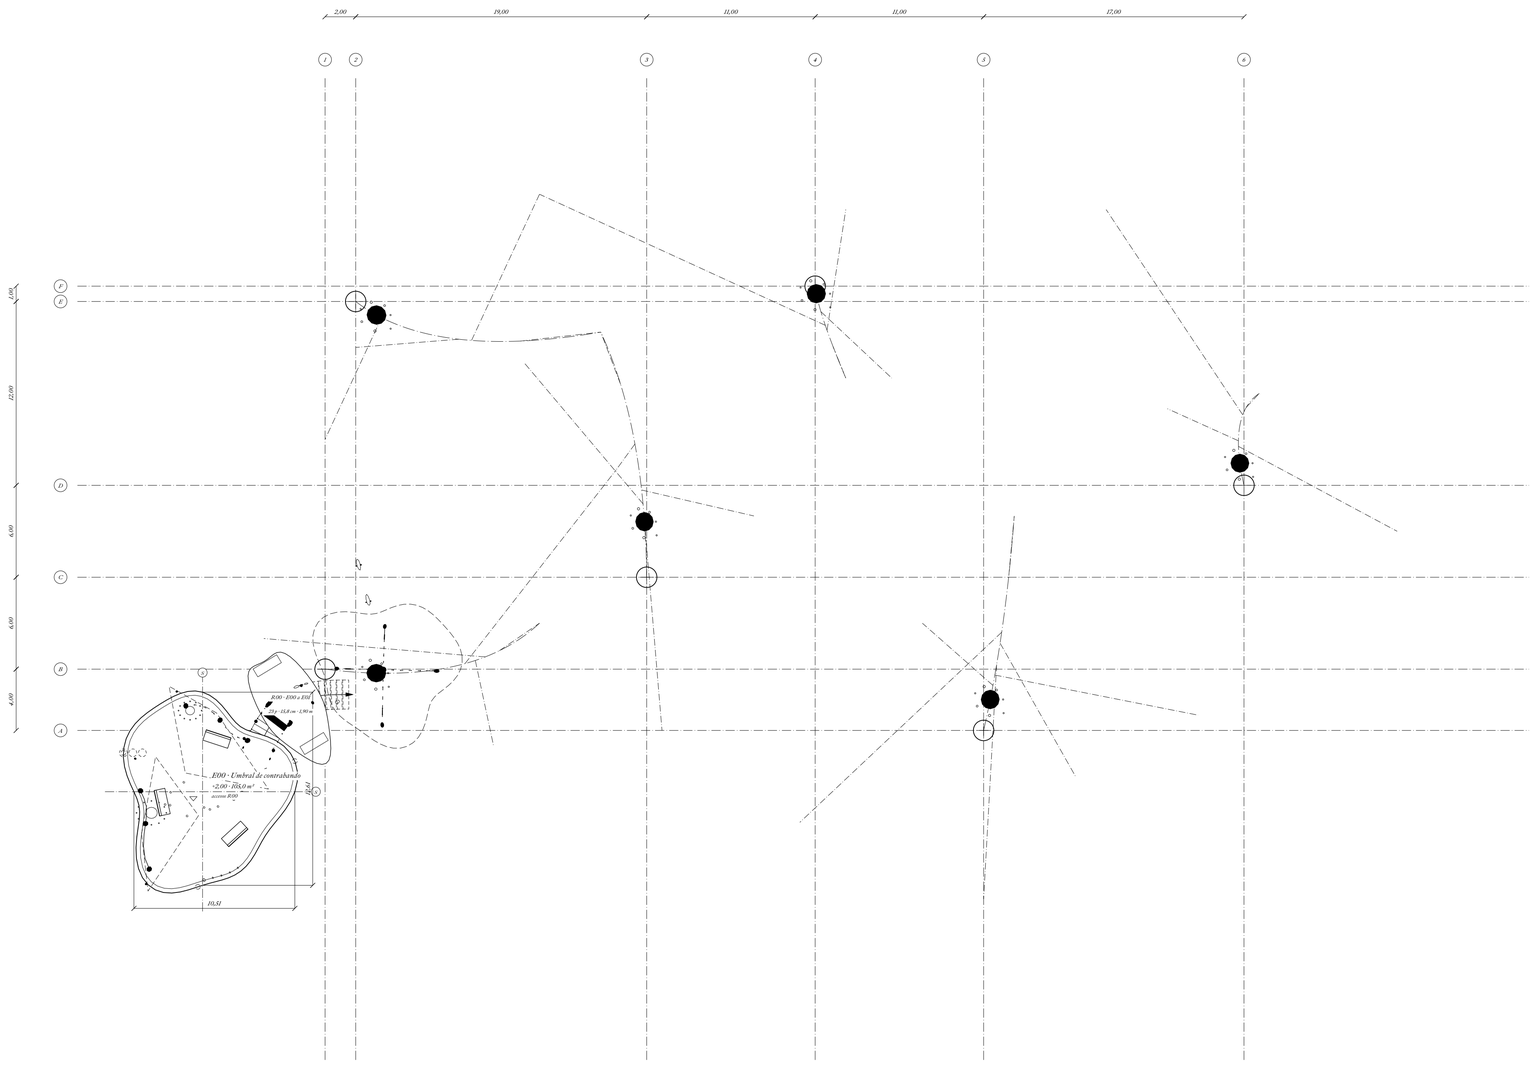


## *NIVEL*

*N01 · corte a +3,20 m*

*1,20 m sobre el tablero de E00 (+2,00)*

## *PROGRAMA*

*E00 · Umbral de contrabando*

*+2,00 · 103,0 m² · tablero 27 cm*

*3 bancos con respaldo · 1 velas · 3 cilindros bajo el tablero · 13 luces*

*sin rama de tronco propia*

## *CONEXIONES EN ESTA PLANTA*

*R00 · sala · E00 +2,00 a E01 +3,20*

## *LECTURA DEL DIBUJO*

*Negro: todo lo cortado a la cota del corte*

*0,25 mm: tableros del nivel*

*0,10 / 0,06 mm: tableros inferiores, según profundidad*

*Discontinua larga: tableros superiores, velas y luces*

*Discontinua corta: máquinas bajo el tablero*

*Trazo-punto: troncos, ramas, malla y ejes S*

*Corte horizontal único a +3,20 m sobre toda la megaestructura: cada malla de Rhino intersecada con el plano.*


*Debajo, los tableros inferiores en proyección: el más alto tapa al más bajo. Encima, hasta 6 m, en discontinua.*

*Escaleras: línea de huella, arranque (círculo) y llegada (triángulo); peldaños por encima del corte en discontinua.*

*0 2 4 10 m*

# *Megaestructura macarra · nivel 02 · +5,20*

*PLANTA · E 1:200 · corte horizontal a +6,40 m · todo lo cortado en negro · lo que queda debajo en proyección*

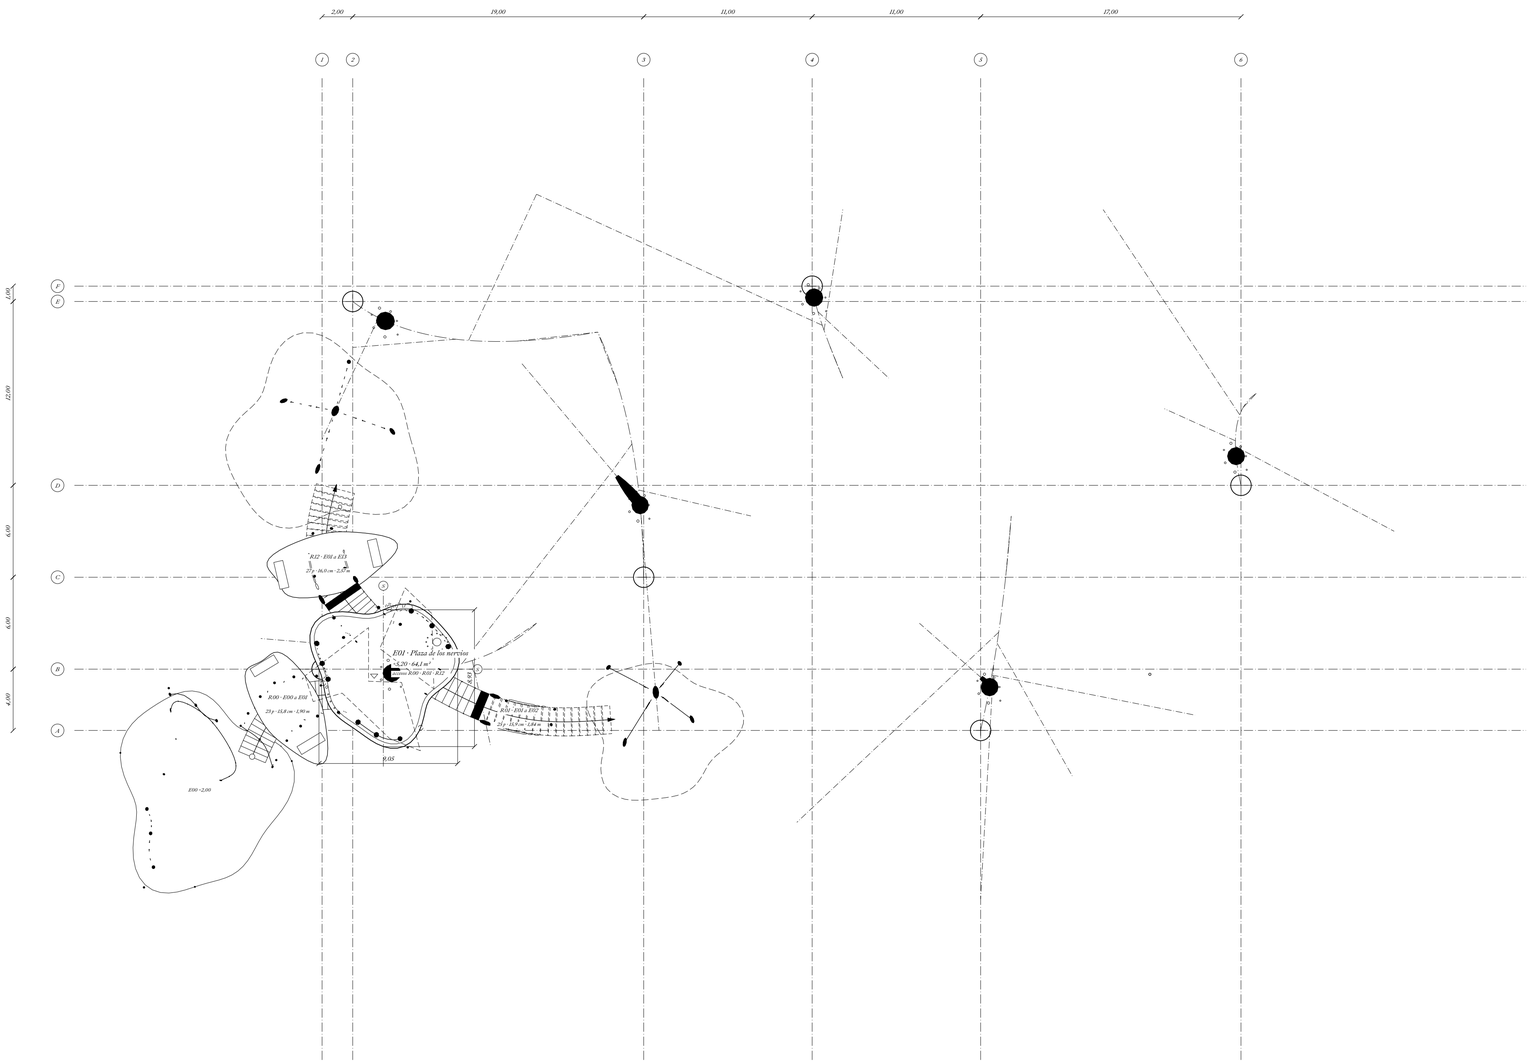


## NIVEL

*N02 · corte a +6,40 m*

*1,20 m sobre el tablero de E01 (+5,20)*

## PROGRAMA

*E01 · Plaza de los nervios*

*+5,20 · 64,1 m² · tablero 27 cm*

*sin bancos · 1 velas · 5 cilindros bajo el tablero · 3 luces*

*sostenida por T00*

## CONEXIONES EN ESTA PLANTA

*R00 · llega · E00 +2,00 a E01 +5,20*

*R01 · sale · E01 +5,20 a E02 +8,70*

*R12 · sale · E01 +5,20 a E03 +9,00*

## LECTURA DEL DIBUJO

*Negro: todo lo cortado a la cota del corte*

*0,25 mm: tableros del nivel*

*0,10 / 0,06 mm: tableros inferiores, según profundidad*

*Discontinua larga: tableros superiores, velas y luces*

*Discontinua corta: máquinas bajo el tablero*

*Trazo-punto: troncos, ramas, malla y ejes S*

*Corte horizontal único a +6,40 m sobre toda la megaestructura: cada malla de Rhino intersecada con el plano.*


*Debajo, los tableros inferiores en proyección: el más alto tapa al más bajo. Encima, hasta 6 m, en discontinua.*

*Escaleras: línea de huella, arranque (círculo) y llegada (triángulo); peldaños por encima del corte en discontinua.*

*0 2 4 10 m*

# *Megaestructura macarra · nivel 03 · +8,70 / +9,00*

*PLANTA · E 1:200 · corte horizontal a +9,90 m · todo lo cortado en negro · lo que queda debajo en proyección*

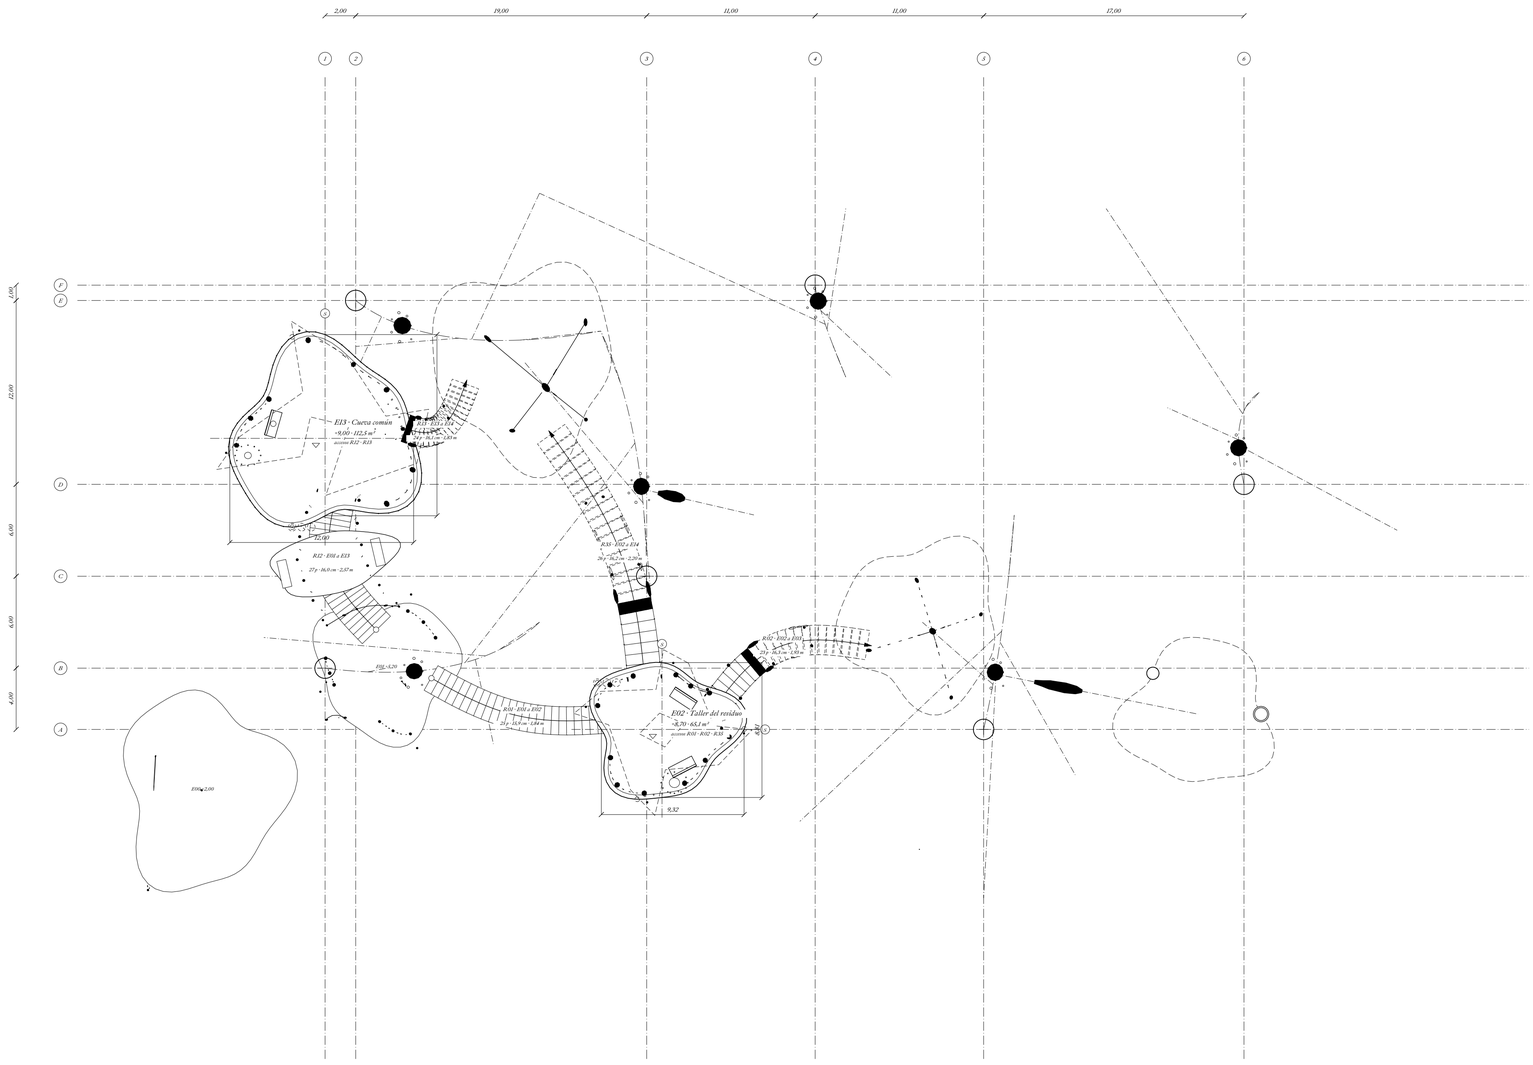


## *NIVEL*

***N03 · corte a +9,90 m***

- *1,20 m sobre el tablero de E02 (+8,70)*
- *0,90 m sobre el tablero de E03 (+9,00)*

## *PROGRAMA*

***E02 · Taller del residuo***

- *+8,70 · 65,1 m² · tablero 27 cm*
- *2 bancos con respaldo · 1 velas · 3 cilindros bajo el tablero · 3 luces*
- *sostenida por T01*

***E03 · Cueva común***

- *+9,00 · 112,5 m² · tablero 27 cm*
- *1 bancos con respaldo · 1 velas · 3 cilindros bajo el tablero · 3 luces*
- *sostenida por T05*

## *CONEXIONES EN ESTA PLANTA*

*R01 · llega · E01 +5,20 a E02 +8,70*
*R02 · sale · E02 +8,70 a E03 +12,00*
*R12 · llega · E01 +5,20 a E13 +9,00*
*R13 · sale · E13 +9,00 a E04 +12,40*
*R35 · sale · E02 +8,70 a E04 +12,40*

## *LECTURA DEL DIBUJO*

*Negro: todo lo cortado a la cota del corte*
*0,25 mm: tableros del nivel*
*0,10 / 0,06 mm: tableros inferiores, según profundidad*
*Discontinua larga: tableros superiores, velas y luces*
*Discontinua corta: máquinas bajo el tablero*
*Trazo-punto: troncos, ramas, malla y ejes S*

*Corte horizontal único a +9,90 m sobre toda la megaestructura: cada malla de Rhino intersecada con el plano.*


*Debajo, los tableros inferiores en proyección; el más alto tapa al más bajo. Encima, hasta 6 m, en discontinua.*

*Escaleras: línea de huella, arranque (círculo) y llegada (triángulo); peldaños por encima del corte en discontinua.*

*0 2 4 10 m*

# *Megaestructura macarra · nivel 04 · +12,00 / +12,40*

*PLANTA · E 1:200 · corte horizontal a +13,20 m · todo lo cortado en negro · lo que queda debajo en proyección*

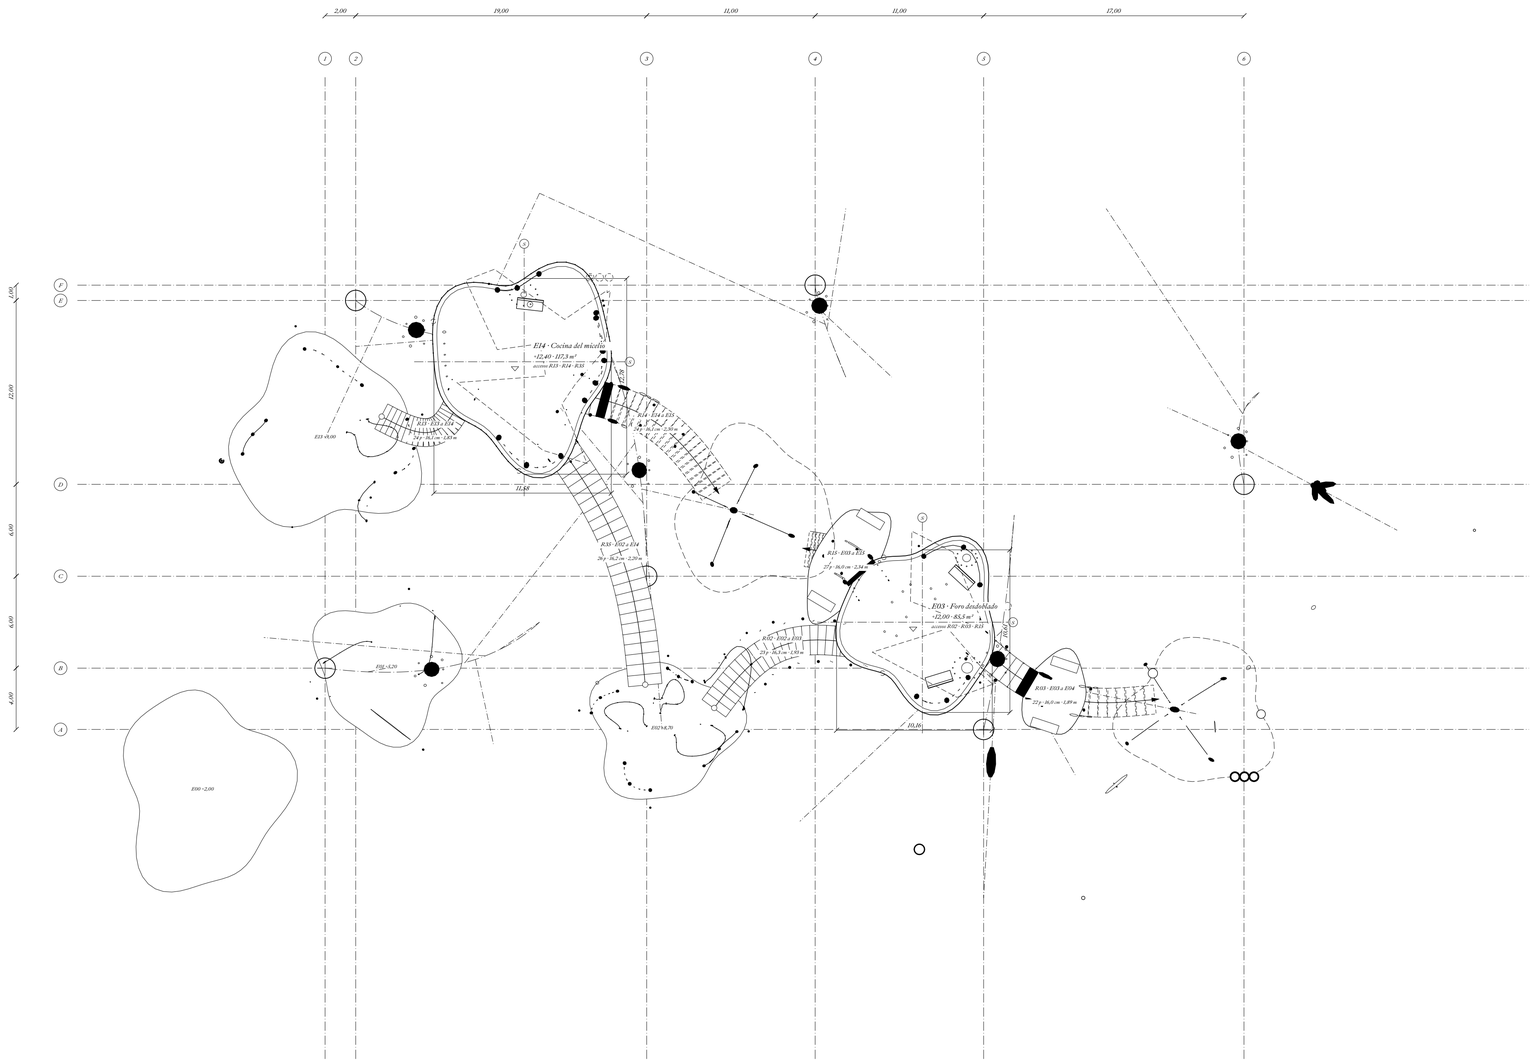


## *NIVEL*

*N04 · corte a +13,20 m*

- *1,20 m sobre el tablero de E03 (+12,00)*
- *0,80 m sobre el tablero de E14 (+12,40)*

## *PROGRAMA*

*E03 · Foro desdoblado*

- *+12,00 · 85,5 m² · tablero 27 cm*
- *2 bancos con respaldo · 1 velas · 3 cilindros bajo el tablero · 13 luces*
- *sostenida por T02*

*E14 · Cocina del micelio*

- *+12,40 · 117,3 m² · tablero 27 cm*
- *1 bancos con respaldo · 1 velas · 3 cilindros bajo el tablero · 5 luces*
- *sostenida por T01*

## *CONEXIONES EN ESTA PLANTA*

*R02 · llega · E02 +8,70 a E03 +12,00*

*R03 · sale · E03 +12,00 a E04 +5,10*

*R13 · llega · E13 +9,00 a E14 +12,40*

*R14 · sale · E14 +12,40 a E15 +5,80*

*R35 · sale · E03 +12,00 a E35 +5,80*

*R35 · llega · E02 +8,70 a E34 +12,40*

## *LECTURA DEL DIBUJO*

*Negro: todo lo cortado a la cota del corte*

*0,25 mm: tableros del nivel*

*0,10 / 0,06 mm: tableros inferiores, según profundidad*

*Discontinua larga: tableros superiores, velas y luces*

*Discontinua corta: máquinas bajo el tablero*

*Trazo-punto: troncos, ramas, malla y ejes S*

*Corte horizontal único a +13,20 m sobre toda la megaestructura: cada malla de Rhino intersecada con el plano.*


*Debajo, los tableros inferiores en proyección: el más alto tapa al más bajo. Encima, hasta 6 m, en discontinua.*

*Escaleras: línea de huella, arranque (círculo) y llegada (triángulo); peldaños por encima del corte en discontinua.*

*0 2 4 10 m*

# *Megaestructura macarra · nivel 05 · +15,10 / +15,80*

*PLANTA · E 1:200 · corte horizontal a +16,30 m · todo lo cortado en negro · lo que queda debajo en proyección*

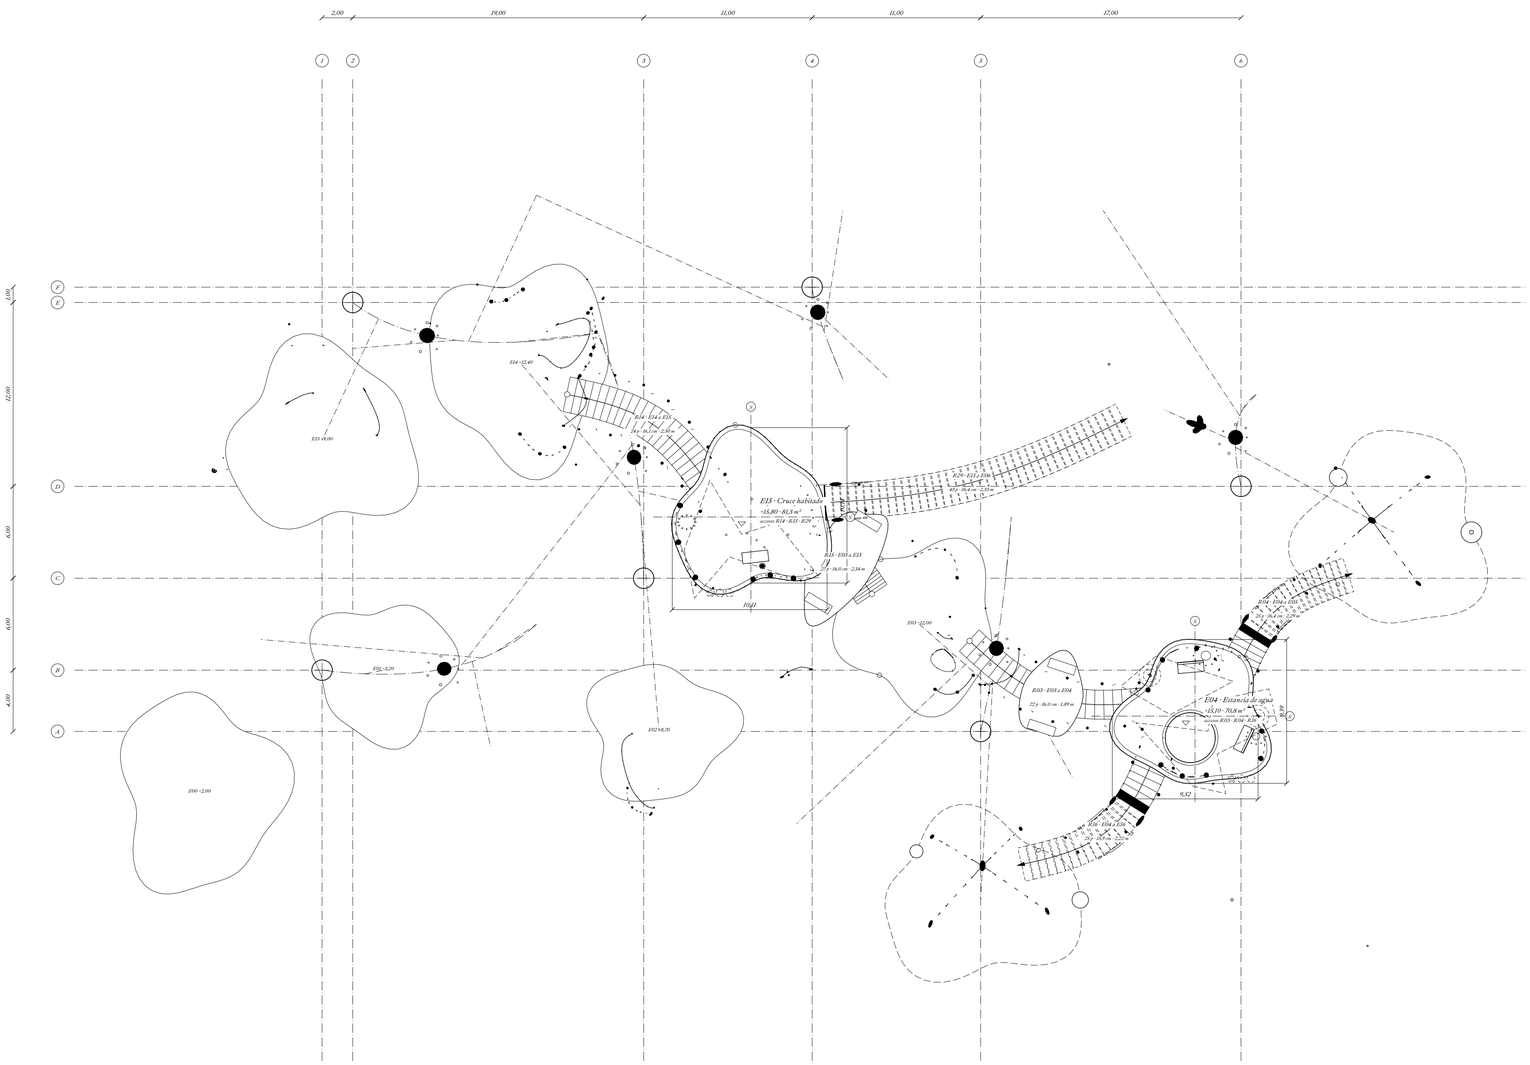


## *NIVEL*

***N05 · corte a +16,30 m***

*1,20 m sobre el tablero de E04 (+15,10)*

*0,50 m sobre el tablero de E15 (+15,80)*

## *PROGRAMA*

***E04 · Estancia de agua***

*+15,10 · 70,8 m² · tablero 27 cm*

*2 bancos con respaldo · 1 velas · 3 cilindros bajo el tablero · 3 luces · cuenco de agua y vasijas colgadas*

*sostenida por T02*

***E15 · Cruce habitado***

*+15,80 · 81,3 m² · tablero 27 cm*

*1 bancos con respaldo · 1 velas · 3 cilindros bajo el tablero · 13 luces*

*sostenida por T01*

## *CONEXIONES EN ESTA PLANTA*

*R03 · llega · E03 +12,00 a E04 +15,10*

*R04 · sale · E04 +15,10 a E05 +18,70*

*R14 · llega · E14 +12,40 a E15 +15,80*

*R15 · llega · E03 +12,00 a E15 +15,80*

*R16 · sale · E04 +15,10 a E16 +18,60*

*R29 · sale · E15 +15,80 a E06 +22,00*

## *LECTURA DEL DIBUJO*

*Negro: todo lo cortado a la cota del corte*

*0,25 mm: tableros del nivel*

*0,10 / 0,06 mm: tableros inferiores, según profundidad*

*Discontinua larga: tableros superiores, velas y luces*

*Discontinua corta: máquinas bajo el tablero*

*Trazo-punto: troncos, ramas, malla y ejes S*

*Corte horizontal único a +16,30 m sobre toda la megaestructura: cada malla de Rhino intersecada con el plano.*


*Debajo, los tableros inferiores en proyección: el más alto tapa al más bajo. Encima, hasta 6 m, en discontinua.*

*Escaleras: línea de huella, arranque (círculo) y llegada (triángulo); peldaños por encima del corte en discontinua.*

*0 2 4 10 m*

# *Megaestructura macarra · nivel 06 · +18,60 / +18,70*

*PLANTA · E 1:200 · corte horizontal a +19,80 m · todo lo cortado en negro · lo que queda debajo en proyección*

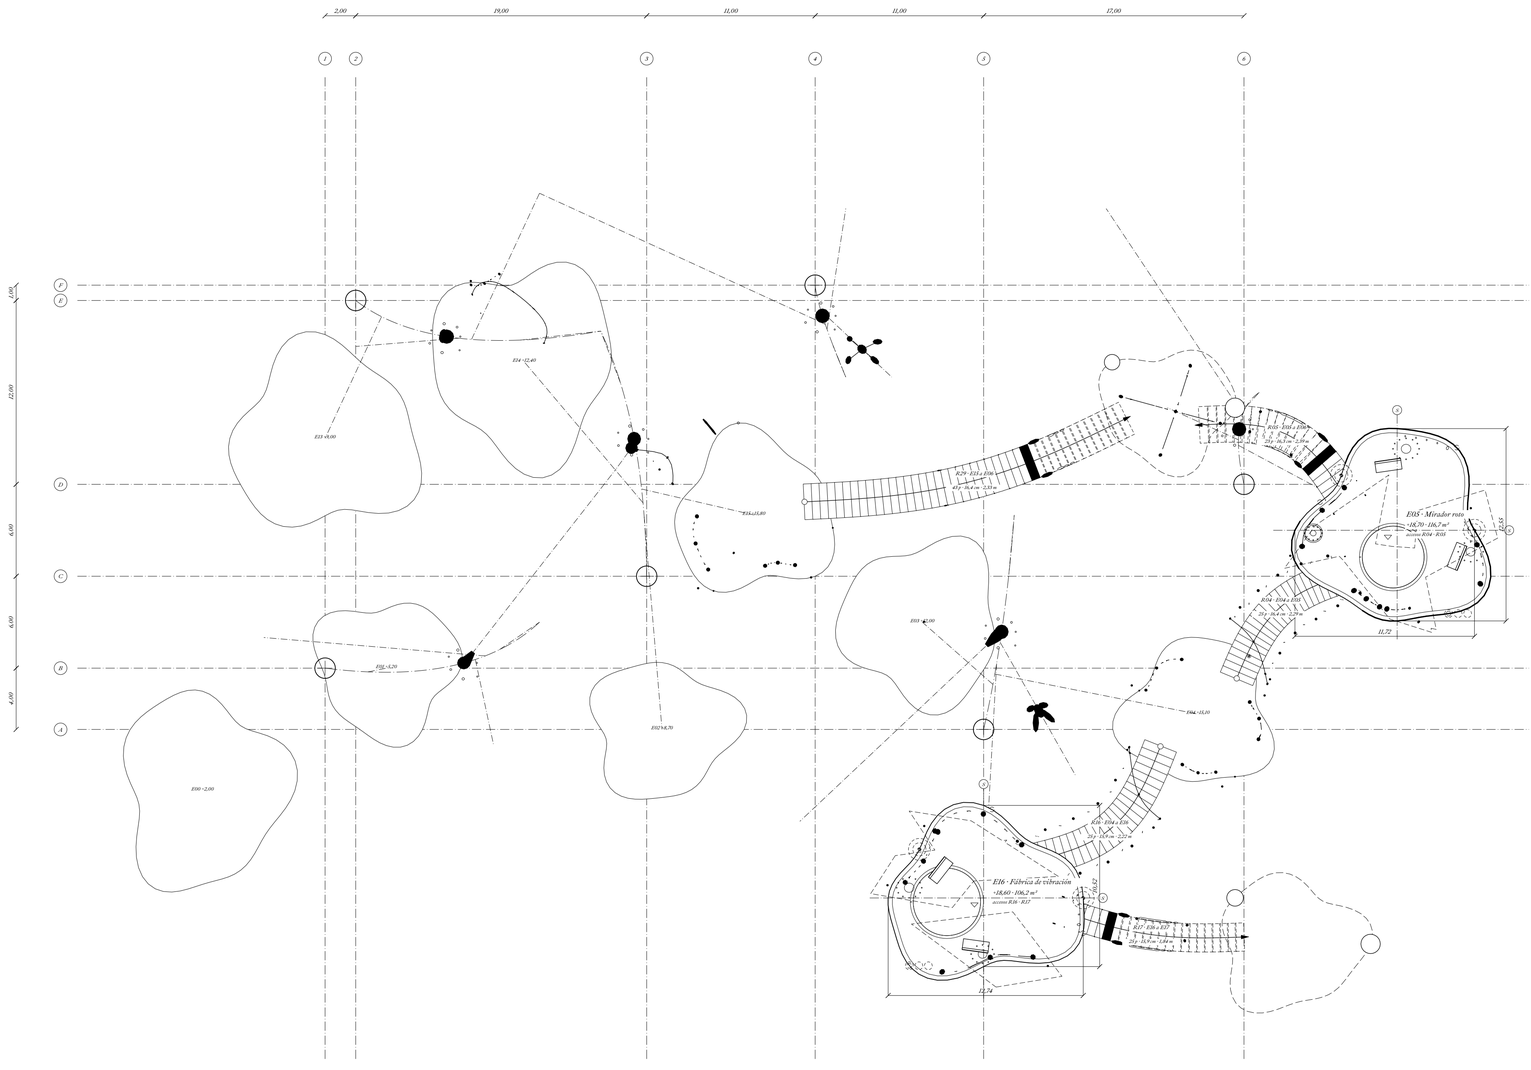


## NIVEL

*N06 · corte a +19,80 m*

- *1,20 m sobre el tablero de E16 (+18,60)*
- *1,10 m sobre el tablero de E05 (+18,70)*

## PROGRAMA

*E16 · Fábrica de vibración*

- *+18,60 · 106,2 m² · tablero 27 cm*
- *2 bancos con respaldo · 1 velas · 3 cilindros bajo el tablero · 3 luces · cuenco de agua y vasijas colgadas*
- *sostenida por T02*

*E05 · Mirador roto*

- *+18,70 · 116,7 m² · tablero 27 cm*
- *2 bancos con respaldo · 1 velas · 3 cilindros bajo el tablero · 3 luces · cuenco de agua y vasijas colgadas*
- *sostenida por T03*

## CONEXIONES EN ESTA PLANTA

*R04 · llega · E04 +13,10 a E05 +18,70*

*R05 · sale · E05 +18,70 a E06 +22,00*

*R16 · llega · E04 +13,10 a E16 +18,60*

*R17 · sale · E16 +18,60 a E17 +22,10*

*R29 · pasa cortada · E35 +15,80 a E06 +22,00*

## LECTURA DEL DIBUJO

*Negro: todo lo cortado a la cota del corte*

*0,25 mm: tableros del nivel*

*0,10 / 0,06 mm: tableros inferiores, según profundidad*

*Discontinua larga: tableros superiores, velas y luces*

*Discontinua corta: máquinas bajo el tablero*

*Trazo-punto: troncos, ramas, malla y ejes S*

*Corte horizontal único a +19,80 m sobre toda la megaestructura: cada malla de Rhino intersecada con el plano.*


*Debajo, los tableros inferiores en proyección: el más alto tapa al más bajo. Encima, hasta 6 m, en discontinua.*

*Escaleras: línea de huella, arranque (círculo) y llegada (triángulo); peldaños por encima del corte en discontinua.*

*0 2 4 10 m*

# *Megaestructura macarra · nivel 07 · +22,00 / +22,10*

*PLANTA · E 1:200 · corte horizontal a +23,20 m · todo lo cortado en negro · lo que queda debajo en proyección*

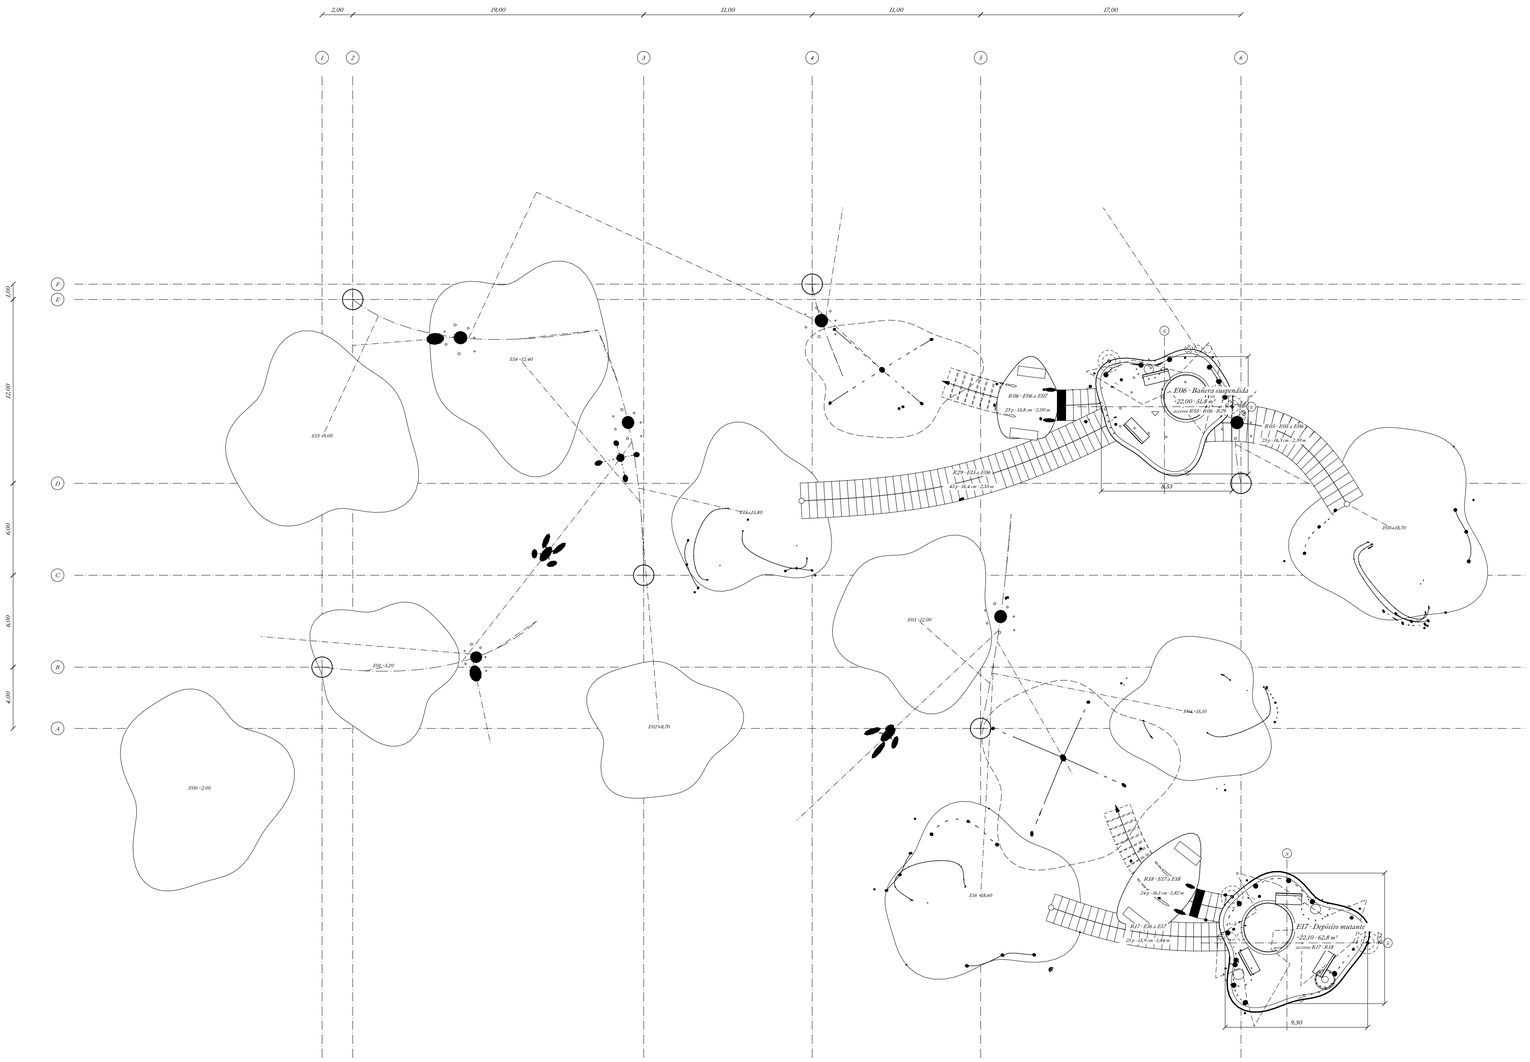


## *NIVEL*

*N07 · corte a +23,20 m*

- *1,20 m sobre el tablero de E06 (+22,00)*
- *1,10 m sobre el tablero de E27 (+22,10)*

## *PROGRAMA*

*E06 · Bañera suspendida*

- *+22,00 · 51,8 m² · tablero 27 cm*
- *2 bancos con respaldo · 1 velas · 3 cilindros bajo el tablero · 13 luces · cuenco de agua y tuvijas colgadas sostenida por T03*

*E17 · Depósito mutante*

- *+22,10 · 62,8 m² · tablero 27 cm*
- *3 bancos con respaldo · 1 velas · 3 cilindros bajo el tablero · 3 luces · cuenco de agua y tuvijas colgadas sin rama de tronco propia*

## *CONEXIONES EN ESTA PLANTA*

*R35 · llega · E05 +18,70 a E06 +22,00*

*R36 · sale · E06 +22,00 a E07 +25,20*

*R37 · llega · E16 +18,60 a E17 +22,10*

*R38 · sale · E17 +22,10 a E18 +25,80*

*R29 · llega · E15 +15,80 a E06 +22,00*

## *LECTURA DEL DIBUJO*

*Negro: todo lo cortado a la cota del corte*

*0,25 mm: tableros del nivel*

*0,10 / 0,06 mm: tableros inferiores, según profundidad*

*Discontinua larga: tableros superiores, velas y luces*

*Discontinua corta: máquinas bajo el tablero*

*Trazo-punto: troncos, ramas, malla y ejes S*

*Corte horizontal único a +23,20 m sobre toda la megaestructura: cada malla de Rhino intersecada con el plano.*


*Debajo, los tableros inferiores en proyección: el más alto tapa al más bajo. Encima, hasta 6 m, en discontinua.*

*Escaleras: línea de huella, arranque (círculo) y llegada (triángulo); peldaños por encima del corte en discontinua.*

*0 2 4 10 m*

# *Megaestructura macarra · nivel 08 · +25,20 / +25,50*

*PLANTA · E 1:200 · corte horizontal a +26,40 m · todo lo cortado en negro · lo que queda debajo en proyección*

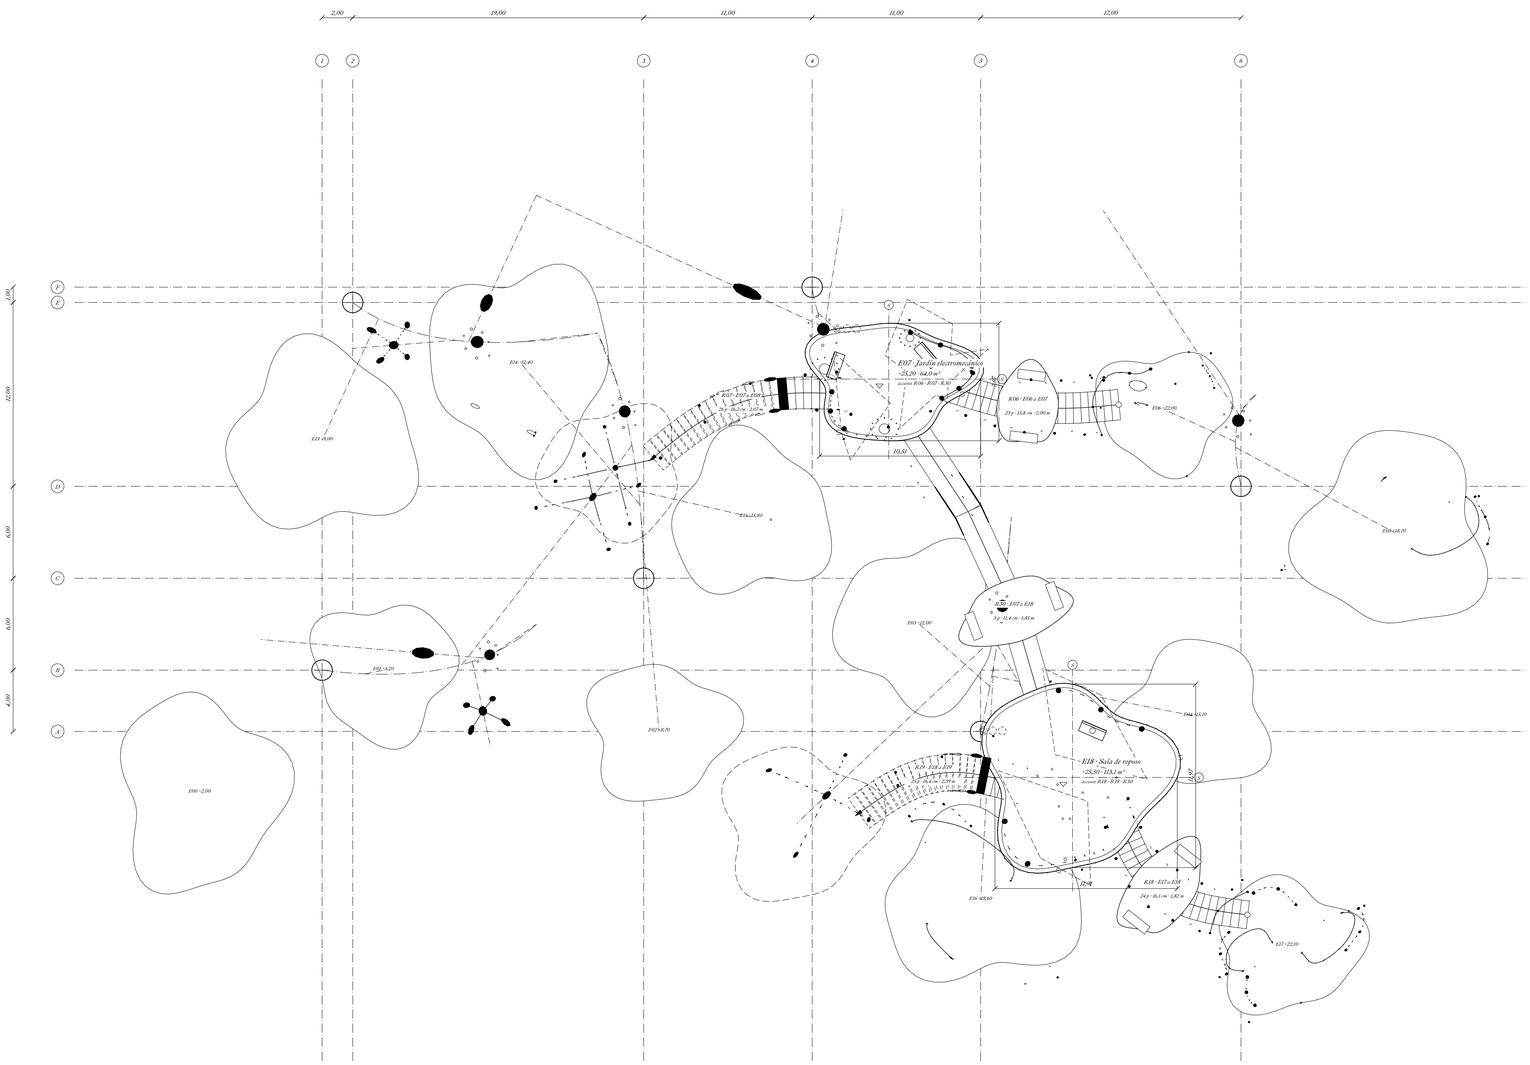


## NIVEL

***N08 · corte a +26,40 m***

- *1,20 m sobre el tablero de E07 (+25,20)*
- *0,90 m sobre el tablero de E08 (+25,50)*

## PROGRAMA

***E07 · Jardín electromecánico***

- *+25,20 · 64,0 m² · tablero 27 cm*
- *2 bancos con respaldo · 1 velas · 3 cilindros bajo el tablero · 3 luces*
- *sostenida por T04*

***E08 · Sala de reposo***

- *+25,50 · 113,1 m² · tablero 27 cm*
- *1 bancos con respaldo · 1 velas · 3 cilindros bajo el tablero · 13 luces*
- *sostenida por T02*

## CONEXIONES EN ESTA PLANTA

*R06 · llega · E06 · +22,00 a E07 · +25,20*

*R07 · sale · E07 · +25,20 a E08 · +28,90*

*R18 · llega · E17 · +22,10 a E18 · +25,50*

*R19 · sale · E18 · +25,50 a E19 · +29,10*

*R30 · sale · E07 · +25,20 a E18 · +25,50*

## LECTURA DEL DIBUJO

*Negro: todo lo cortado a la cota del corte*

*0,25 mm: tableros del nivel*

*0,10 / 0,06 mm: tableros inferiores, según profundidad*

*Discontinua larga: tableros superiores, velas y luces*

*Discontinua corta: máquinas bajo el tablero*

*Trazo-punto: troncos, ramas, malla y ejes S*

*Corte horizontal único a +26,40 m sobre toda la megaestructura: cada malla de Rhino intersecada con el plano.*


*Debajo, los tableros inferiores en proyección: el más alto tapa al más bajo. Encima, hasta 6 m, en discontinua.*

*Escaleras: línea de huella, arranque (círculo) y llegada (triángulo); peldaños por encima del corte en discontinua.*

*0 2 4 10 m*

# *Megaestructura macarra · nivel 09 · +28,90 / +29,10*

*PLANTA · E 1:200 · corte horizontal a +30,10 m · todo lo cortado en negro · lo que queda debajo en proyección*

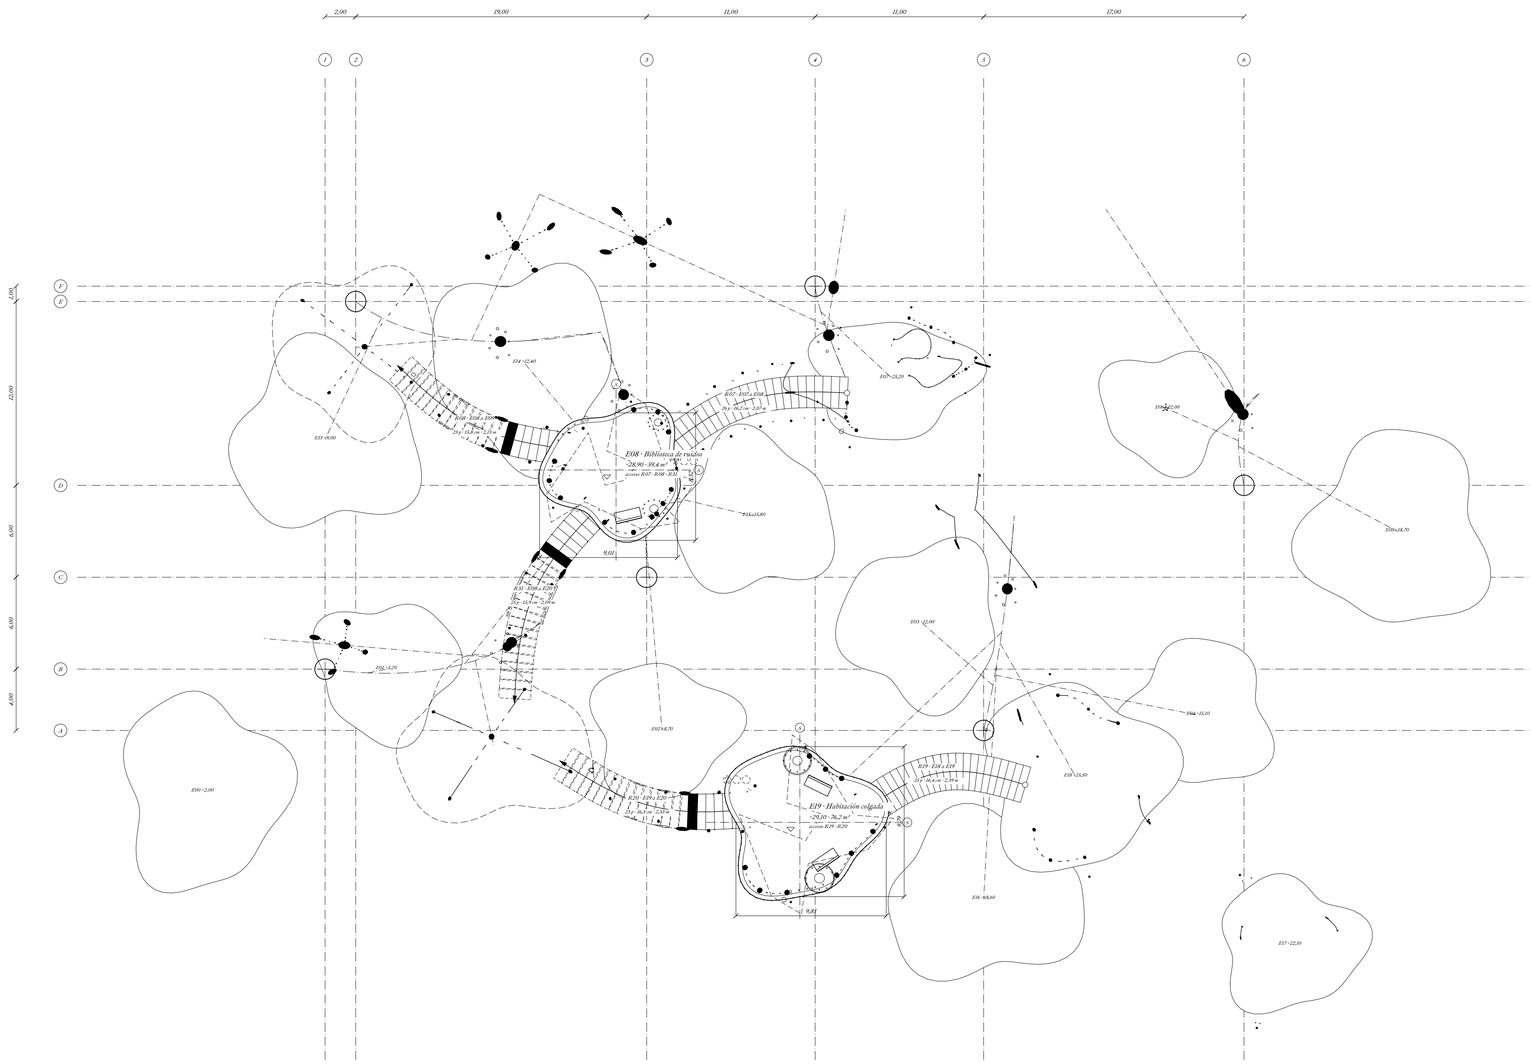


## *NIVEL*

*N09 · corte a +30,10 m*

- *1,20 m sobre el tablero de E08 (+28,90)*
- *1,00 m sobre el tablero de E19 (+29,10)*

## *PROGRAMA*

*E08 · Biblioteca de ruidos*

- *+28,90 · 59,4 m² · tablero 27 cm*
- *1 bancos con respaldo · 1 velas · 3 cilindros bajo el tablero · 3 luces sostenida por T00 · T01*

*E19 · Habitación colgada*

- *+29,10 · 76,2 m² · tablero 27 cm*
- *2 bancos con respaldo · 1 velas · 3 cilindros bajo el tablero · 3 luces sostenida por T02*

## *CONEXIONES EN ESTA PLANTA*

*R07 · llega · E07 +25,20 a E08 +28,90*

*R08 · sale · E08 +28,90 a E09 +32,10*

*R19 · llega · E18 +25,50 a E19 +29,10*

*R20 · sale · E19 +29,10 a E20 +32,40*

*R31 · sale · E08 +28,90 a E20 +32,40*

## *LECTURA DEL DIBUJO*

*Negro: todo lo cortado a la cota del corte*

*0,25 mm: tableros del nivel*

*0,10 / 0,06 mm: tableros inferiores, según profundidad*

*Discontinua larga: tableros superiores, velas y luces*

*Discontinua corta: máquinas bajo el tablero*

*Trazo-punto: troncos, ramas, malla y ejes S*

*Corte horizontal único a +30,10 m sobre toda la megaestructura: cada malla de Rhino intersecada con el plano.*


*Debajo, los tableros inferiores en proyección: el más alto tapa al más bajo. Encima, hasta 6 m, en discontinua.*

*Escaleras: línea de huella, arranque (círculo) y llegada (triángulo); peldaños por encima del corte en discontinua.*

*0 2 4 10 m*

# *Megaestructura macarra · nivel 10 · +32,10 / +32,40*

*PLANTA · E 1:200 · corte horizontal a +33,30 m · todo lo cortado en negro · lo que queda debajo en proyección*

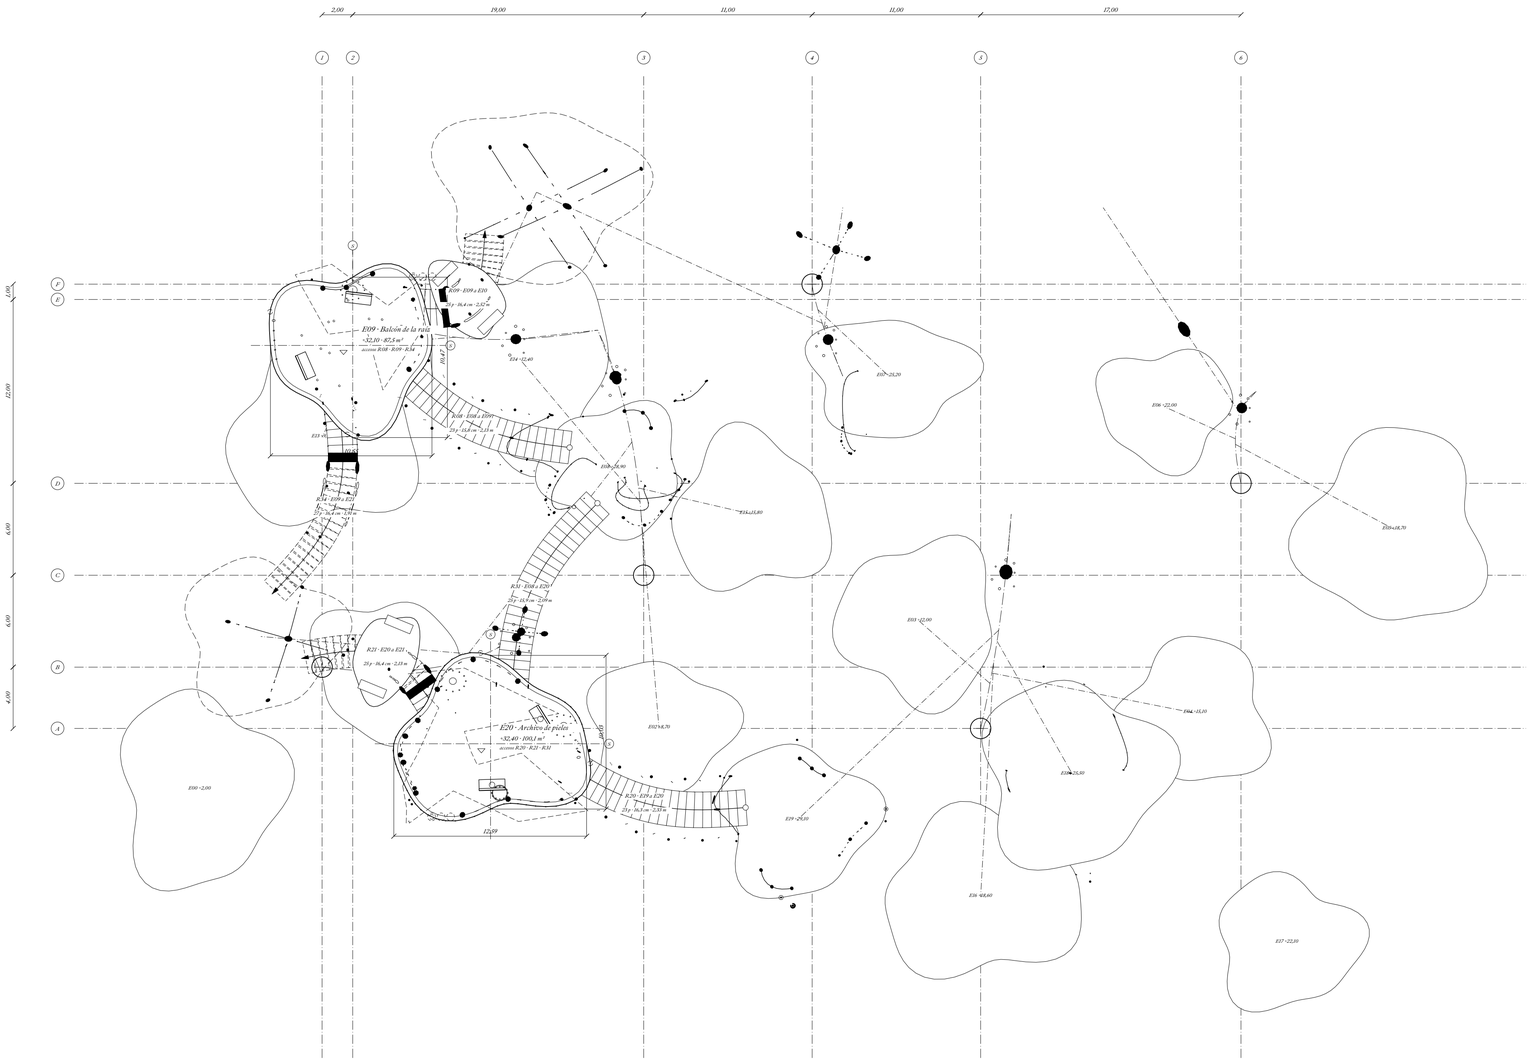


## *NIVEL*

*N10 · corte a +33,30 m*

- *1,20 m sobre el tablero de E09 (+32,10)*
- *0,90 m sobre el tablero de E20 (+32,40)*

## *PROGRAMA*

*E09 · Balcón de la raíz*

- *+32,10 · 87,5 m² · tablero 27 cm*
- *2 bancos con respaldo · 1 velas · 3 cilindros bajo el tablero · 13 luces*
- *sostenida por T05*

*E20 · Archivo de pieles*

- *+32,40 · 100,1 m² · tablero 27 cm*
- *2 bancos con respaldo · 1 velas · 3 cilindros bajo el tablero · 5 luces*
- *sostenida por T00*

## *CONEXIONES EN ESTA PLANTA*

*R08 · llega · E08 +28,90 a E09 +32,10*

*R09 · sale · E09 +32,10 a E10 +33,70*

*R20 · llega · E19 +29,10 a E20 +32,40*

*R21 · sale · E20 +32,40 a E21 +36,00*

*R31 · llega · E08 +28,90 a E20 +32,40*

*R34 · sale · E09 +32,10 a E21 +36,00*

## *LECTURA DEL DIBUJO*

*Negro: todo lo cortado a la cota del corte*

*0,25 mm: tableros del nivel*

*0,10 / 0,06 mm: tableros inferiores, según profundidad*

*Discontinua larga: tableros superiores, velas y luces*

*Discontinua corta: máquinas bajo el tablero*

*Trazo-punto: troncos, ramas, malla y ejes S*

*Corte horizontal único a +33,30 m sobre toda la megaestructura: cada malla de Rhino intersecada con el plano.*


*Debajo, los tableros inferiores en proyección: el más alto tapa al más bajo. Encima, hasta 6 m, en discontinua.*

*Escaleras: línea de huella, arranque (círculo) y llegada (triángulo); peldaños por encima del corte en discontinua.*

*0 2 4 10 m*

# *Megaestructura macarra · nivel 11 · +35,70 / +36,00*

*PLANTA · E 1:200 · corte horizontal a +36,90 m · todo lo cortado en negro · lo que queda debajo en proyección*

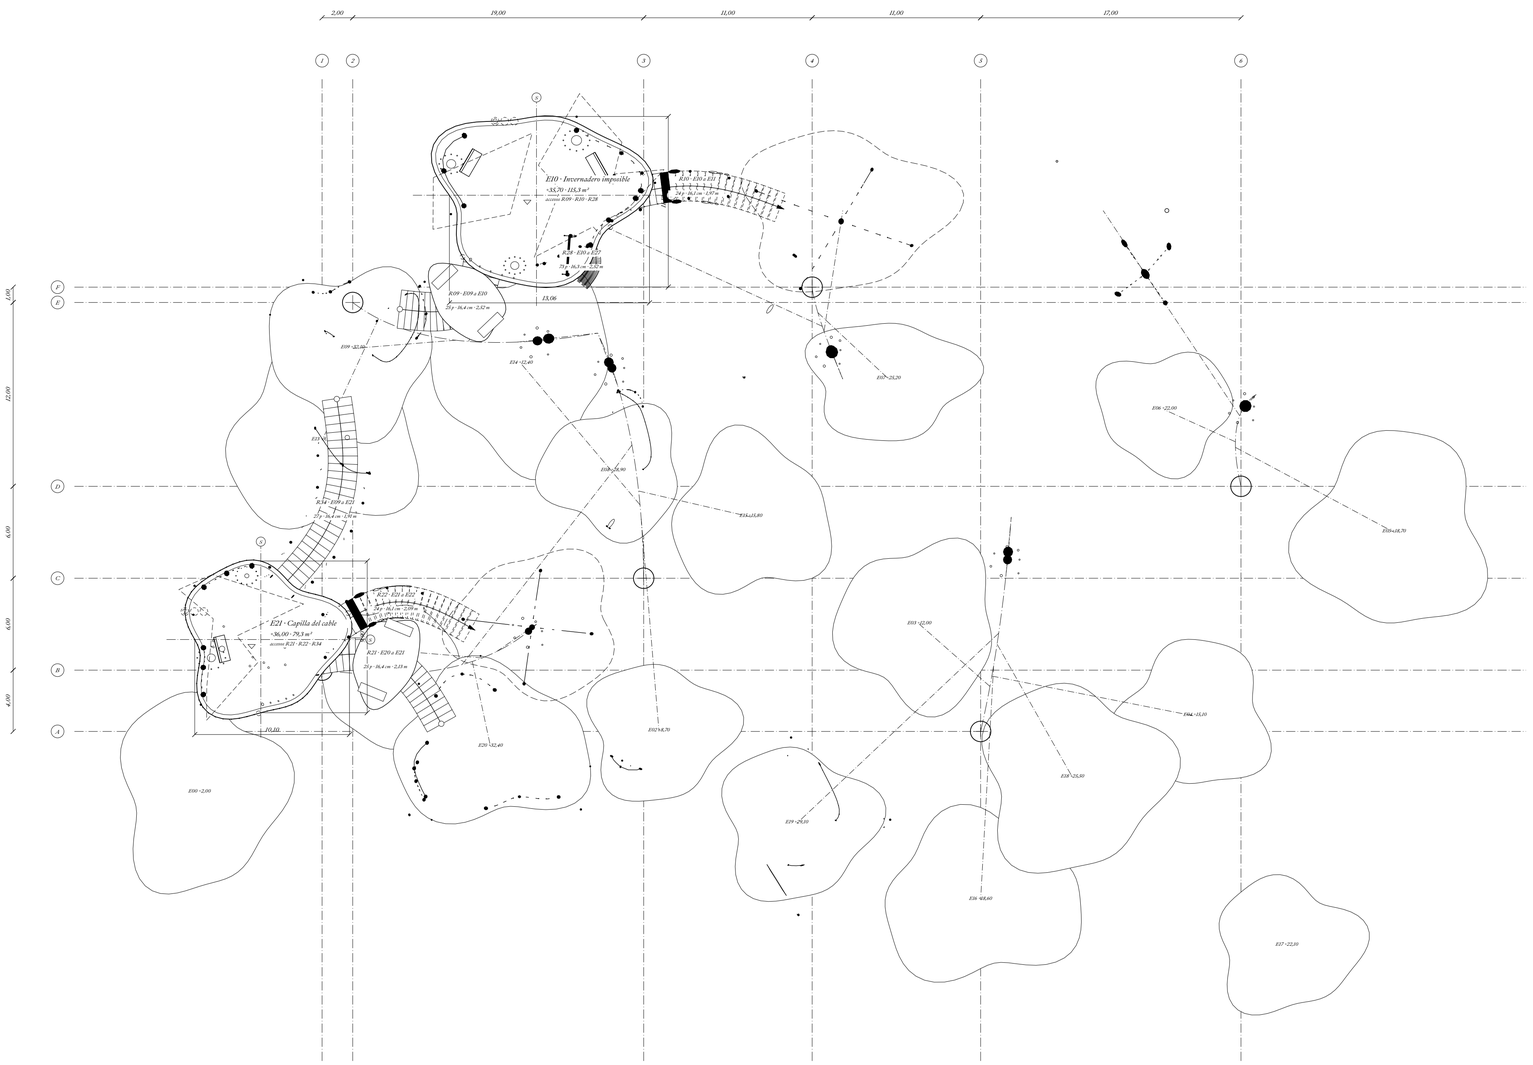


## NIVEL

*NII · corte a +36,90 m*

- *1,20 m sobre el tablero de E10 (+35,70)*
- *0,90 m sobre el tablero de E21 (+36,00)*

## PROGRAMA

*E10 · Invernadero imposible*

- *+35,70 · 115,3 m² · tablero 27 cm*
- *2 bancos con respaldo · 1 velas · 3 cilindros bajo el tablero · 3 luces*
- *sostenida por T04 · T05*

*E21 · Capilla del cable*

- *+36,00 · 79,3 m² · tablero 27 cm*
- *1 bancos con respaldo · 1 velas · 3 cilindros bajo el tablero · 13 luces*
- *sostenida por T00*

## CONEXIONES EN ESTA PLANTA

*R09 · llega · E09 +32,10 a E10 +35,70*

*R10 · sale · E10 +35,70 a E11 +35,10*

*R21 · llega · E20 +32,40 a E21 +36,00*

*R22 · sale · E21 +36,00 a E22 +39,40*

*R28 · sale · E10 +35,70 a E27 +46,20*

*R34 · llega · E09 +32,10 a E21 +36,00*

## LECTURA DEL DIBUJO

*Negro: todo lo cortado a la cota del corte*

*0,25 mm: tableros del nivel*

*0,10 / 0,06 mm: tableros inferiores, según profundidad*

*Discontinua larga: tableros superiores, velas y luces*

*Discontinua corta: máquinas bajo el tablero*

*Trazo-punto: troncos, ramas, malla y ejes S*

*Corte horizontal único a +36,90 m sobre toda la megaestructura: cada malla de Rhino intersecada con el plano.*


*Debajo, los tableros inferiores en proyección: el más alto tapa al más bajo. Encima, hasta 6 m, en discontinua.*

*Escaleras: línea de huella, arranque (círculo) y llegada (triángulo); peldaños por encima del corte en discontinua.*

0 2 4 10 m

# *Megaestructura macarra · nivel 12 · +39,10 / +39,40*

*PLANTA · E 1:200 · corte horizontal a +40,30 m · todo lo cortado en negro · lo que queda debajo en proyección*

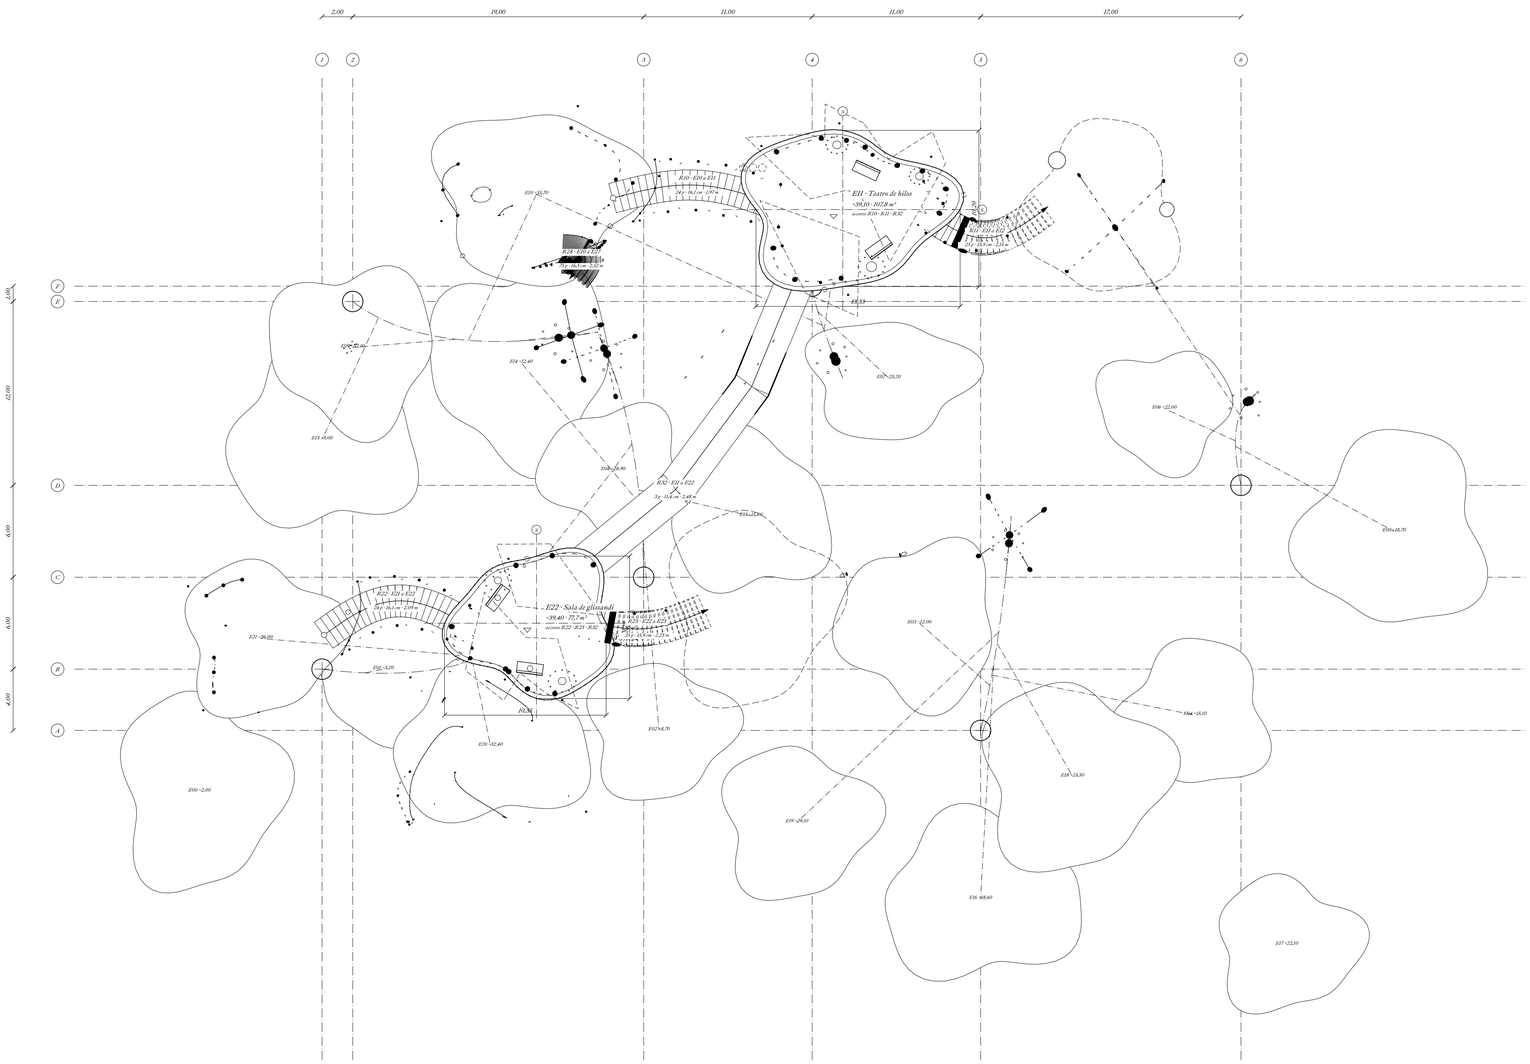


## *NIVEL*

*N12 · corte a +40,30 m*

- *1,20 m sobre el tablero de E11 (+39,10)*
- *0,90 m sobre el tablero de E22 (+39,40)*

## *PROGRAMA*

*E11 · Teatro de hilos*

- *+39,10 · 107,8 m² · tablero 27 cm*
- *2 bancos con respaldo · 1 velas · 3 cilindros bajo el tablero · 3 luces sostenida por T04*

*E22 · Sala de glissandi*

- *+39,40 · 77,7 m² · tablero 27 cm*
- *2 bancos con respaldo · 1 velas · 3 cilindros bajo el tablero · 3 luces sostenida por T00*

## *CONEXIONES EN ESTA PLANTA*

*R10 · llega · E10 -33,70 a E11 +39,10*

*R11 · sale · E11 +39,10 a E22 +42,60*

*R22 · llega · E21 -36,00 a E22 +39,40*

*R23 · sale · E22 +39,40 a E23 +42,90*

*R28 · pasa cortada · E10 -33,70 a E27 +46,20*

*R32 · sale · E11 +39,10 a E22 +39,40*

## *LECTURA DEL DIBUJO*

*Negro: todo lo cortado a la cota del corte*

*0,25 mm: tableros del nivel*

*0,10 / 0,06 mm: tableros inferiores, según profundidad*

*Discontinua larga: tableros superiores, velas y luces*

*Discontinua corta: máquinas bajo el tablero*

*Trazo-punto: troncos, ramas, malla y ejes S*

*Corte horizontal único a +40,30 m sobre toda la megaestructura: cada malla de Rhino intersecada con el plano.*


*Debajo, los tableros inferiores en proyección: el más alto tapa al más bajo. Encima, hasta 6 m, en discontinua.*

*Escaleras: línea de huella, arranque (círculo) y llegada (triángulo); peldaños por encima del corte en discontinua.*

*0 2 4 10 m*

# *Megaestructura macarra · nivel 13 · +42,60 / +42,90*

*PLANTA · E 1:200 · corte horizontal a +43,80 m · todo lo cortado en negro · lo que queda debajo en proyección*

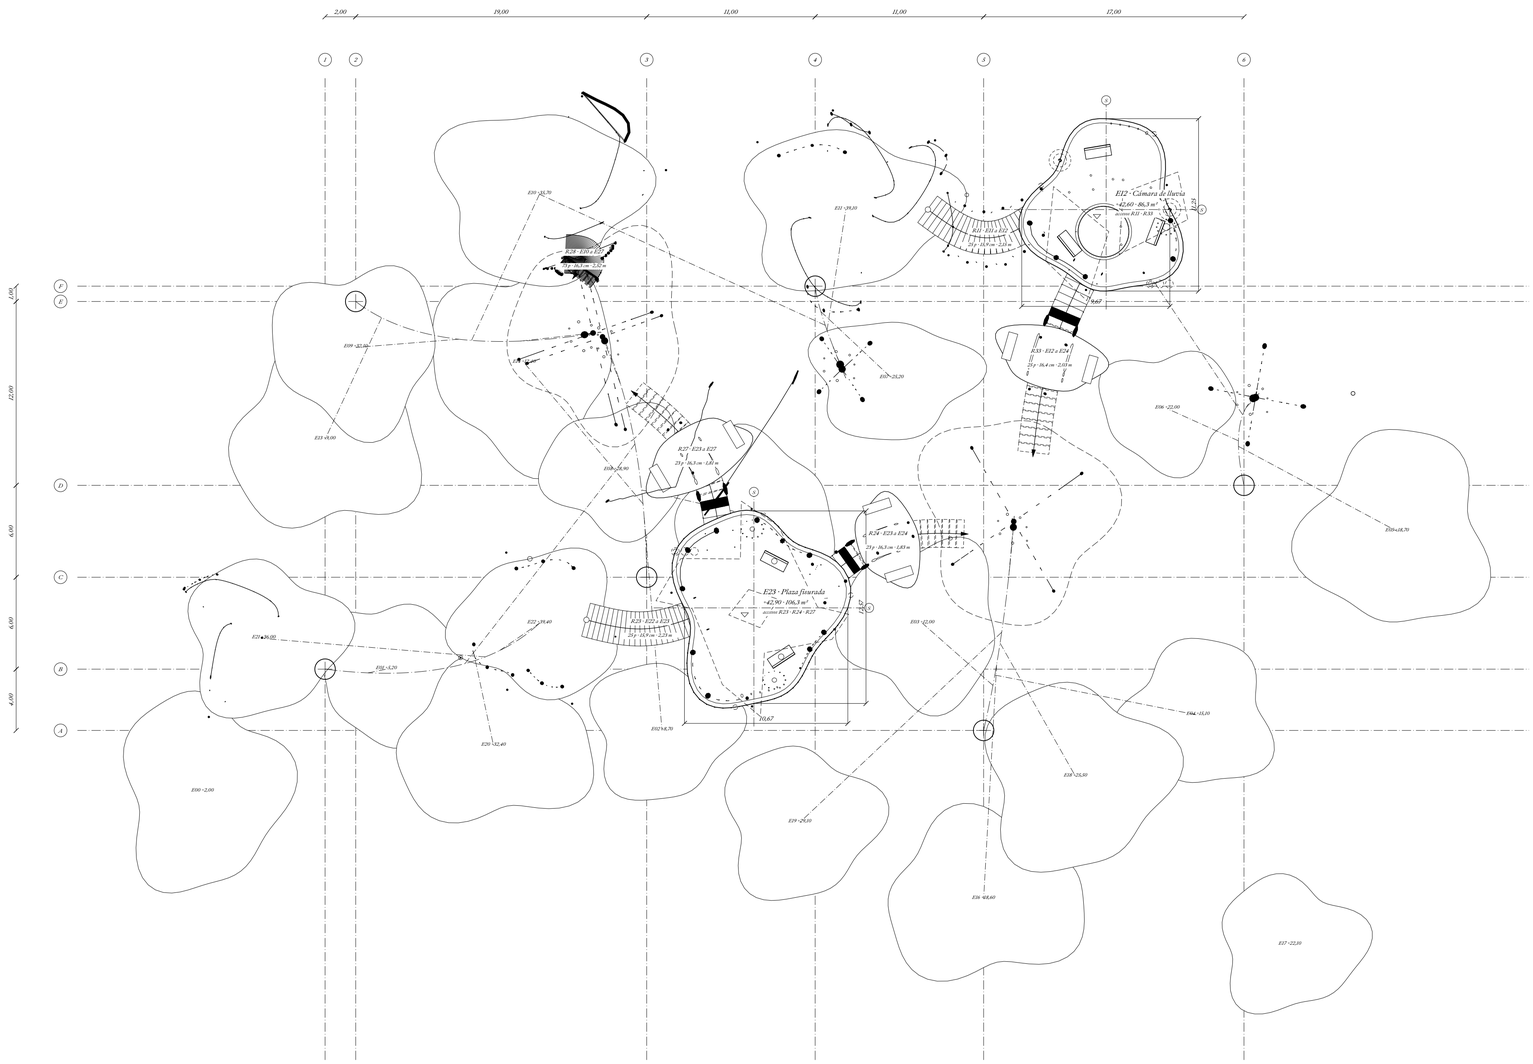


## NIVEL

*N13 · corte a +43,80 m*

- *1,20 m sobre el tablero de E12 (+42,60)*
- *0,90 m sobre el tablero de E23 (+42,90)*

## PROGRAMA

*E12 · Cámara de lluvia*

- *+42,60 · 86,3 m² · tablero 27 cm*
- *3 bancos con respaldo · 1 velas · 3 cilindros bajo el tablero · 13 luces · cuenco de agua y tuvijas colgadas*
- *sostenida por T03*

*E23 · Plaza fisurada*

- *+42,90 · 106,3 m² · tablero 27 cm*
- *2 bancos con respaldo · 1 velas · 3 cilindros bajo el tablero · 5 luces*
- *sin rama de tronco propia*

## CONEXIONES EN ESTA PLANTA

*R11 · llega · E11 +39,10 a E12 +42,60*

*R23 · llega · E22 +39,40 a E23 +42,90*

*R24 · sale · E23 +42,90 a E24 +46,20*

*R27 · sale · E23 +42,90 a E27 +46,20*

*R28 · pasa cortada · E10 +33,70 a E27 +46,20*

*R33 · sale · E12 +42,60 a E24 +46,20*

## LECTURA DEL DIBUJO

*Negro: todo lo cortado a la cota del corte*

*0,25 mm: tableros del nivel*

*0,10 / 0,06 mm: tableros inferiores, según profundidad*

*Discontinua larga: tableros superiores, velas y luces*

*Discontinua corta: máquinas bajo el tablero*

*Trazo-punto: troncos, ramas, malla y ejes S*

*Corte horizontal único a +43,80 m sobre toda la megaestructura: cada malla de Rhino intersecada con el plano.*


*Debajo, los tableros inferiores en proyección; el más alto tapa al más bajo. Encima, hasta 6 m, en discontinua.*

*Escaleras: línea de huella, arranque (círculo) y llegada (triángulo); peldaños por encima del corte en discontinua.*

*0 2 4 10 m*

# *Megaestructura macarra · nivel 14 · +46,20 / +46,20*

*PLANTA · E 1:200 · corte horizontal a +47,40 m · todo lo cortado en negro · lo que queda debajo en proyección*

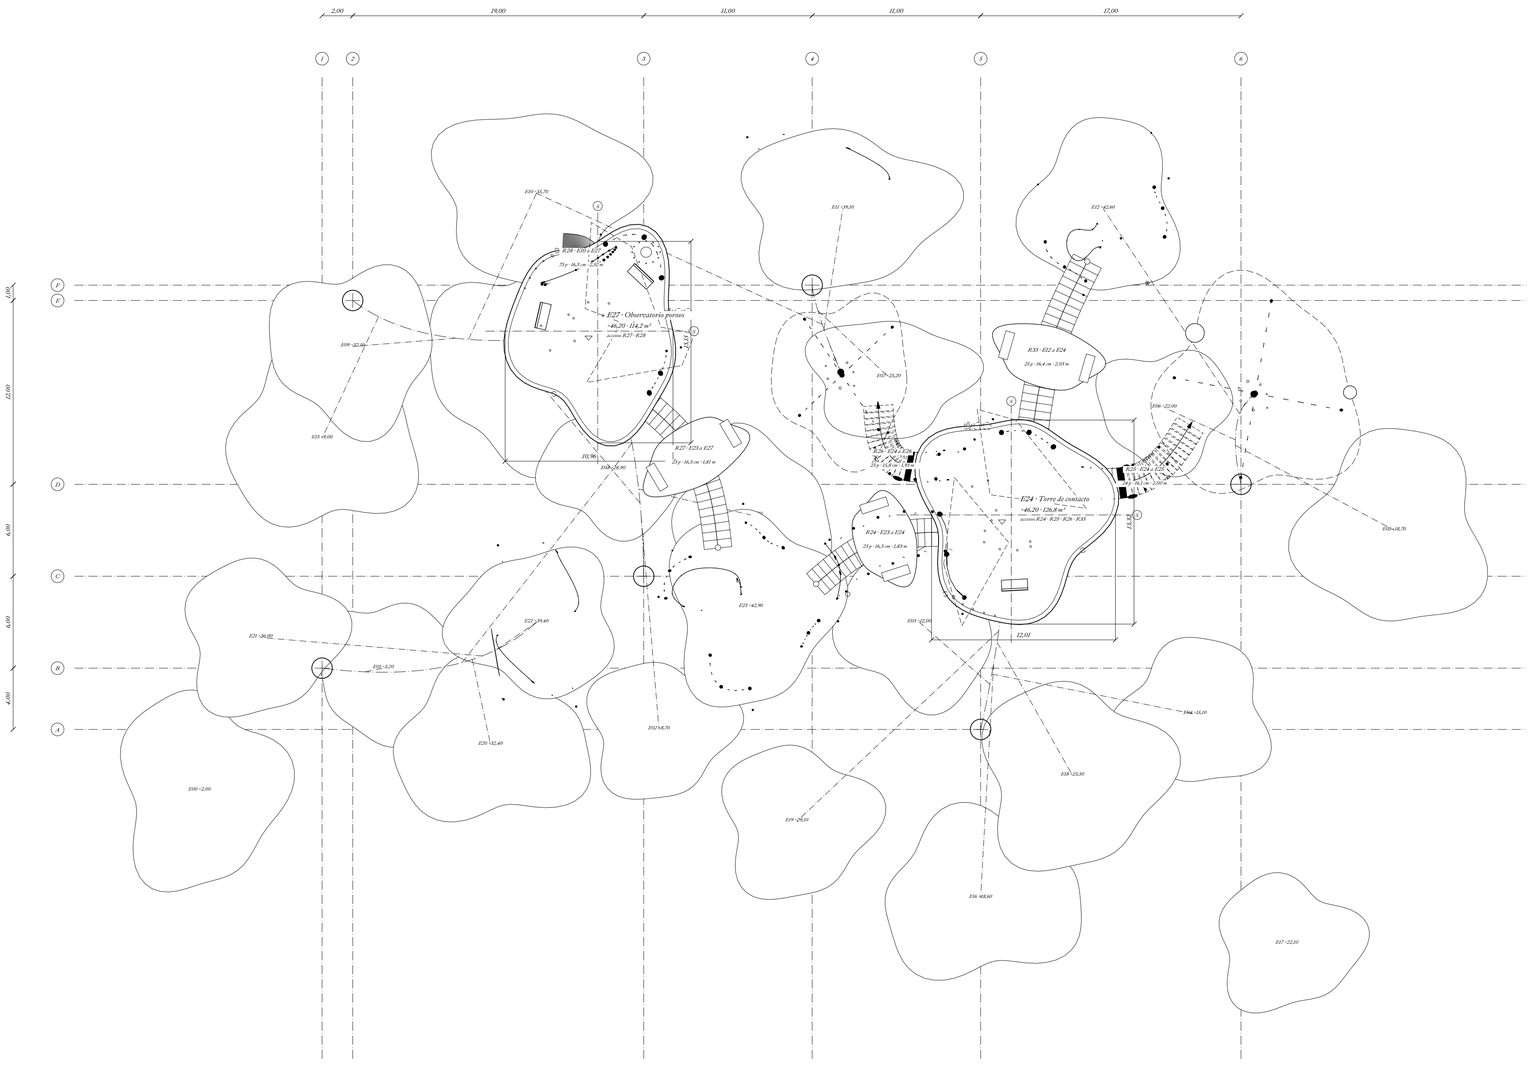


## *NIVEL*

***N14 · corte a +47,40 m***

- *1,20 m sobre el tablero de E24 (+46,20)*
- *1,20 m sobre el tablero de E27 (+46,20)*

## *PROGRAMA*

***E24 · Torre de contacto***

- *+46,20 · 126,8 m² · tablero 27 cm*
- *1 bancos con respaldo · 1 velas · 3 cilindros bajo el tablero · 13 luces*
- *sostenida por T02*

***E27 · Observatorio poroso***

- *+46,20 · 114,2 m² · tablero 27 cm*
- *2 bancos con respaldo · 1 velas · 3 cilindros bajo el tablero · 13 luces*
- *sostenida por T01 · T05*

## *CONEXIONES EN ESTA PLANTA*

*R24 · llega · E23 +42,90 a E24 +46,20*

*R25 · sale · E24 +46,20 a E25 +49,60*

*R26 · sale · E24 +46,20 a E26 +49,40*

*R27 · llega · E23 +42,90 a E27 +46,20*

*R28 · llega · E10 +33,70 a E27 +46,20*

*R33 · llega · E12 +42,60 a E24 +46,20*

## *LECTURA DEL DIBUJO*

*Negro: todo lo cortado a la cota del corte*

*0,25 mm: tableros del nivel*

*0,10 / 0,06 mm: tableros inferiores, según profundidad*

*Discontinua larga: tableros superiores, velas y luces*

*Discontinua corta: máquinas bajo el tablero*

*Trazo-punto: troncos, ramas, malla y ejes S*

*Corte horizontal único a +47,40 m sobre toda la megaestructura; cada malla de Rhino intersecada con el plano.*


*Debajo, los tableros inferiores en proyección: el más alto tapa al más bajo. Encima, hasta 6 m, en discontinua.*

*Escaleras: línea de huella, arranque (círculo) y llegada (triángulo); peldaños por encima del corte en discontinua.*

*0 2 4 10 m*

# *Megaestructura macarra · nivel 15 · +49,40 / +49,60*

*PLANTA · E 1:200 · corte horizontal a +50,60 m · todo lo cortado en negro · lo que queda debajo en proyección*

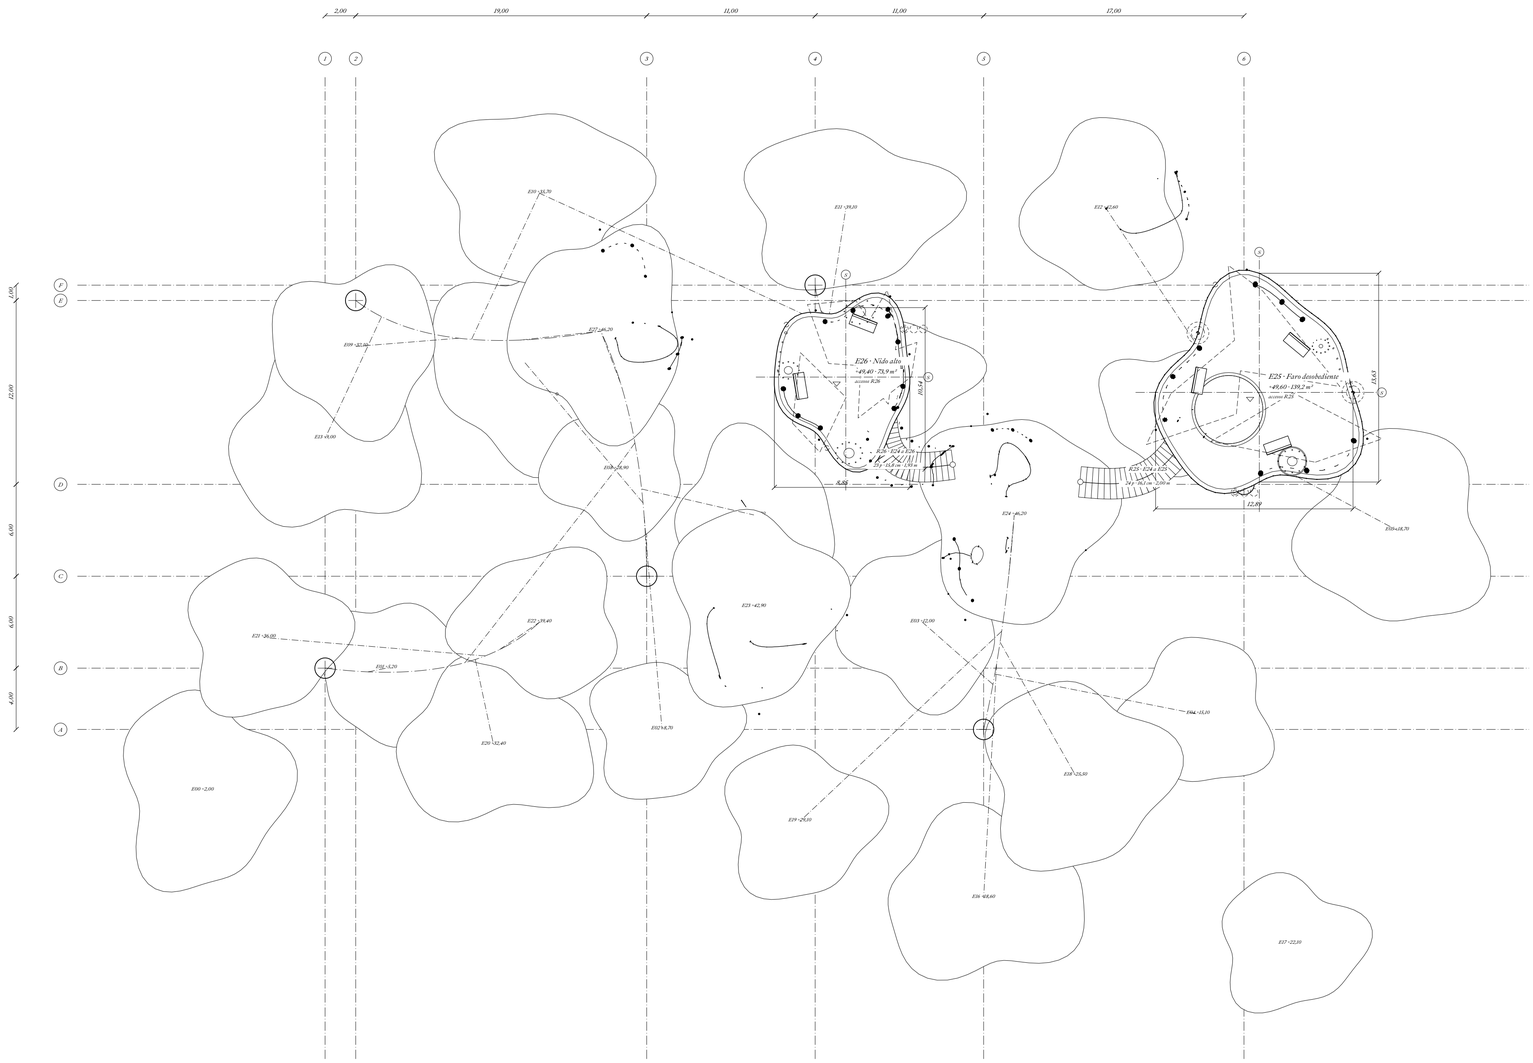


## NIVEL

*N15 · corte a +50,60 m*

- *1,20 m sobre el tablero de E26 (+49,40)*
- *1,00 m sobre el tablero de E25 (+49,60)*

## PROGRAMA

*E26 · Nido alto*

- *+49,40 · 73,9 m² · tablero 27 cm*
- *2 bancos con respaldo · 1 velas · 3 cilindros bajo el tablero · 3 luces*
- *sostenida por T04*

*E25 · Faro desobediente*

- *+49,60 · 139,2 m² · tablero 27 cm*
- *3 bancos con respaldo · 1 velas · 3 cilindros bajo el tablero · 3 luces · cuenco de agua y tarifas colgadas*
- *sostenida por T03*

## CONEXIONES EN ESTA PLANTA

*R25 · liga · E24 +46,20 a E25 +49,60*

*R26 · liga · E24 +46,20 a E26 +49,40*

## LECTURA DEL DIBUJO

*Negro: todo lo cortado a la cota del corte*

*0,25 mm: tableros del nivel*

*0,10 / 0,06 mm: tableros inferiores, según profundidad*

*Discontinua larga: tableros superiores, velas y luces*

*Discontinua corta: máquinas bajo el tablero*

*Trazo-punto: troncos, ramas, malla y ejes S*

*Corte horizontal único a +50,60 m sobre toda la megaestructura: cada malla de Rhino intersecada con el plano.*


*Debajo, los tableros inferiores en proyección; el más alto tapa al más bajo. Encima, hasta 6 m, en discontinua.*

*Escaleras: línea de huella, arranque (círculo) y llegada (triángulo); peldaños por encima del corte en discontinua.*

*0 2 4 10 m*

# *Megaestructura macarra · sección A*

*SECCIÓN · E 1:200 · longitudinal por y = +3,00, mirando a norte · corte exacto y líneas ocultas de Rhino*

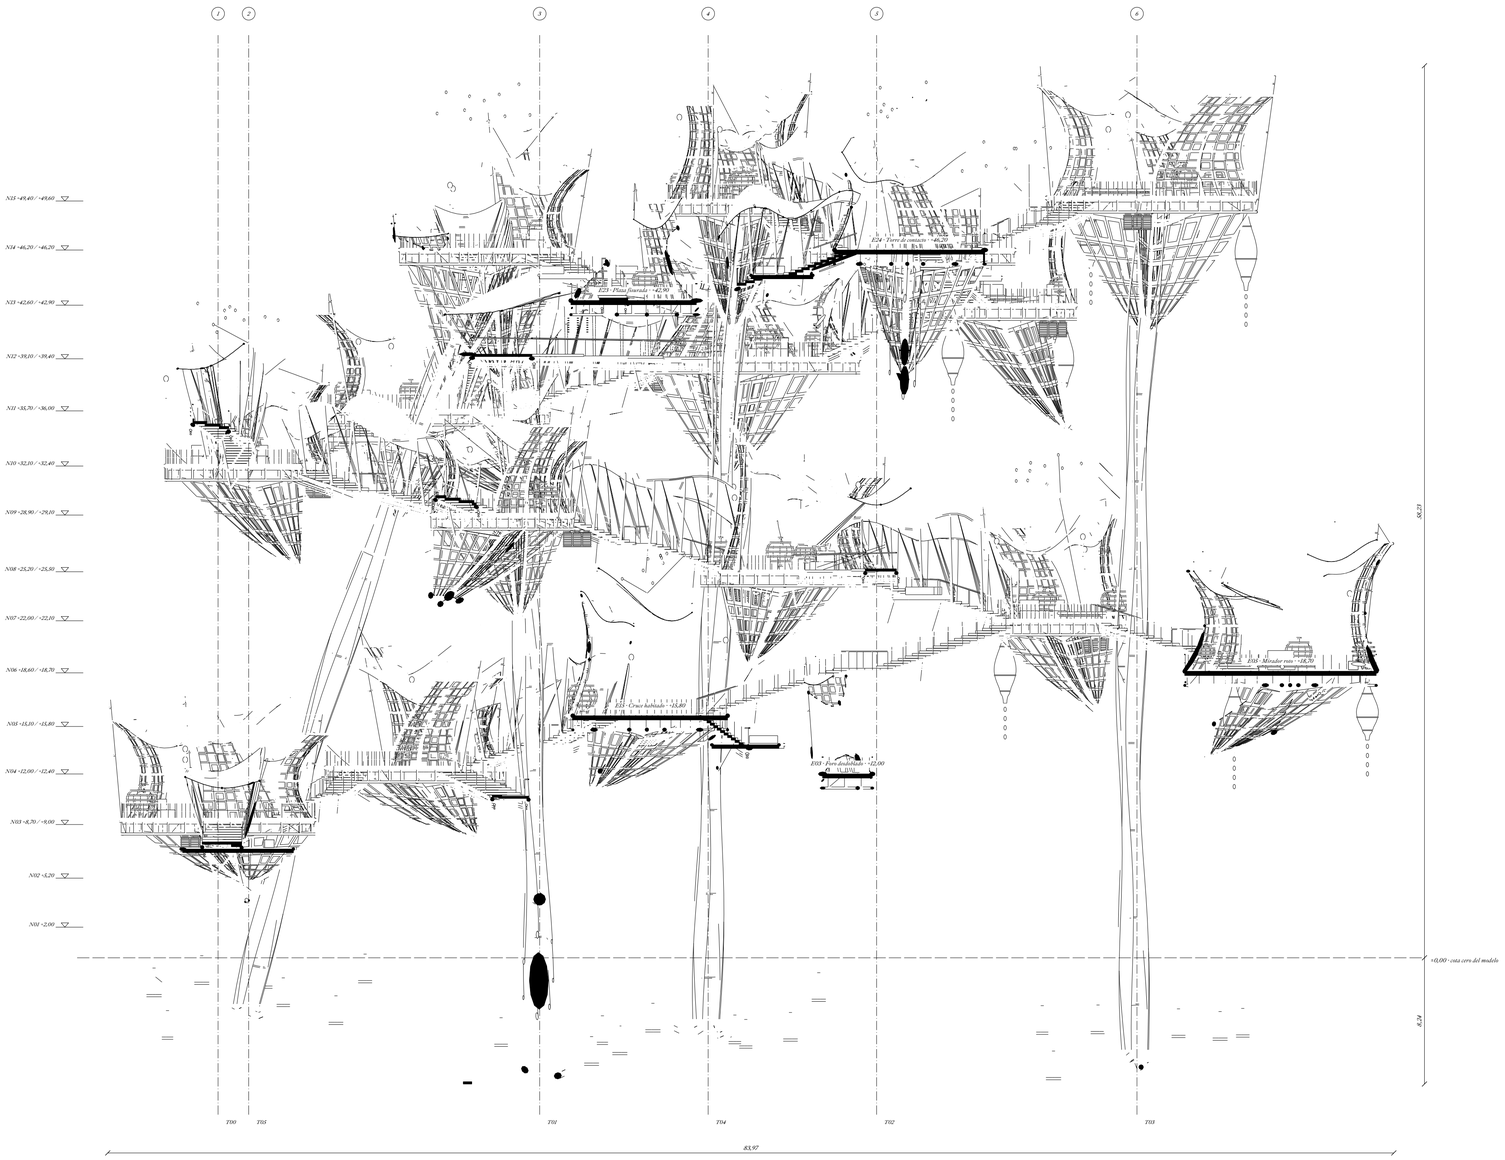


## *SECCIÓN A*

*longitudinal por y = +3,00, mirando a norte*

## *ESTANCIAS CORTADAS*

*E03 · Foro doubleblade · +12,00*

*E05 · Mirador roto · +18,70*

*E15 · Cruce habitado · +15,80*

*E23 · Plaza fisurada · +42,90*

*E24 · Torre de contacto · +46,20*

## *ESCALERAS CORTADAS*

*R17 · R15 · R24 · R27 · R30 · R31 · R32 · R34 · R35*

## *TRONCOS CORTADOS*

*T00 · T01 · T02 · T03*

## *LECTURA DEL DIBUJO*

*Negro: tableros, bordes, peldaños, troncos, costillas y células cortadas*

*0,13 mm blanco: mobiliario, máquinas, depósitos y conductos cortados*

*0,09 mm: contornos aparentes de lo que queda detrás*

*0,05 mm: aristas, tensores, velas y células detrás*

*Izquierda: los quince niveles N01-N15*

*Trazo-punto: ejes de la malla de troncos*

*Plano vertical por longitudinal por y = +3: cada malla de Rhino intersecada con el plano (negro) y líneas ocultas de Rhino de lo que queda detrás.*

*De los tubos (bordes, barandillas, troncos, costillas, tensores, nervios) solo se dibuja su contorno aparente, no las aristas de faceta.*

*El modelo no tiene terreno: la línea ±0,00 es la cota cero del archivo. Las raíces de los troncos bajan hasta −8,24 m.*

*0 2 4 10 m*

# *Megaestructura macarra · sección B*

*SECCIÓN · E 1:200 · transversal por x = 0,00, mirando a levante · corte exacto y líneas ocultas de Rhino*

F E D C B A

N15 · 49,40 / · 49,60

N14 · 46,20 / · 46,20

N13 · 42,60 / · 42,90

N12 · 39,10 / · 39,40

N11 · 33,70 / · 36,00

N10 · 32,10 / · 32,40

N09 · 28,90 / · 29,10

N08 · 25,20 / · 25,80

N07 · 22,00 / · 22,10

N06 · 18,60 / · 18,70

N05 · 15,10 / · 15,80

N04 · 12,00 / · 12,40

N03 · 8,70 / · 9,00

N02 · 5,20

N01 · 2,00

E31 · Teatro de hilos · +39,10

E23 · Plaza finurada · +42,90

E03 · Cruce habitado · +15,80

T04 T05 T03 T01 T00 T02

60,53

8,54

±0,00 · cota cero del modelo

## *SECCIÓN B*

*transversal por x = 0,00, mirando a levante*

## *ESTANCIAS CORTADAS*

*E31 · Teatro de hilos · +39,10*

*E15 · Cruce habitado · +15,80*

*E23 · Plaza finurada · +42,90*

*E26 · Nido alto · +49,40*

## *ESCALERAS CORTADAS*

*R02 · R07 · R32*

## *TRONCOS CORTADOS*

*T02 · T04*

## *LECTURA DEL DIBUJO*

*Negro: tableros, bordes, peldaños, troncos, costillas y células cortadas*

*0,13 mm blanco: mobiliario, máquinas, depósitos y conductos cortados*

*0,09 mm: contornos aparentes de lo que queda detrás*

*0,05 mm: aristas, tensores, velas y células detrás*

*Izquierda: los quince niveles N01-N15*

*Trazo-punto: ejes de la malla de troncos*

*Plano vertical por transversal por x = 0: cada malla de Rhino intersecada con el plano (negro) y líneas ocultas de Rhino de lo que queda detrás.*


*De los tubos (bordes, barandillas, troncos, costillas, tensores, nervios) solo se dibuja su contorno aparente, no las aristas de faceta.*

*El modelo no tiene terreno: la línea ±0,00 es la cota cero del archivo. Las raíces de los troncos bajan hasta −8,24 m.*

0 2 4 10 m

# *Megaestructura macarra · sección C*

*SECCIÓN · E:1:200 · longitudinal por el eje A de la malla, mirando a norte · corte exacto y líneas ocultas de Rhino*

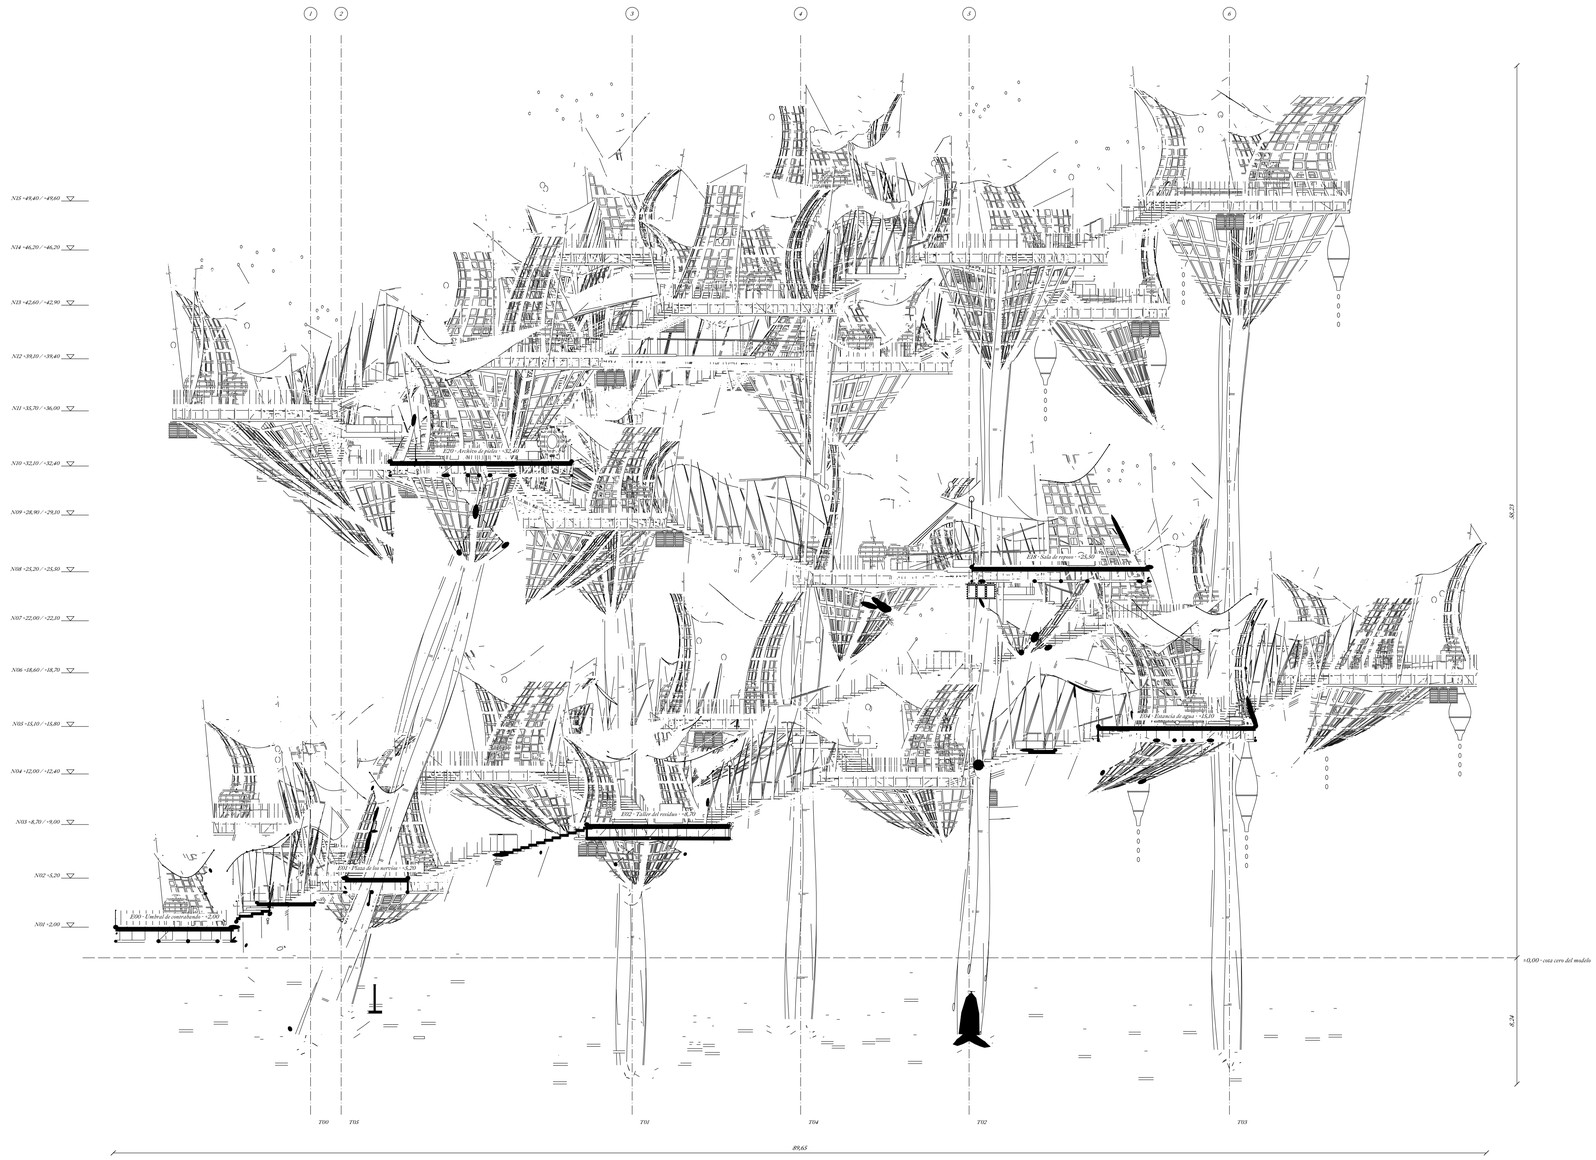


## *SECCIÓN C*

*longitudinal por el eje A de la malla, mirando a norte*

## *ESTANCIAS CORTADAS*

*E00 · Umbral de contrabando · +2,00*

*E01 · Plaza de los nervios · +5,20*

*E02 · Taller del residuo · +8,70*

*E04 · Estancia de agua · +15,10*

*E18 · Sala de reposo · +25,50*

*E20 · Archivo de pieles · +32,40*

## *ESCALERAS CORTADAS*

*R00 · R01 · R21*

## *TRONCOS CORTADOS*

*T00 · T01 · T02*

## *LECTURA DEL DIBUJO*

*Negro: tableros, bordes, peldaños, troncos, costillas y células cortadas*

*0,13 mm blanco: mobiliario, máquinas, depósitos y conductos cortados*

*0,09 mm: contornos aparentes de lo que queda detrás*

*0,05 mm: aristas, tensores, velas y células detrás*

*Izquierda: los quince niveles N00-N15*

*Trazo-punto: ejes de la malla de troncos*

*Plano vertical por longitudinal por el eje A de la malla: cada malla de Rhino intersecada con el plano (negro) y líneas ocultas de Rhino de lo que queda detrás.*


*De los tubos (bordes, barandillas, troncos, costillas, tensores, nervios) solo se dibuja su contorno aparente, no las aristas de faceta.*

*El modelo no tiene terreno: la línea +0,00 es la cota cero del archivo. Las raíces de los troncos bajan hasta −8,24 m.*

*0 2 4 10 m*

# *Megaestructura macarra · sección D*

*SECCIÓN · E:1:200 · transversal por el eje 6 de la malla, mirando a poniente · corte exacto y líneas ocultas de Rhino*

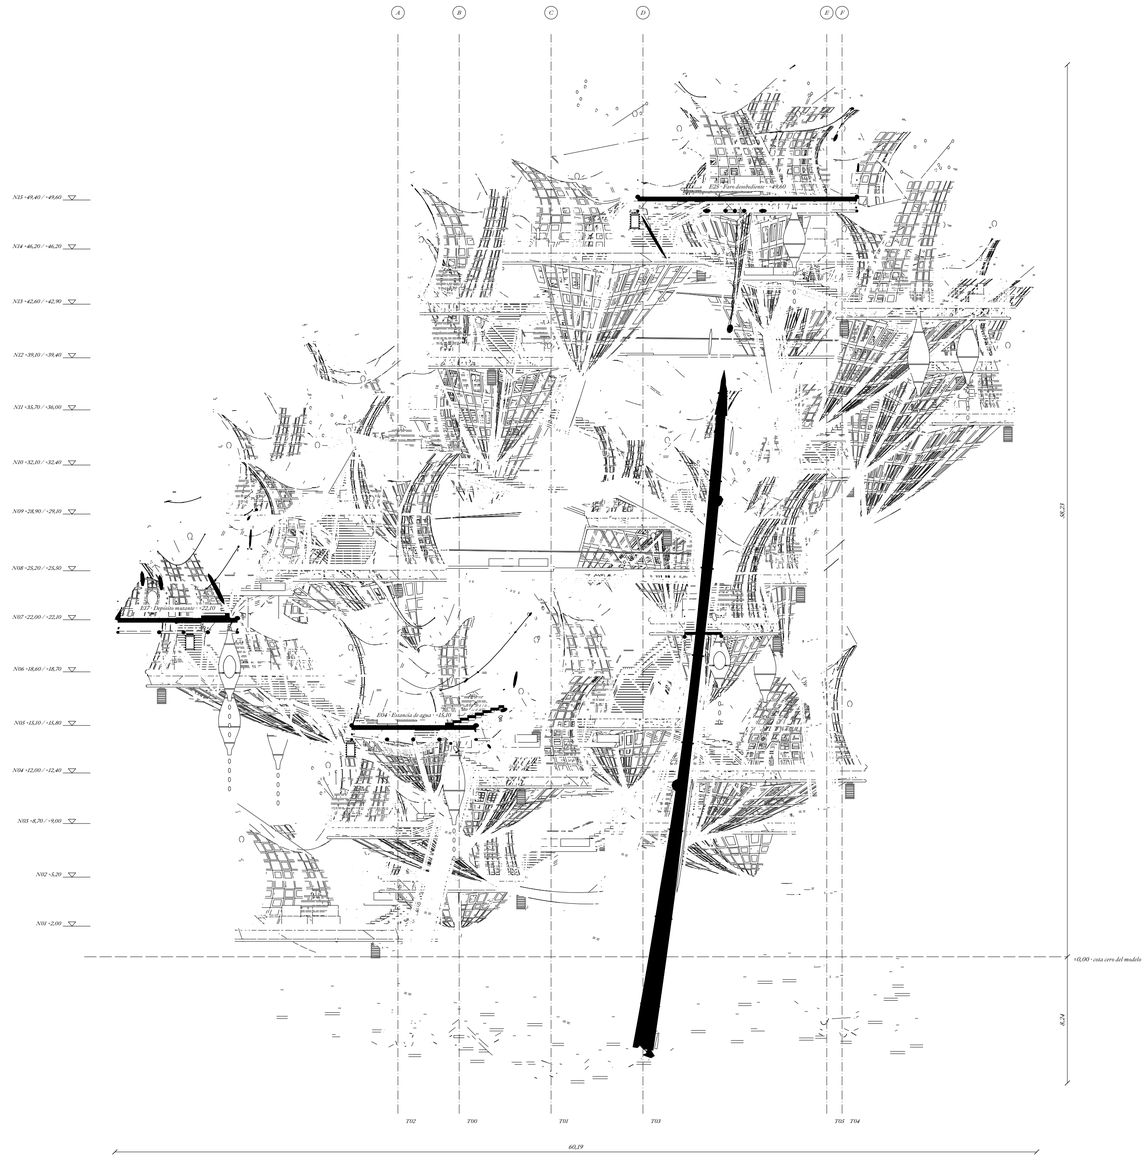


## *SECCIÓN D*

*transversal por el eje 6 de la malla, mirando a poniente*

## *ESTANCIAS CORTADAS*

*E04 · Estancia de agua · +15,10*

*E27 · Depósito mazanas · +22,10*

*E25 · Faro desobediente · +49,60*

## *ESCALERAS CORTADAS*

*R04 · R05 · R17 · R18*

## *TRONCOS CORTADOS*

*T03*

## *LECTURA DEL DIBUJO*

*Negro: tableros, bordes, peldaños, troncos, costillas y células cortadas*

*0,13 mm blanco: mobiliario, máquinas, depósitos y conductos cortados*

*0,09 mm: contornos aparentes de lo que queda detrás*

*0,05 mm: aristas, tensores, velas y células detrás*

*Izquierda: los quince niveles N01-N15*

*Trazo-punto: ejes de la malla de tronco*

*Plano vertical por transversal por el eje 6 de la malla: cada malla de Rhino intersecada con el plano (negro) y líneas ocultas de Rhino de lo que queda detrás.*

*De los tubos (bordes, barandillas, troncos, costillas, tensores, nervios) solo se dibuja su contorno aparente, no las aristas de facets.*

*El modelo no tiene terreno: la línea +0,00 es la cota cero del archivo. Las raíces de los troncos bajan hasta −8,24 m.*

*0 2 4 10 m*