


Racimo de cuatro

derivado de N19B · planta 1:50 · nivel tipo

4 habitaciones	4 × 12,02	48,1 m²
2 baños	2 × 3,89	7,8 m²
suelo común	cocina, comer, estar, paso	48,0 m²
útil		103,8 m²
construida	11,10 × 10,80	119,9 m²
por persona	útil / construida	26,0 / 30,0

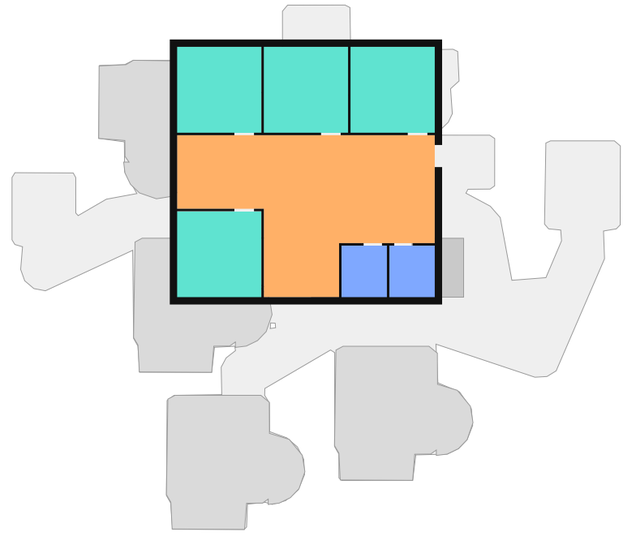

N19B (gris) y racimo (color) a la misma escala, 1:250

suelo 273,6 → 103,8 m² útiles · caja 24,8 × 21,4 → 11,1 × 10,8 m

recorridos medios, m	N19B	racimo
habitación ↔ habitación	8,6	5,0
habitación → baño	5,9	5,6
habitación → cocina	10,5	7,2
entrada → habitación	12,5	5,5

por el suelo libre, esquivando muebles; N19B medido en su modelo 3D

- habitación · cama 1,25 × 2,00, tablero plegable, armario curvo, Ø 1,50 libre
- suelo común continuo de la calle a la plataforma
- baños contra la medianera, patinillo al núcleo
- ventana


Salen al zócalo de PB: cortar/coser (T), reparar (R), bici (G) y secar (D).

Se queda: dormir, trabajar, cocinar, comer, estar y lavarse.


Habitación 3,43 × 3,50 m: el círculo libre de 1,50 m cabe sin tocar muebles.

Suelo común con círculo inscrito de 4,57 m; 39 m² admiten un círculo de 3 m.

Muro exterior 0,30 · tabique 0,10 · altura libre 2,80 · forjado 0,30.

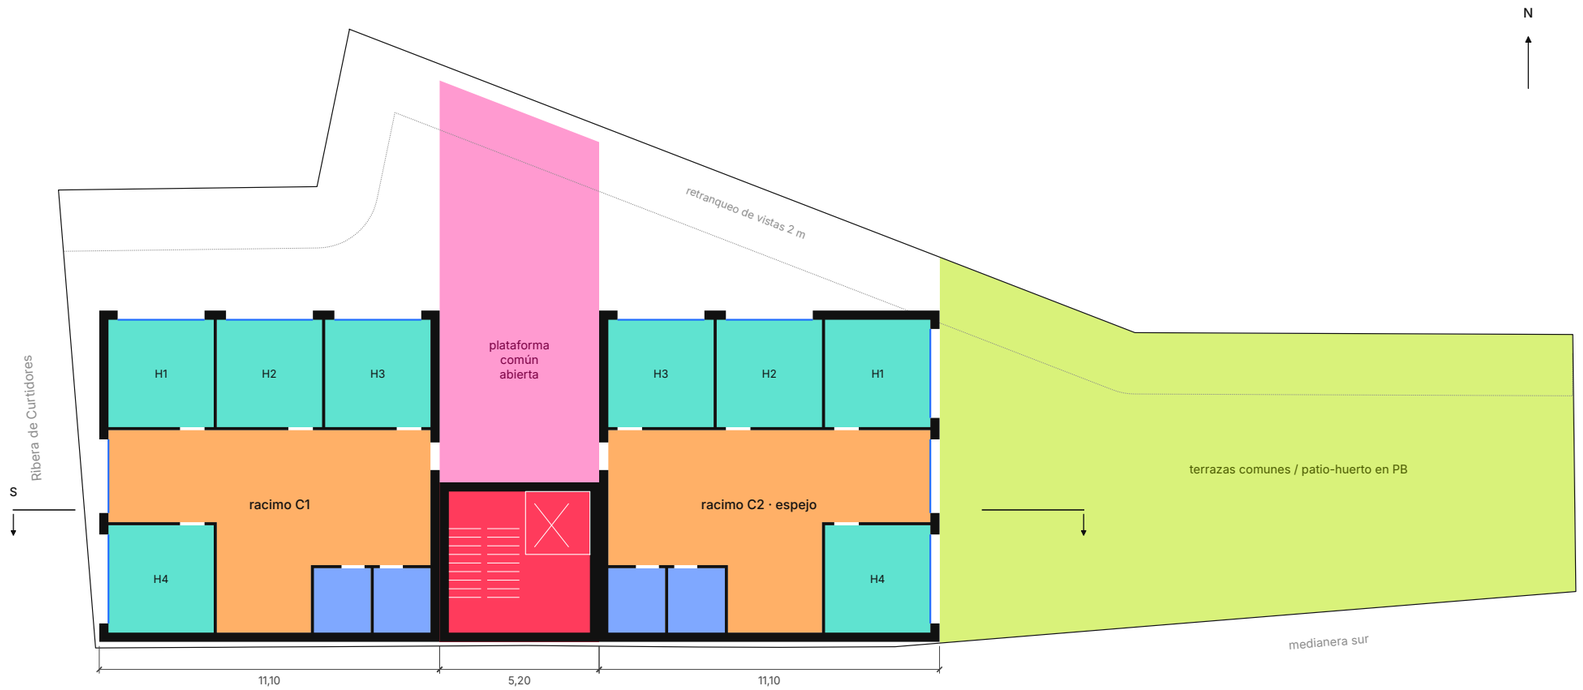

planta tipo, niveles +8,00 a +20,40 · 1:200

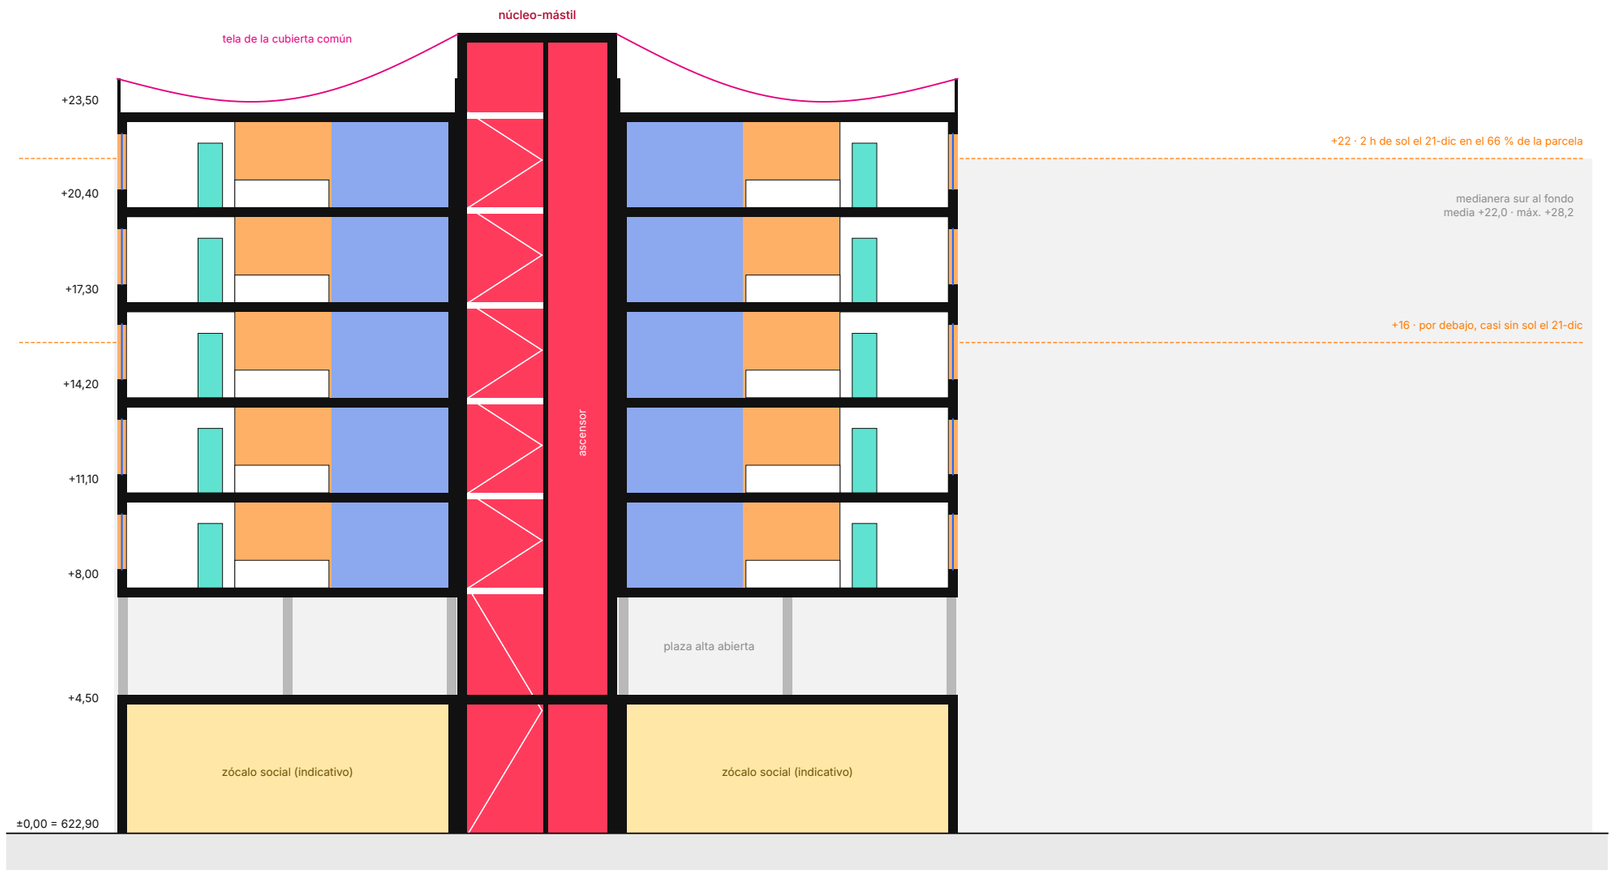

sección S por el suelo común de los racimos, mirando al sur · 1:200

Diez racimos en la parcela

dos por planta, uno a cada lado del núcleo

niveles

±0,00	zócalo social y pasaje al patio (indicativo)
+4,50	plaza alta abierta, sólo estructura
+8,00 a +20,40	5 plantas × 2 racimos = 40 personas
+23,50	cubierta común bajo la tela
cada 3,10 m	forjado 0,30 · altura libre 2,80

superficie construida, m²

10 racimos	10 × 119,9	1.198,8
núcleo	8 niveles × 27,0	216,3
zócalo PB (indicativo)	2 × 119,9	239,8
total	enunciado ≈ 1.500 (+10 %)	**1.654,9**

plataformas abiertas (6 × 63,7) no computadas

comprobado sobre el modelo

Todo dentro del contorno de Catastro (651 m²).
Cada ventana tiene 2 m libres delante dentro de la parcela o da a la calle (art. 582 del Código Civil, vistas rectas).
Puerta del racimo → escalera: 1,9 m (C1) y 4,2 m (C2); máx. 25 m (DB SI 3).
Altura de evacuación +20,40: escalera protegida (DB SI 3, entre 14 y 28 m).
Escalera: tramos 1,05 m, huella 0,28, contrahuella 0,172, mesetas 1,15 (DB SUA 1: ≥ 1,00 · ≥ 0,28 · ≤ 0,185 · ≥ 1,00).
Barandilla de 1,10 m en plataformas (DB SUA 1, desnivel > 6 m).
Ascensor con cabina 1,10 × 1,40 junto a la escalera.

por decidir

Altura máxima del Centro Histórico (cubierta +23,50, medianera +22 / +28,2).
Sol: las plantas +8 y +11 quedan bajo +16; la luz les llega de norte, calle y fondo.
Estructura: apoyar en el zócalo o colgar los racimos del núcleo-mástil.
Figura legal: vivienda compartida de 4 (2 baños) o residencia compartida (dormitorio con baño en cada unidad).

- habitación
- suelo común
- baños
- núcleo-mástil
- plataforma
- fondo común
- umbral de sol