
Centros para convivir


Vivienda temporal para jóvenes en Ribera de Curtidores 31

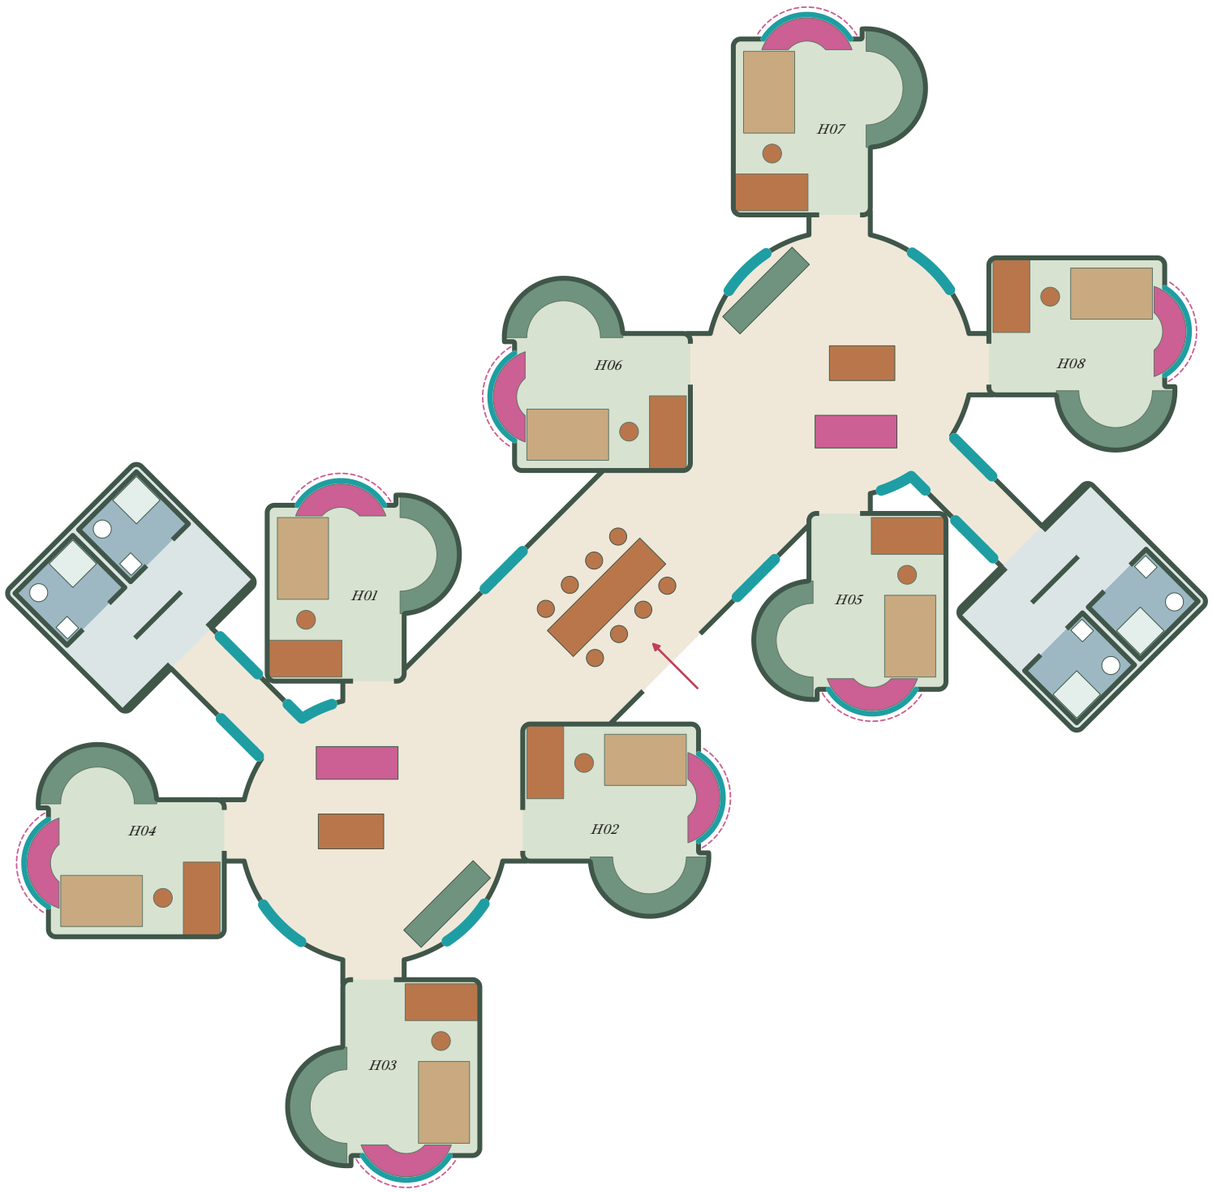

Cuaderno de plantas

G3 Proyectos · Universidad Europea de Madrid · Octubre 2026

Llegar, cocinar, acompañar, retirarse, volver.

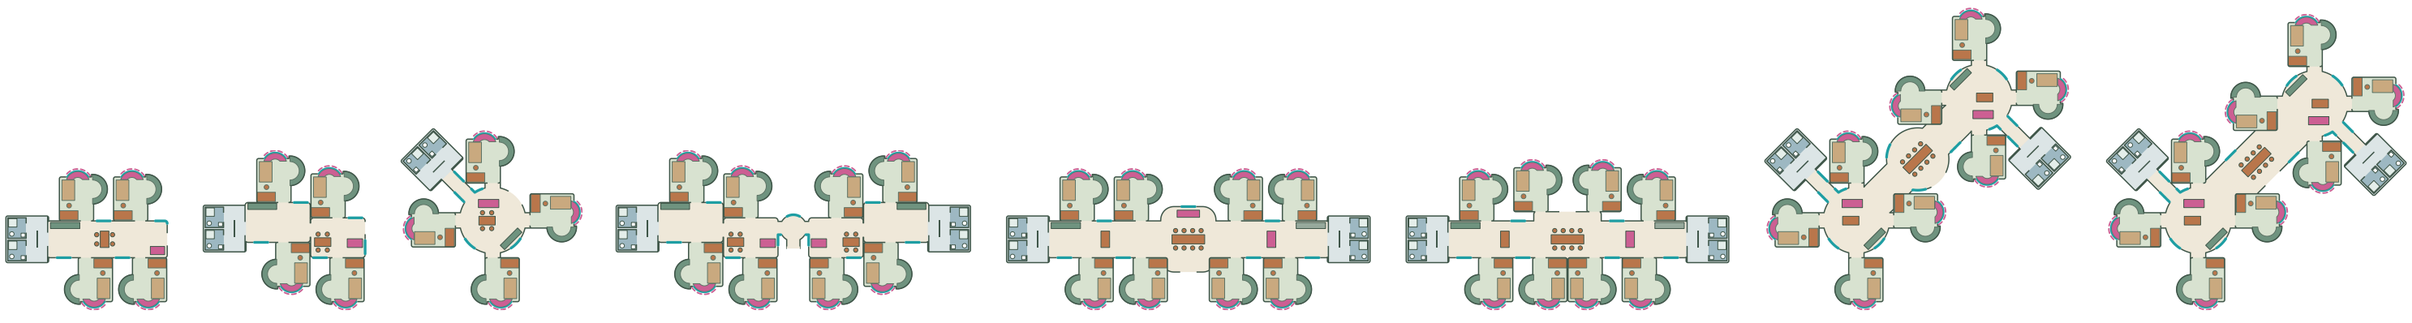

Convivencia continua *Dos ámbitos* *Centro libre* *Pareja con umbral* *Encuentro mayor* *Casa común continua* *Plaza entre estancias* *Continuidad diagonal*

Las ocho organizaciones a la misma escala. E 1:600

Este cuaderno recoge cómo se organiza una casa para cuatro, y para ocho, personas jóvenes que comparten vivienda durante un tiempo en El Rastro. No empieza por una forma. Empieza por lo que pasa dentro: volver empapadas de madrugada, una entrevista por videollamada mientras otra cocina, alguien que necesita dormir porque entra a trabajar a las seis.

De esas escenas salen relaciones: cosas que conviene acercar, cosas que hay que proteger unas de otras y cosas que pueden compartir el mismo sitio por turnos. Las relaciones se ordenan primero en un tejido sin metros y después se miden con cuerpos, muebles y pasos reales.

Una regla ordena todas las plantas: el centro de la casa es para convivir. Los aseos se agrupan en el borde, detrás de un vestíbulo y un filtro, y el suelo que queda en medio se reserva para cocinar, comer, hablar y estar.

Salen tres casas de cuatro —una continua, una en dos ámbitos, una con el centro libre— y cinco maneras de unirlas en grupos de ocho. Cada residente tiene su habitación, con un vestidor que se recorre, un tablero A1 que se recoge contra la pared y una bow pequeña donde sentarse a mirar fuera.

Índice

01 *Dieciséis escenas* 4
Una casa compartida, hora a hora.

02 *Acercar y proteger* 6
Cinco atractores y los cruces entre ellos.

03 *La parcela* 8
651 m² entre medianeras, abiertos a Ribera de Curtidores.

04 *Un tejido de cosas que pasan* 10
Puntos que son acciones, hilos que son secuencias.

05 *Veinte acciones* 13
Acercar, proteger, compartir por turnos.

06 *La habitación* 16
18,35 m² para dormir, vestirse, trabajar y mirar fuera.

07 *Servicios en el borde* 18
Dos aseos, un vestíbulo y un filtro.

08 *Tres casas de cuatro* 19
Continua, en dos ámbitos, con el centro libre.

09 *Casas de ocho* 23
Cinco maneras de juntar dos casas.

10 *Superficies* 28
Lo que cuesta cada manera de convivir.

01

Dieciséis escenas

Una casa compartida, hora a hora.

Antes de dibujar una pared, la casa se pone a prueba con dieciséis escenas inventadas. No son entrevistas ni estadísticas: son situaciones que reconoce cualquiera que haya compartido piso, escritas para que choquen entre sí. Cada una dice qué pasa, qué secuencia de acciones arrastra y qué necesita del espacio. La última línea es la crítica: lo que la casa no debería obligar a hacer a nadie.

S01 *00:40*

Volver empapadas

Dos vuelven de ayudar a recoger materiales. Ropa mojada, zapatos y lona; otra persona duerme.

Llegar · dejar · cambiarse · secar

Necesita · Secado y ducha cerca de llegada; ruido lejos del descanso.

La cooperación no debe dejarte durmiendo entre humedad.

S02 *02:10*

Una amiga sin habitación

Una amiga necesita pasar la noche. Quien la recibe tiene una entrega a las nueve.

Acoger · guardar · dormir · salir

Necesita · Acogida con intimidad y duración acordada; sin ocupar evacuación.

Una casa puede apoyar una emergencia sin normalizarla.

S03 *09:00*

Entrevista y desayuno

Entrevista por videollamada; al lado se prepara desayuno y suena la cafetera.

Conectar · hablar · concentrarse

Necesita · Lugar privado con conexión y control acústico.

Buscar trabajo no debería exigir pagar otro espacio.

S04 *01:20*

Entrega y turno temprano

Una persona corta una maqueta; otra necesita dormir para entrar a trabajar a las seis.

Desplegar · cortar · dejar · dormir

Necesita · Superficie resistente y almacenamiento; separar ruido y descanso.

La flexibilidad no consiste en desmontar tu trabajo cada noche.

S05 *20:30*

Cocinar para muchas

Cuatro cocinan doce raciones. Alguien sólo quiere calentar su táper y marcharse.

Preparar · cocinar · servir · recoger

Necesita · Cocina colectiva y uso individual simultáneo, sin bloquear paso.

Compartir debe ampliar opciones, no imponer una comida común.

S06 *19:10*

Conflicto sin público

Dos residentes necesitan mediación mientras el resto está en la sala.

Llegar · hablar · escuchar · salir

Necesita · Conversación reservada y salida discreta; no aislamiento obligatorio.

Lo común también necesita confidencialidad.

S07 *18:00*

Reparar una tela

Se cose una pieza seca de protección mientras alguien busca herramientas para su bici.

Desmontar · extender · reparar · guardar

Necesita · Mesa de reparación, herramientas y acceso de mantenimiento.

Una fachada de tela necesita trabajo, tiempo y presupuesto.

S08 *22:45*

No quiero participar

Hay cena y conversación. Una residente quiere ducharse y acostarse sin explicar nada.

Entrar · asearse · retirarse

Necesita · Acceso a cuarto y baño sin atravesar la reunión.

La comunidad no puede exigir disponibilidad constante.

S09 *07:15*

Intimidad con prisas

Dos tienen horarios distintos; una necesita vestirse mientras otra sigue dormida.

Buscar ropa · vestirse · salir

Necesita · Luz localizada, armario accesible y circulación sin rodear cama.

La intimidad se mide también en no interrumpir a otra persona.

S10 *16:20*

Acompañar sin interrogar

Una amiga viene desbordada; quiere compañía tranquila, sin ser observada por toda la casa.

Recibir · sentarse · acompañar

Necesita · Rincón protegido próximo al estar, sin exposición ni encierro.

Cuidar no equivale a improvisar una consulta sanitaria.

S11 *23:30*

Lavar después del trabajo

Se acaba la ropa limpia; lavar ahora coincide con quien ya duerme.

Clasificar · lavar · secar · guardar

Necesita · Separación acústica, almacenamiento y horario acordado.

Los horarios domésticos deben admitir trabajos incompatibles.

S12 *15:00*

Calor y videollamada

Una habitación se recalienta; cerrar la tela quita vista y parte de la luz del escritorio.

Sombrear · ventilar · seguir trabajando

Necesita · Control individual de tela y luz; estudiar aire, calor y deslumbramiento.

El confort no puede depender de aguantar o gastar más.

S13 *21:00*

Intimidad afectiva

Una residente recibe a su pareja; otras quieren seguir usando la sala y la cocina.

Recibir · estar · retirarse

Necesita · Privacidad visual y acústica; acuerdos sin vigilancia.

Compartir vivienda no elimina la vida íntima.

S14 *11:30*

Quién recoge hoy

Tras una actividad compartida quedan platos, basura y una tela que revisar. Nadie tiene tiempo.

Limpiar · reparar · repartir tareas

Necesita · Equipos accesibles; responsabilidades y presupuesto explícitos.

La sostenibilidad del grupo no se sostiene con trabajo invisible.

S15 *18:40*

Llegar cargada

Una persona llega con compra y material voluminoso; otra lleva la bici.

Llegar · subir · girar · guardar

Necesita · Recorrido continuo, giros y aparcamiento fuera del paso.

La accesibilidad se comprueba con cuerpos y cargas reales.

S16 *13:00*

Descansar enferma

Una residente necesita reposo mientras hay trabajo compartido y cocina en marcha.

Asearse · beber · descansar · pedir ayuda


Necesita · Descanso con control de luz y acceso próximo a aseo.

El cuidado debe permitir retirarse sin desaparecer del grupo.

02

Acercar y proteger

Cinco atractores y los cruces entre ellos.

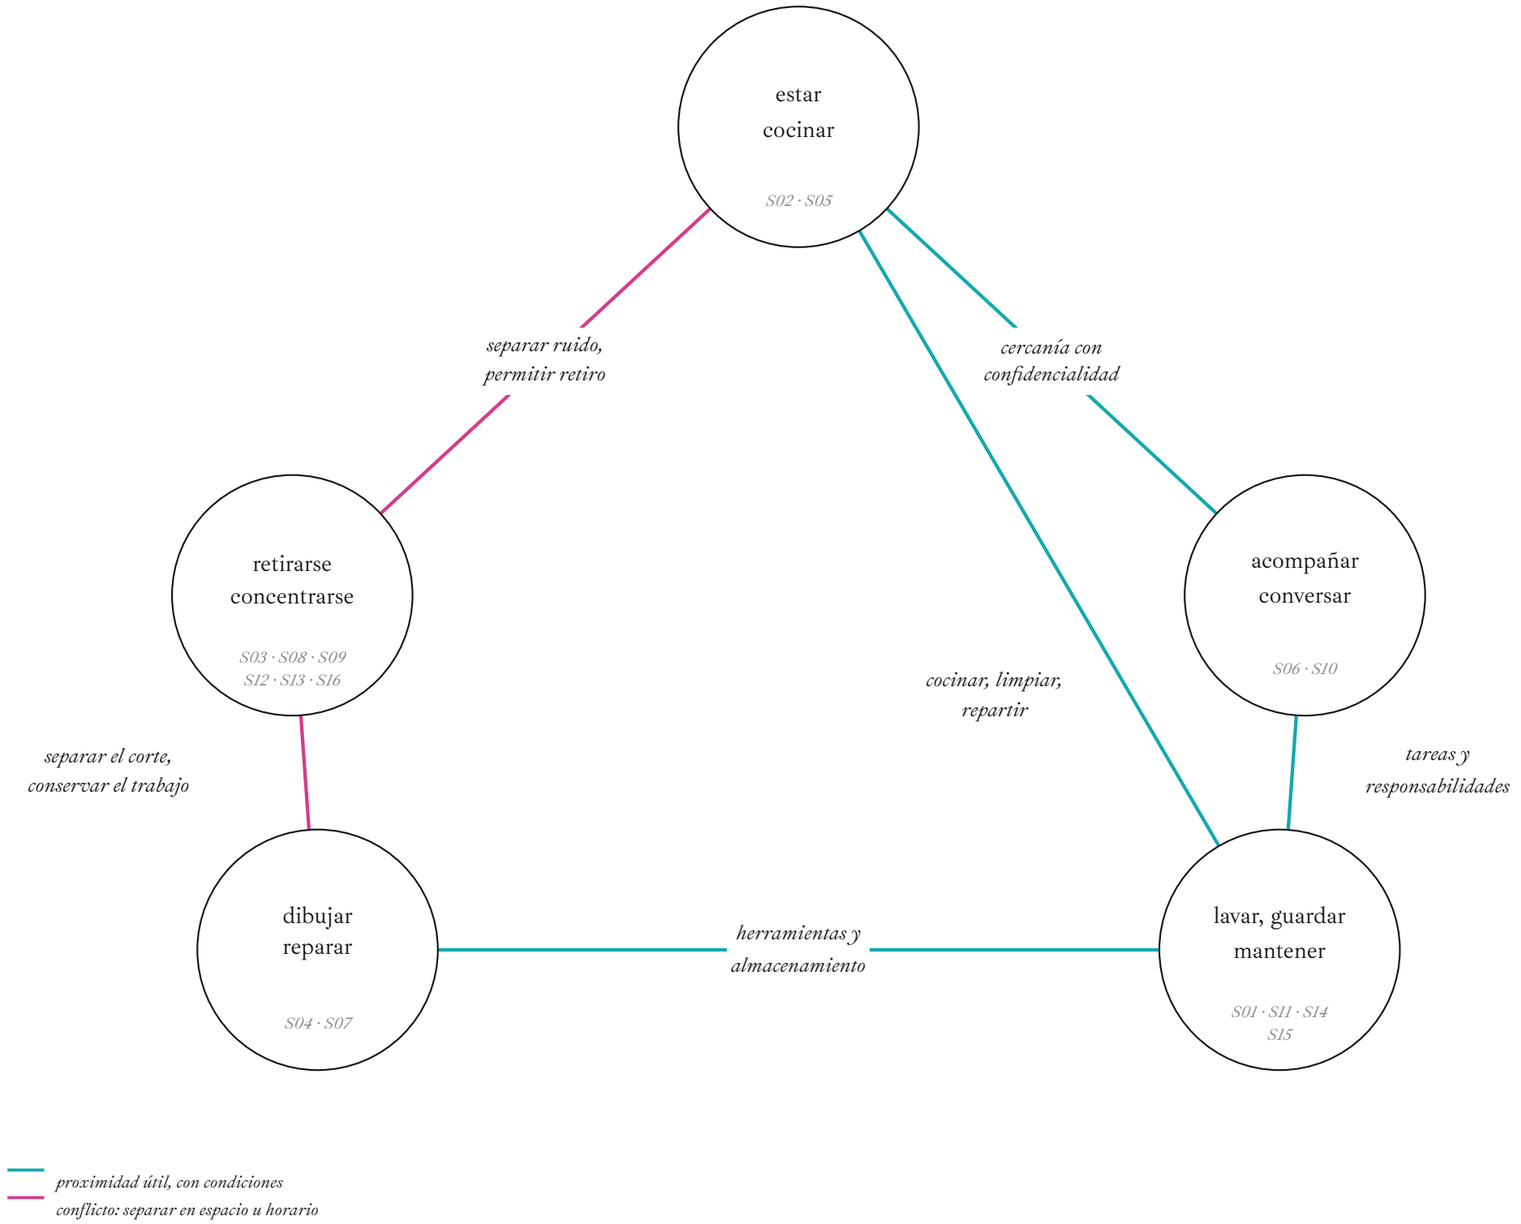

Las escenas se agrupan alrededor de cinco atractores: estar y cocinar; retirarse y concentrarse; acompañar y conversar; dibujar y reparar; lavar, guardar y mantener. Entre ellos hay dos tipos de relación. Las turquesas son proximidades útiles, siempre con condiciones. Las rosas son conflictos que piden separar en el espacio o en el horario. Las distancias del dibujo no son metros: un atractor puede estar en varios sitios y cambiar con la hora.

Cuando dos escenas coinciden, el conflicto se convierte en una exigencia de proyecto.

S01 × S16

Secar y ducharse / dormir enferma

Separar ruido y humedad; ayuda cerca, sin exposición.

S03 × S05

Entrevista / cocinar para varias

Conexión privada y separación acústica, sin prohibir cocinar.

S04 × S08

Entrega nocturna / derecho al retiro

Un trabajo que pueda quedarse montado, fuera del acceso.

S02 × S13

Acoger una noche / intimidad

Un lugar temporal acordado, sin ocupar el dormitorio de otra.

S07 × S15

Reparar / llegar con cargas

Herramientas cerca, material fuera del recorrido.

S10 × S06

Acompañar / mediar un conflicto

El mismo lugar puede servir por turnos si hay confidencialidad.

S11 × S09

Lavar tarde / salir temprano

Capacidad, almacenamiento, separación acústica y horarios.

S12 × S03

Cerrar la tela por calor / trabajar

Controlar clima y luz a la vez; la tela no está siempre abierta.

03


La parcela

651 m² entre medianeras, abiertos a Ribera de Curtidores.



Parcela y edificios vecinos según Catastro; el gris crece con el número de plantas. E 1:400

La parcela catastral 0134911VK4703C da a Ribera de Curtidores por un frente de quince metros y se alarga casi cincuenta hacia el interior de la manzana, entre edificios de alturas muy distintas. Es el suelo real del proyecto: estrecho, profundo y rodeado. Los grises del plano indican el número de plantas de cada edificio vecino; cuanto más oscuro, más alto.

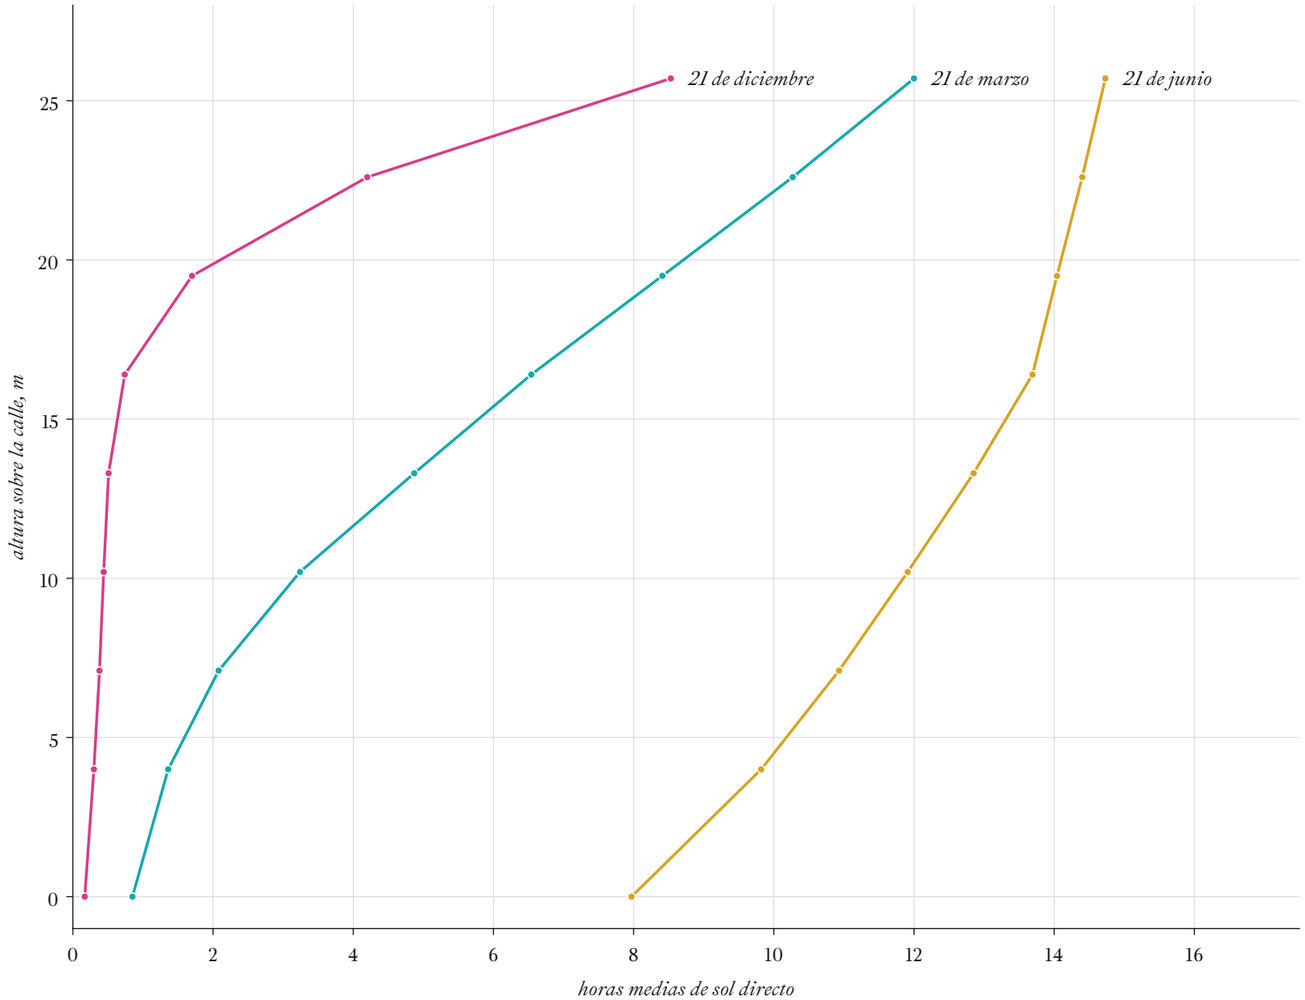

Horas medias de sol directo sobre la parcela a distintas alturas. Modelo 2,5D con las alturas de los edificios vecinos estimadas por su número de plantas.

0,2 – 8,5 h

21 de diciembre, de la calle a 25,7 m

0,9 – 12,0 h

21 de marzo

8,0 – 14,7 h

21 de junio


El sol directo depende de la altura. El 21 de diciembre, a cota de calle, la parcela recibe de media 0,2 horas de sol; a 19,5 m, 1,7 horas; a 25,7 m, 8,5. En marzo pasa de 0,9 a 12 horas, y en junio, de 8 a 14,7.

Por debajo de los dieciséis metros, el invierno es casi de sombra. Las casas necesitan subir para encontrar luz; lo que se queda abajo tiene que ser lo que puede vivir sin sol directo.

04


Un tejido de cosas que pasan

Puntos que son acciones, hilos que son secuencias.

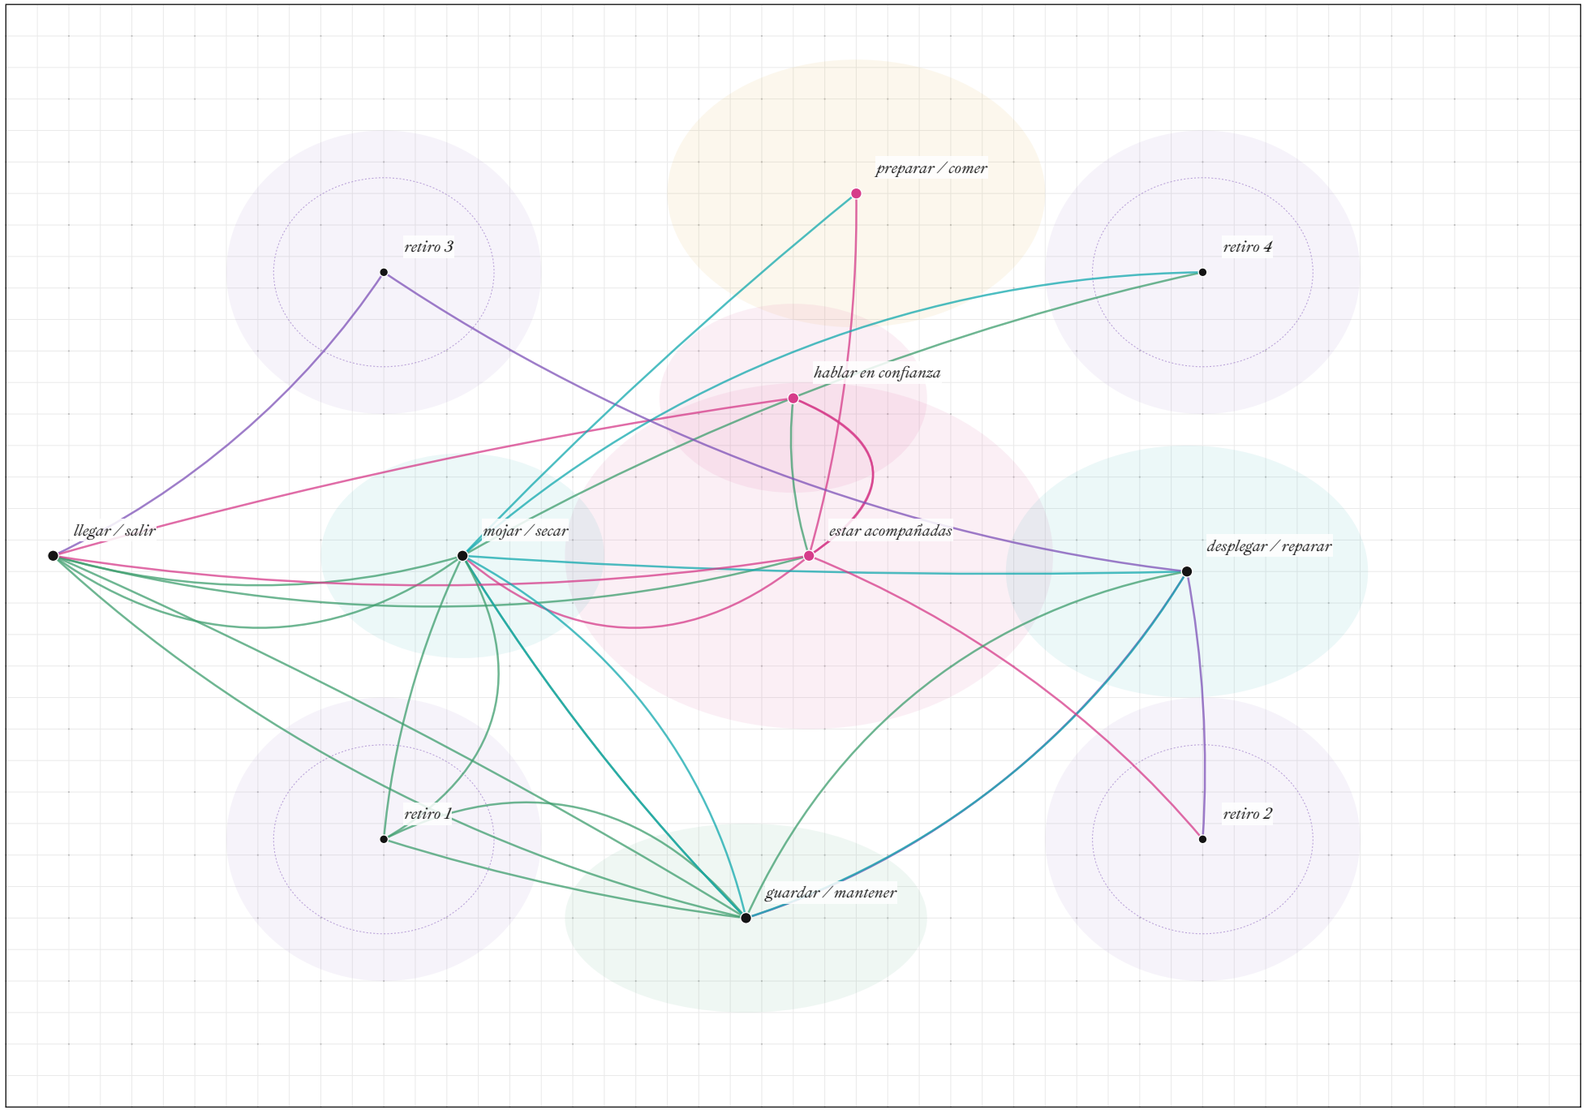

Dieciséis escenas como hilos sobre once puntos. Marco de trabajo sin escala.

Sobre un marco de trabajo sin escala, once puntos recogen lo que se hace en la casa: llegar, mojarse y secarse, estar acompañadas, preparar comida, hablar en confianza, desplegar y reparar, guardar, y cuatro lugares de retiro. Cada escena se dibuja como un hilo que los recorre en orden. Las manchas son ámbitos de uso, no habitaciones. Donde los hilos se amontonan, la casa tiene que decidir.

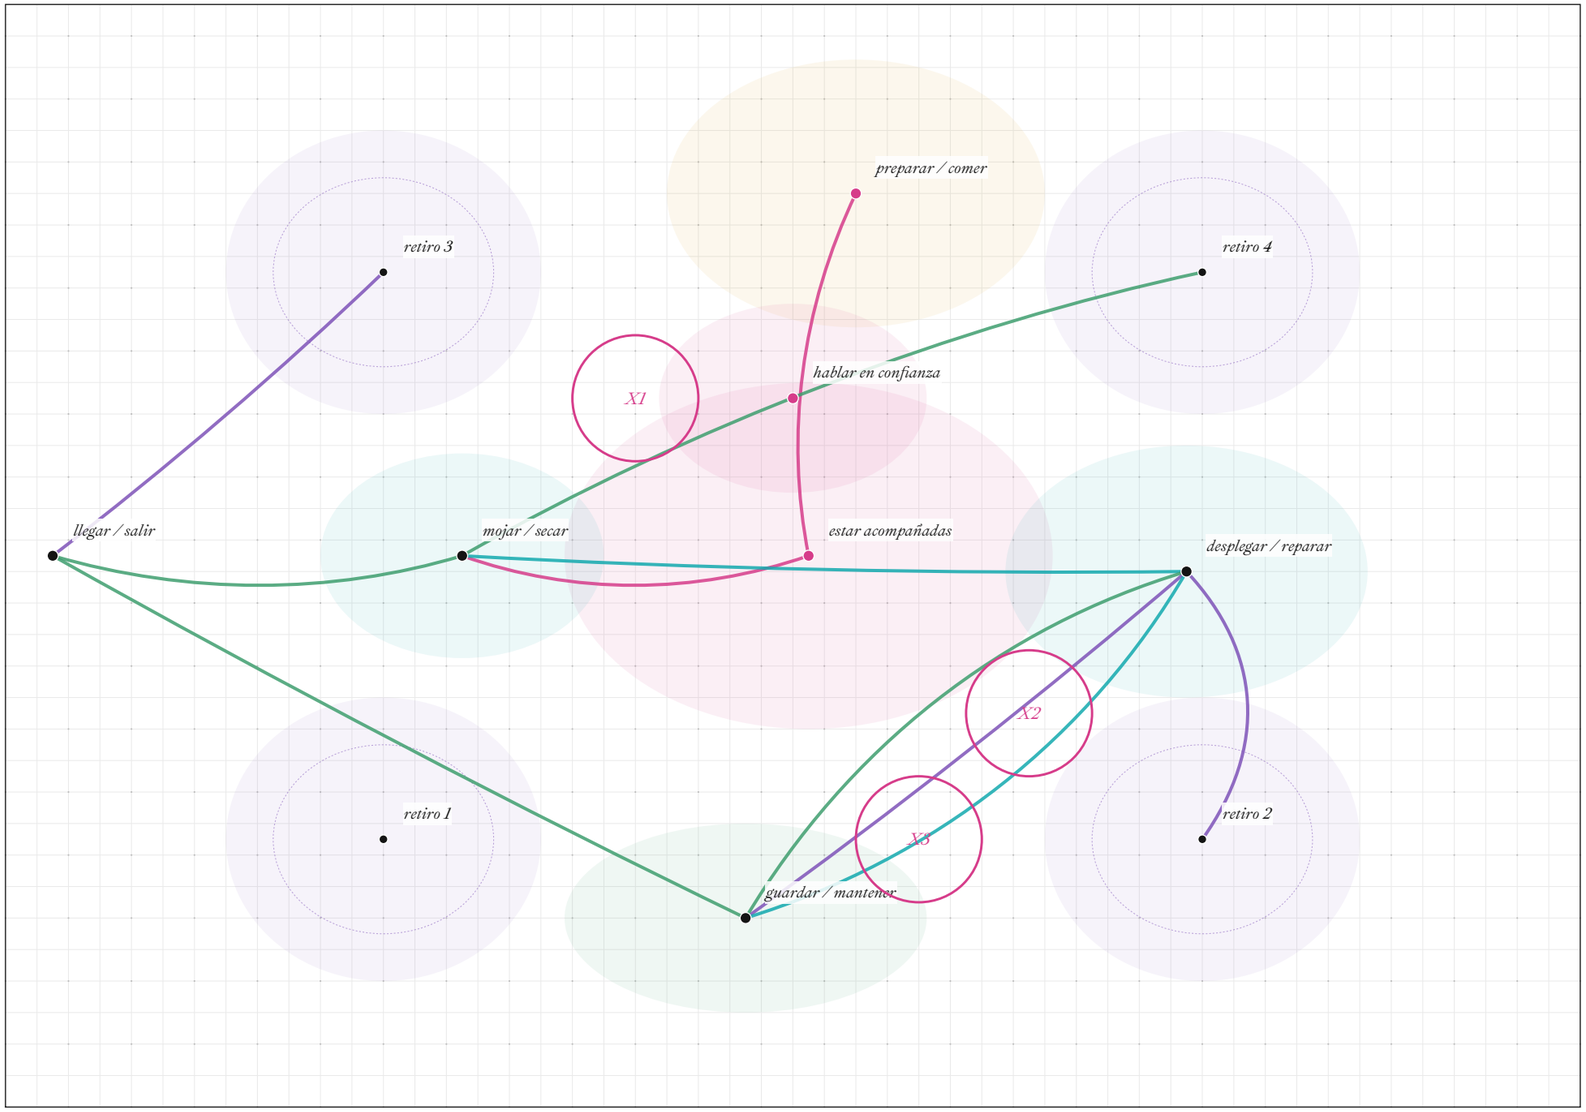

Tres cruces se amplían como problemas espaciales.

X1 S03 × S05

Hablar en privado mientras otras cocinan. Una entrevista no puede depender de que nadie use la cocina.


X2 S04 × S08

Dejar el trabajo montado y poder retirarse. La entrega nocturna necesita un sitio fuera del paso.


X3 S07 × S15

Reparar sin ocupar la llegada. Las herramientas cerca, el material fuera del recorrido.


Acceso, intimidad, sonido, humedad y luz deciden qué cruces se comparten, cuáles se separan y cuáles cambian de hora.

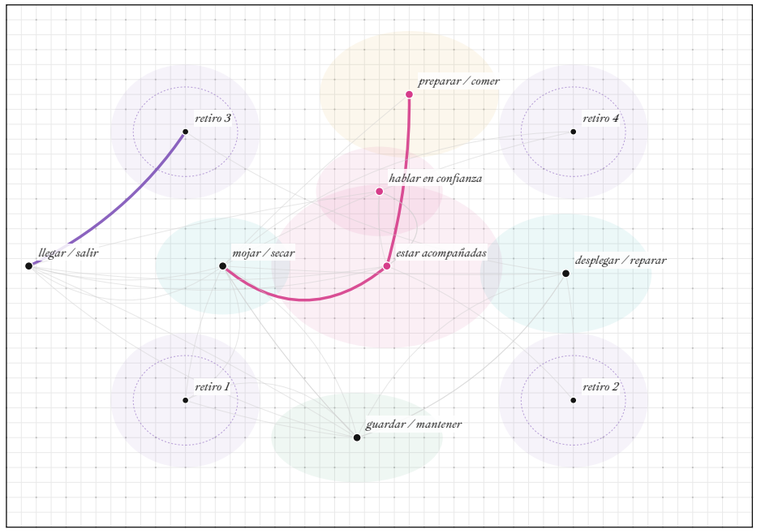


a 09:00 · entrevista y desayuno · S03, S05

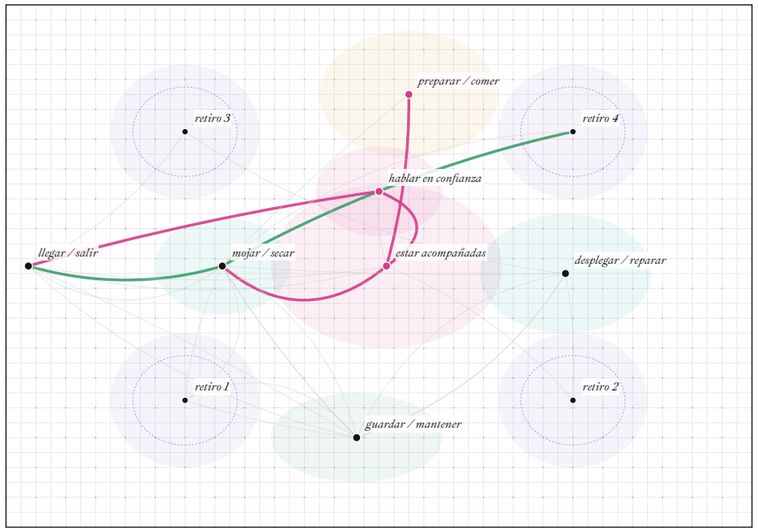

b 20:30 · comer, acompañar y retirarse · S05, S10, S08

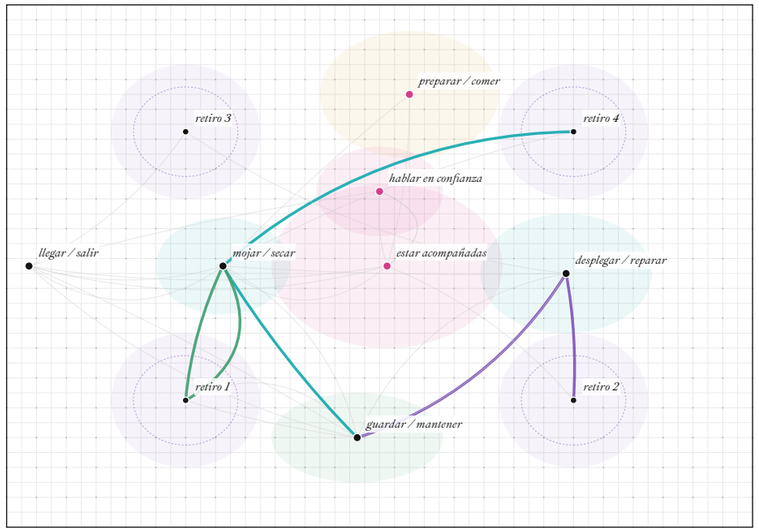

c 01:20 · entrega, lavado y descanso · S04, S11, S16

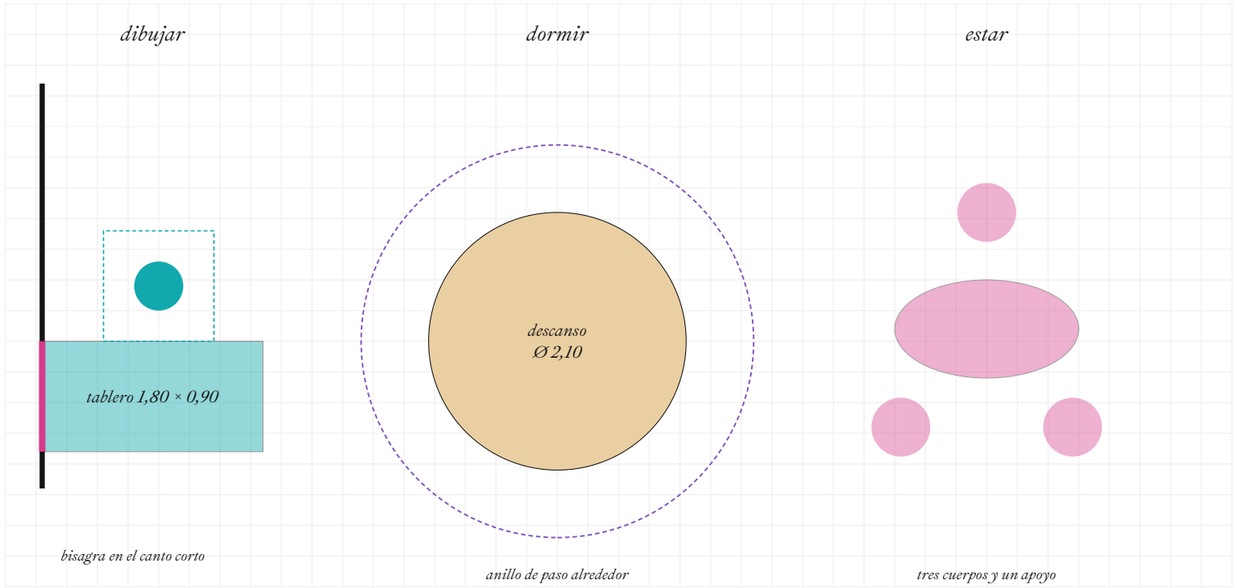

d Dibujar, dormir y estar medidos sobre una retícula de 0,25 m. E 1:50

Medir con el cuerpo


Las mismas posiciones a tres horas del día: la intensidad cambia y nadie ocupa toda la casa a la vez.

Antes de dibujar paredes, el tejido toma tamaño con cuerpos y objetos reales: un tablero A1 que trabaja por su canto corto, un descanso con su anillo de paso y tres cuerpos alrededor de un apoyo.

05

Veinte acciones


Acercar, proteger, compartir por turnos.

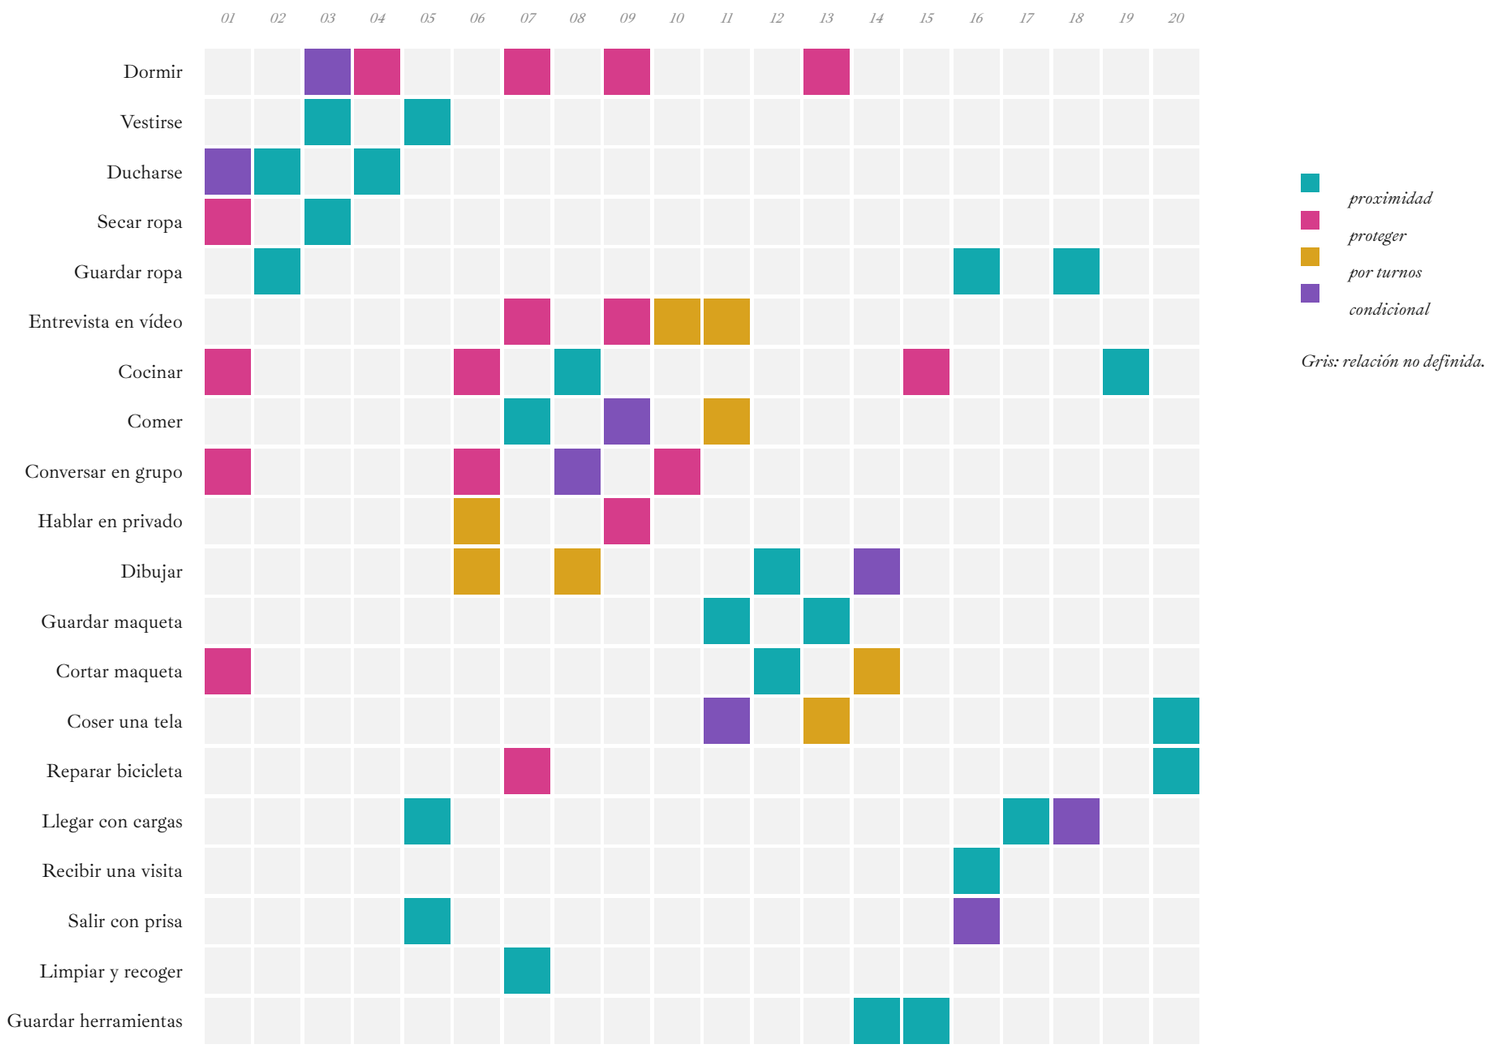


Las acciones se separan de los lugares. Veinte acciones, desde dormir hasta guardar herramientas, y veintiocho relaciones razonadas entre ellas: doce piden proximidad, ocho piden protección, cuatro pueden compartir sitio por turnos y cuatro dependen de condiciones. Lo que queda en gris no está decidido, y por eso no se da por compatible.

Cada relación tiene una razón y una escena de partida.


- *Vestirse × guardar ropa* — *proximidad · S09*
  Alcanzar ropa mientras te vistes.
- *Ducharse × vestirse* — *proximidad · S01/S09*
  Cambiarse con intimidad y transición seca.
- *Ducharse × secar ropa* — *proximidad · S01*
  Gestionar textiles húmedos sin recorrer espacios secos.
- *Cocinar × comer* — *proximidad · S05*
  Trasladar comida sin rodeos.
- *Dibujar × guardar maqueta* — *proximidad · S04*
  Guardar trabajo frágil sin desmontarlo o transportarlo lejos.
- *Cortar maqueta × guardar maqueta* — *proximidad · S04*
  Dejar piezas y materiales a mano.
- *Coser una tela × guardar herramientas* — *proximidad · S07*
  Tomar y devolver herramientas.
- *Reparar bicicleta × guardar herramientas* — *proximidad · S15*
  Tomar y devolver herramientas.
- *Llegar con cargas × guardar ropa* — *proximidad · S01*
  Dejar pertenencias; capacidad y tipo de almacenamiento a revisar.
- *Llegar con cargas × recibir una visita* — *proximidad · S10*
  Resolver la llegada de una visita.
- *Salir con prisa × guardar ropa* — *proximidad · S09*
  Recoger pertenencias al salir; no implica misma puerta que recibir.
- *Cocinar × limpiar y recoger* — *proximidad · S14*
  Recoger después de preparar comida.
- *Dormir × cocinar* — *proteger · S05/S08*
  Cocinar de madrugada puede interrumpir descanso.
- *Dormir × cortar maqueta* — *proteger · S04*
  Corte nocturno y descanso son simultáneos.
- *Dormir × conversar en grupo* — *proteger · S08*
  Las voces del grupo pueden impedir retirarse.
- *Entrevista en vídeo × cocinar* — *proteger · S03/S05*
  La entrevista necesita voz inteligible y privacidad.
- *Entrevista en vídeo × conversar en grupo* — *proteger · S03*
  No exponer una entrevista a conversación ajena.
- *Hablar en privado × conversar en grupo* — *proteger · S06*
  Confidencialidad frente a presencia del grupo.
- *Secar ropa × dormir* — *proteger · S01/S16*
  La humedad no debe resolverse invadiendo el descanso.
- *Reparar bicicleta × cocinar* — *proteger · S15/S05*
  Separar grasa, residuos y herramientas de preparación de comida.
- *Entrevista en vídeo × dibujar* — *por turnos · S03/S04*
  Mesa potencialmente compartible por horario si equipo y postura funcionan.
- *Coser una tela × cortar maqueta* — *por turnos · S07/S04*
  Apoyo de trabajo compartible tras limpieza y almacenamiento.
- *Comer × dibujar* — *por turnos · S05/S04*
  Sólo si no obliga a desmontar continuamente el trabajo.
- *Hablar en privado × entrevista en vídeo* — *por turnos · S06/S03*
  Lugar reservado potencialmente compartible por turnos.
- *Dormir × ducharse* — *condicional · S16*
  Recorrido útil, pero proximidad puede introducir ruido.
- *Comer × conversar en grupo* — *condicional · S05*
  Comer y conversar pueden coincidir, sin obligar a hacerlo.
- *Llegar con cargas × salir con prisa* — *condicional · S15*
  Una misma puerta puede servir; las acciones son distintas.
- *Dibujar × coser una tela* — *condicional · S04/S07*
  Compartir superficie depende de tamaño, suciedad y persistencia.

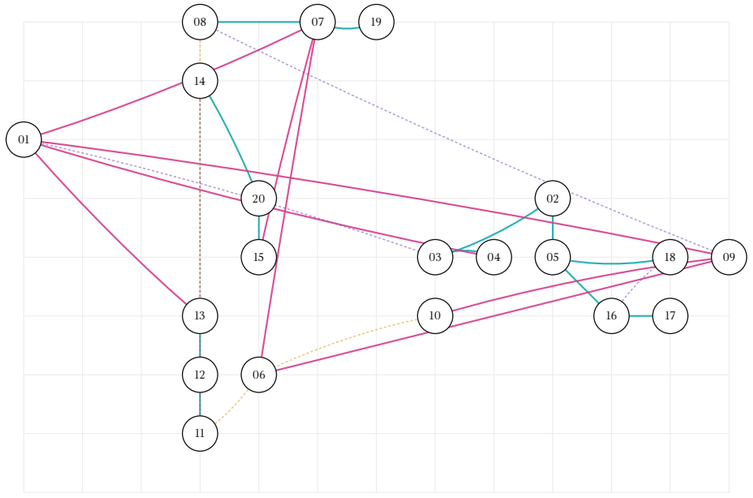

a *Tejido 1*

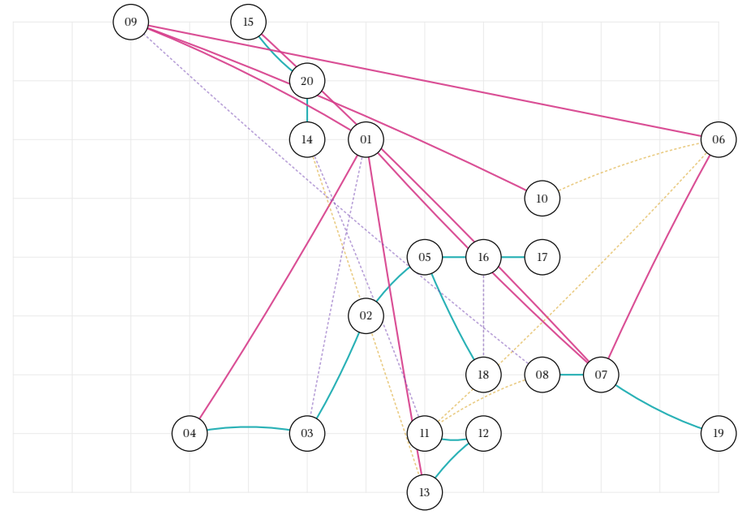

b *Tejido 2*

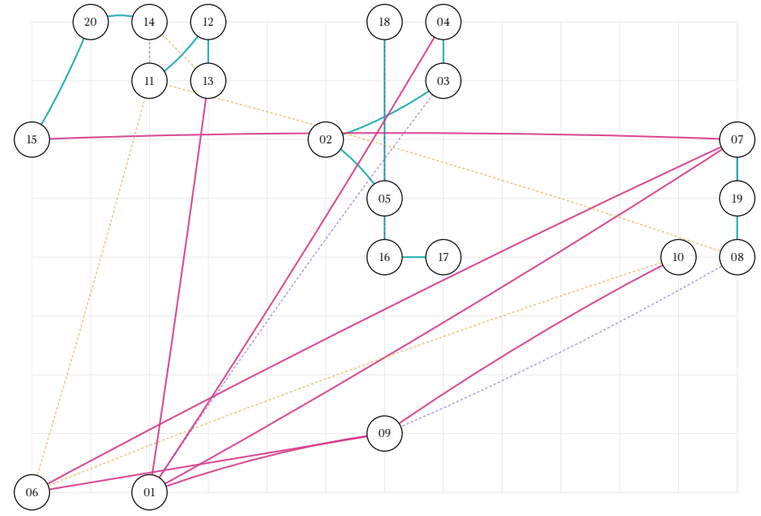

c *Tejido 3*

Tres maneras de ordenar las mismas relaciones

Las veinte acciones se mueven libres sobre una retícula de 13 × 9 posiciones con dos reglas: lo que pide proximidad, a tres pasos como mucho; lo que pide protección, a cinco como poco.

De dieciocho búsquedas se eligen tres colocaciones que cumplen las dos reglas sin excepción y que se parecen lo menos posible entre sí. Ninguna es una planta: son el paso entre las relaciones y la casa.


proximidad
proteger
por turnos condicional

01 *Dormir*
02 *Vestirse*
03 *Ducharse*
04 *Secar ropa*
05 *Guardar ropa*
06 *Entrevista en vídeo*
07 *Cocinar*
08 *Comer*
09 *Conversar en grupo*
10 *Hablar en privado*
11 *Dibujar*
12 *Guardar maqueta*
13 *Cortar maqueta*
14 *Coser una tela*
15 *Reparar bicicleta*
16 *Llegar con cargas*
17 *Recibir una visita*
18 *Salir con prisa*
19 *Limpiar y recoger*
20 *Guardar herramientas*


06

La habitación

18,35 m² para dormir, vestirse, trabajar y mirar fuera.

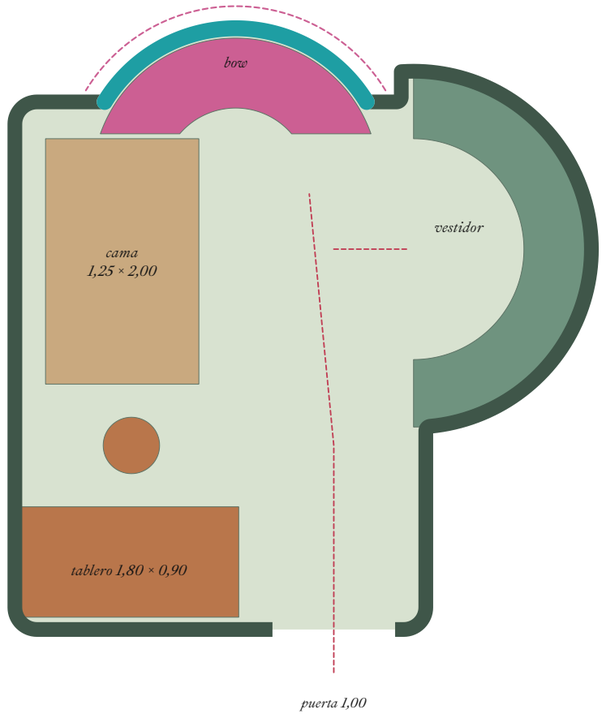


a *Tablero abierto. E 1:50*

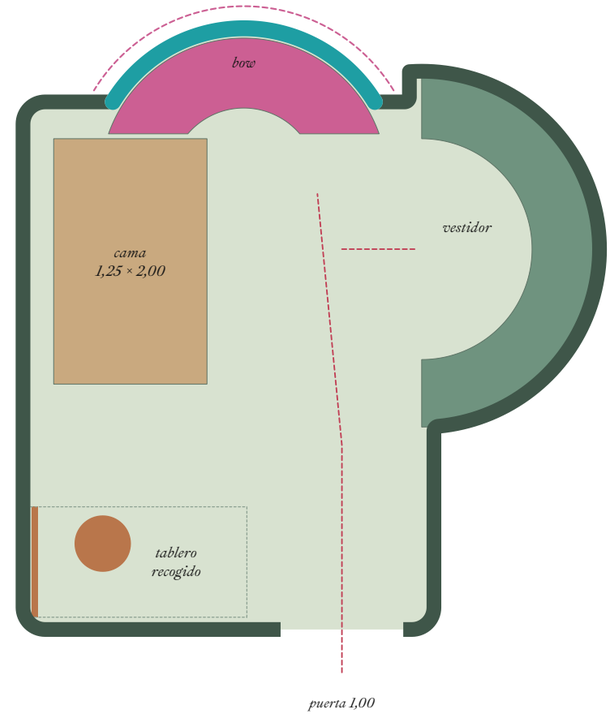


b *Tablero recogido. E 1:50*

Cada residente tiene su habitación. La cama de 1,25 × 2,00 m queda a un lado y deja libre el eje de la puerta. El tablero de 1,80 × 0,90 m gira sobre su canto corto: abierto es una mesa para trabajar un A1; recogido, deja el suelo libre. El vestidor es una media luna que se recorre por dentro, y al fondo la bow abre la habitación hacia fuera con un asiento que sigue la curva del vidrio.

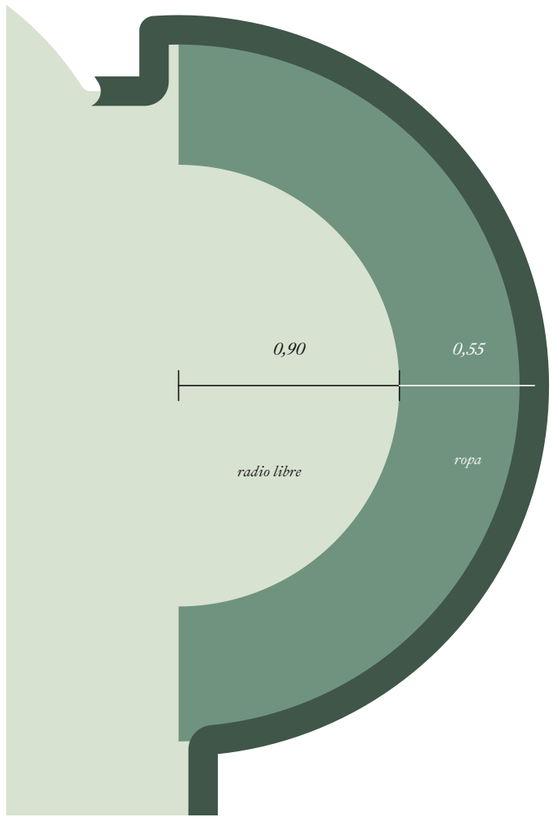


a *Vestidor: 0,55 m de ropa alrededor de un hueco libre de 0,90 m de radio. E 1:25*

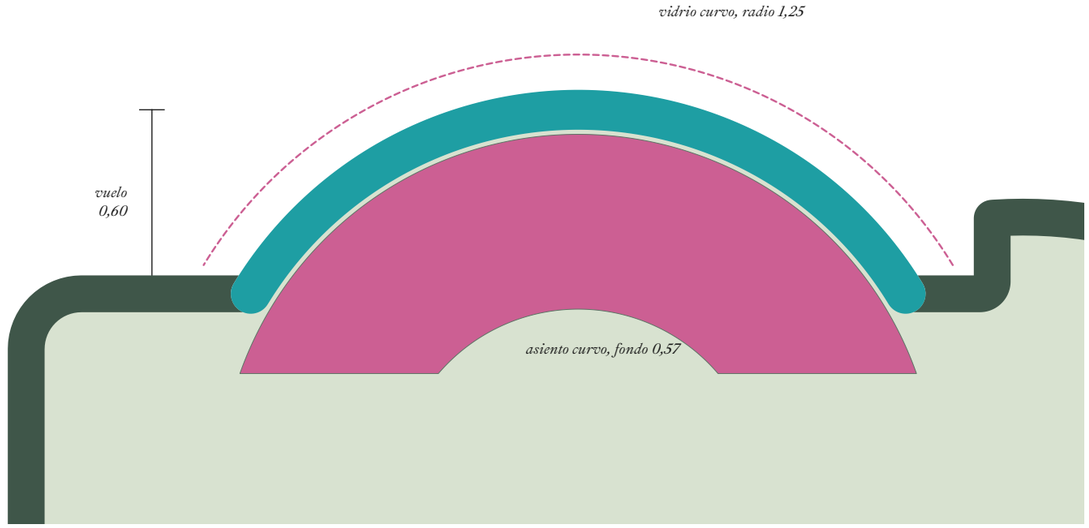

b *Bow: vidrio curvo de 1,25 m de radio que vuela 0,60 m de la fachada, y un asiento curvo de 0,57 m de fondo. E 1:20*

La bow es pequeña a propósito: un sitio para una persona, con la espalda en la habitación y la cara en la calle.

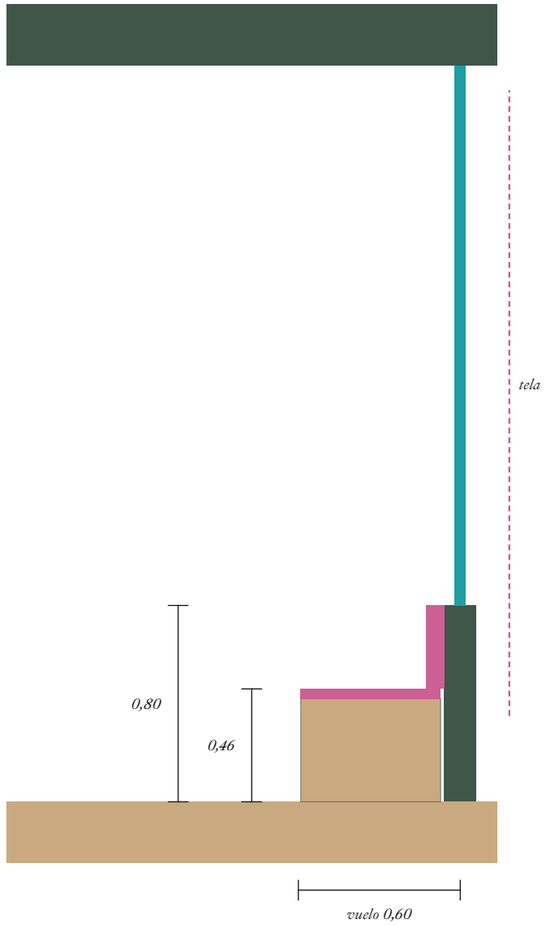


c *Sección por la bow: asiento a 0,46 m, antepecho a 0,80 m y la tela por delante del vidrio. E 1:25*

07

Servicios en el borde

Dos aseos, un vestíbulo y un filtro.

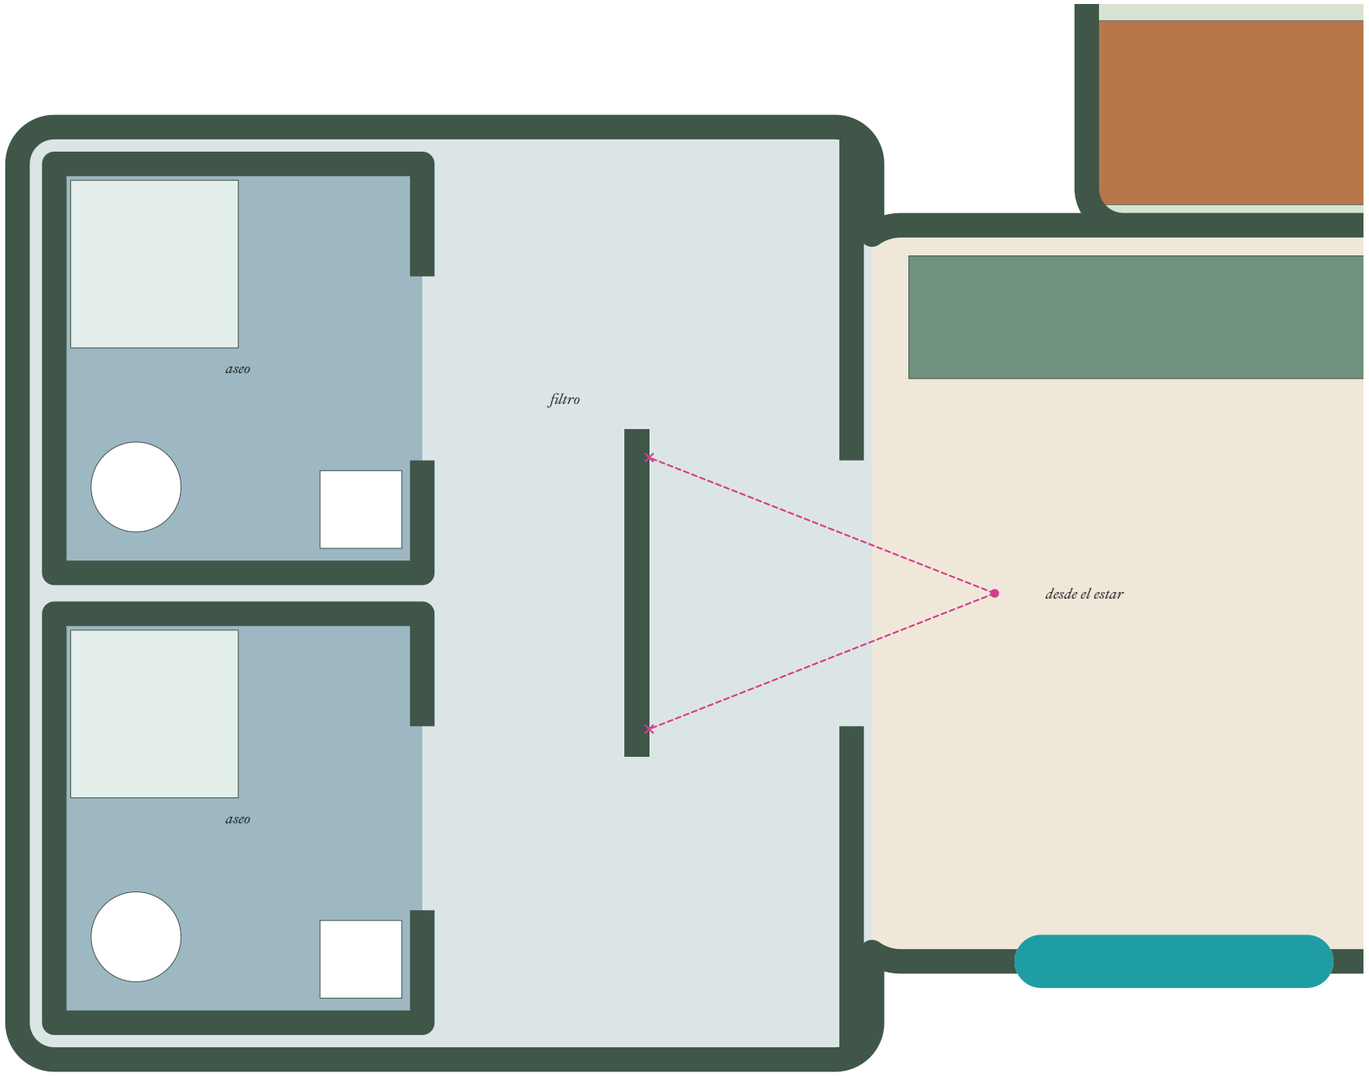


Las visuales desde el estar hacia las puertas de los aseos se detienen en el filtro. E 1:30

Ningún aseo ocupa el centro de la casa. Los dos aseos de cada casa de cuatro se agrupan en una pieza de servicio pegada al perímetro, con su propia fachada. Se entra por un paso de 1,30 m a un vestíbulo; un tabique exento corta la visual desde el estar hacia las puertas, y el paso lo rodea con holgura para un giro de 90 cm. El centro queda para cocinar, comer y estar, y quien quiere ducharse y acostarse no tiene que cruzar la reunión.


08

Tres casas de cuatro


Continua, en dos ámbitos, con el centro libre.

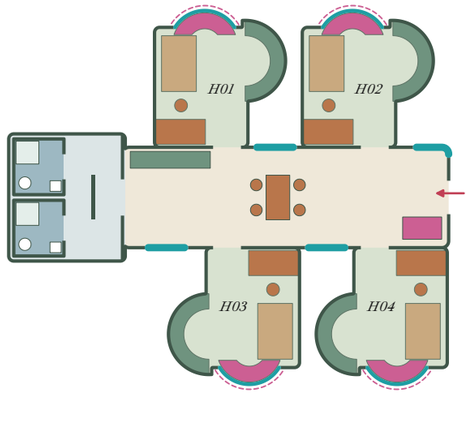

a *V01 · Convivencia continua*

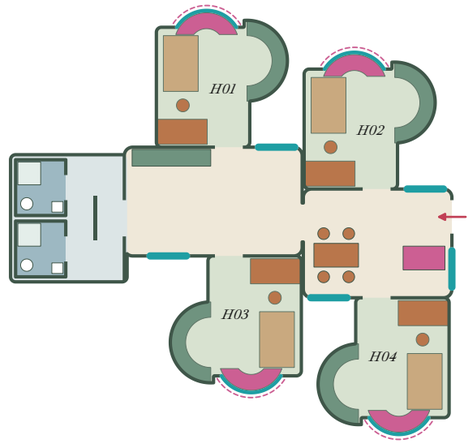

b *V02 · Dos ámbitos*

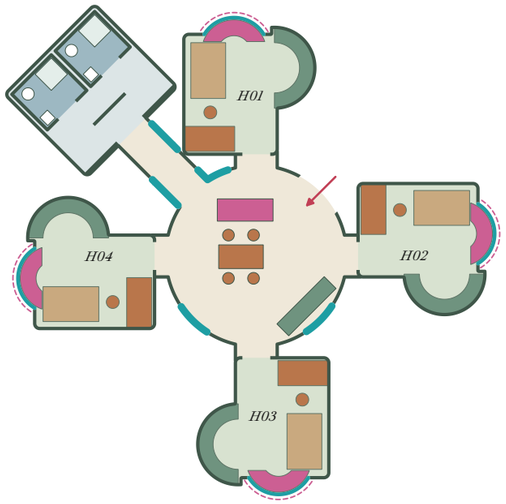

c *V03 · Centro libre*

Misma habitación, misma pieza de servicios, misma escala. E 1:220

dormitorio
tablero y mesas
bow con asiento, estar
suelo común

cama
vestidor y cocina
vidrio
aseos

Con la misma habitación y la misma pieza de servicios salen tres maneras distintas de convivir. En la primera, cocinar, comer y estar se enlazan en un solo espacio. En la segunda, la casa se divide en dos ámbitos conectados. En la tercera, el estar ocupa un círculo libre y las habitaciones lo rodean. Ninguna es un giro de otra.


Convivencia continua

V01 · cuatro residentes


Una sola sala alargada reúne cocina, mesa y estar. Las cuatro habitaciones se abren a ella por parejas, enfrentadas, y las bow miran hacia fuera.

Preparar y comer quedan juntos sin pasar por ningún dormitorio; el estar se va al otro extremo, junto a la entrada. Los aseos ocupan el extremo opuesto, detrás de su vestíbulo, y la mesa se coloca de través para dejar paso alrededor de sus cuatro sillas.


134,17 m² de suelo · 144,28 m² de envolvente

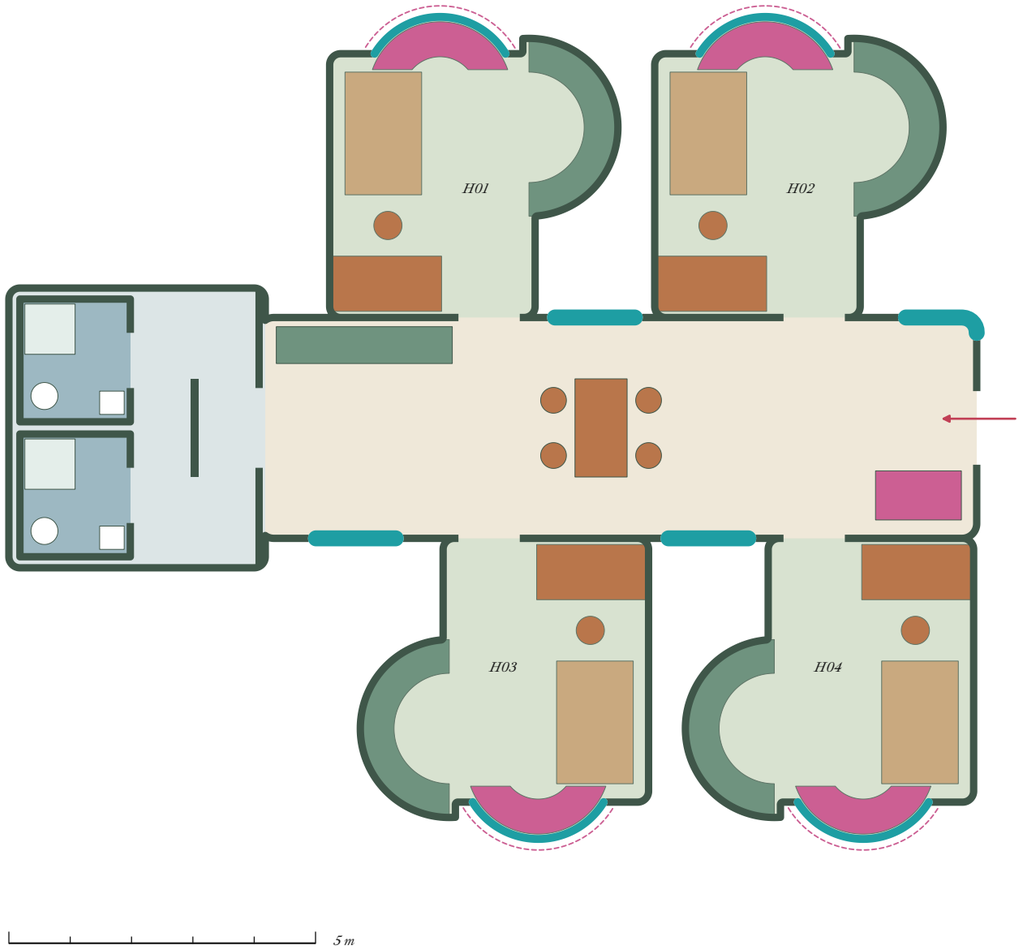

Planta. E 1:100

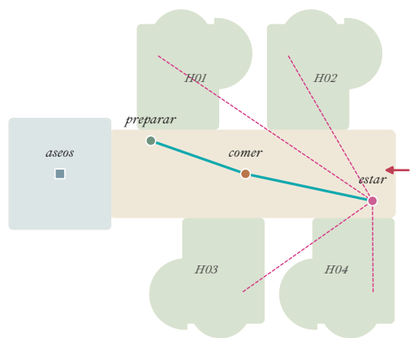

Lectura de la planta. Turquesa: preparar, comer y estar, cerca. Rosa: lo que el estar no debe invadir. E 1:250

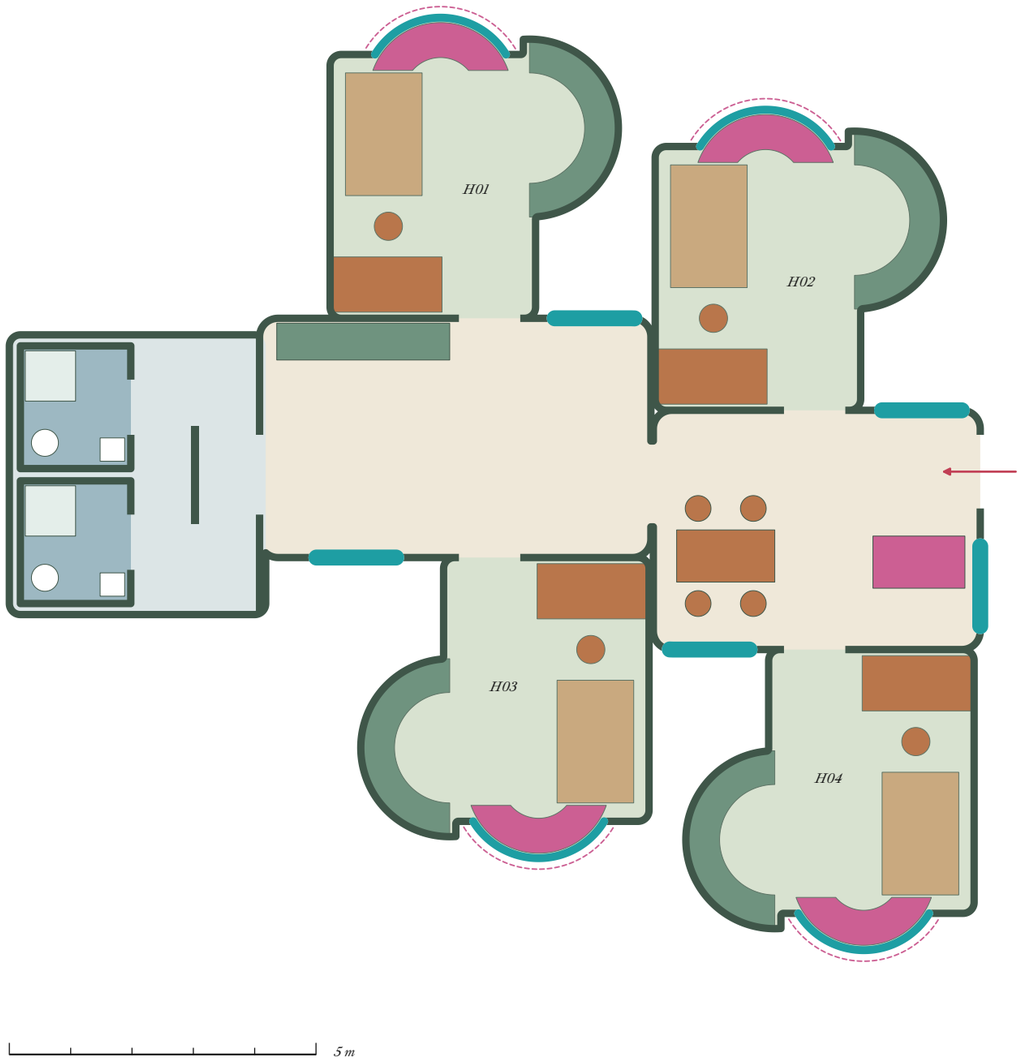

Planta. E 1:100


Dos ámbitos

V02 · cuatro residentes

La casa se parte en dos ámbitos desplazados, unidos por un paso. En uno se prepara la comida; en el otro se come y se está. Nadie está obligado a participar de lo que pasa al otro lado.

Los aseos salen de los dos focos y se concentran en el borde, con un filtro que no se confunde con el paso entre ámbitos.

137,67 m² de suelo · 147,80 m² de envolvente

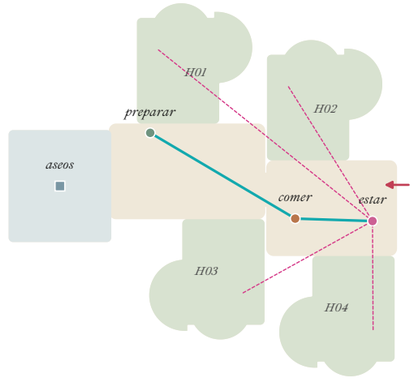

Lectura de la planta. Turquesa: preparar, comer y estar, cerca. Rosa: lo que el estar no debe invadir. E 1:250


Centro libre

V03 · cuatro residentes


El estar recupera el centro: un círculo de 3,25 m de radio con la mesa, el sofá y la cocina, sin ningún servicio dentro. Las cuatro habitaciones se colocan en cruz alrededor y se enlazan con él mediante pequeños ensanchamientos rectos.

Los aseos se llevan a una pieza de servicio en el borde, unida al círculo por un brazo en diagonal que deja las bow siempre hacia fuera. Es la más generosa en el centro y la que más recorrido pide.

132,53 m² de suelo · 144,83 m² de envolvente

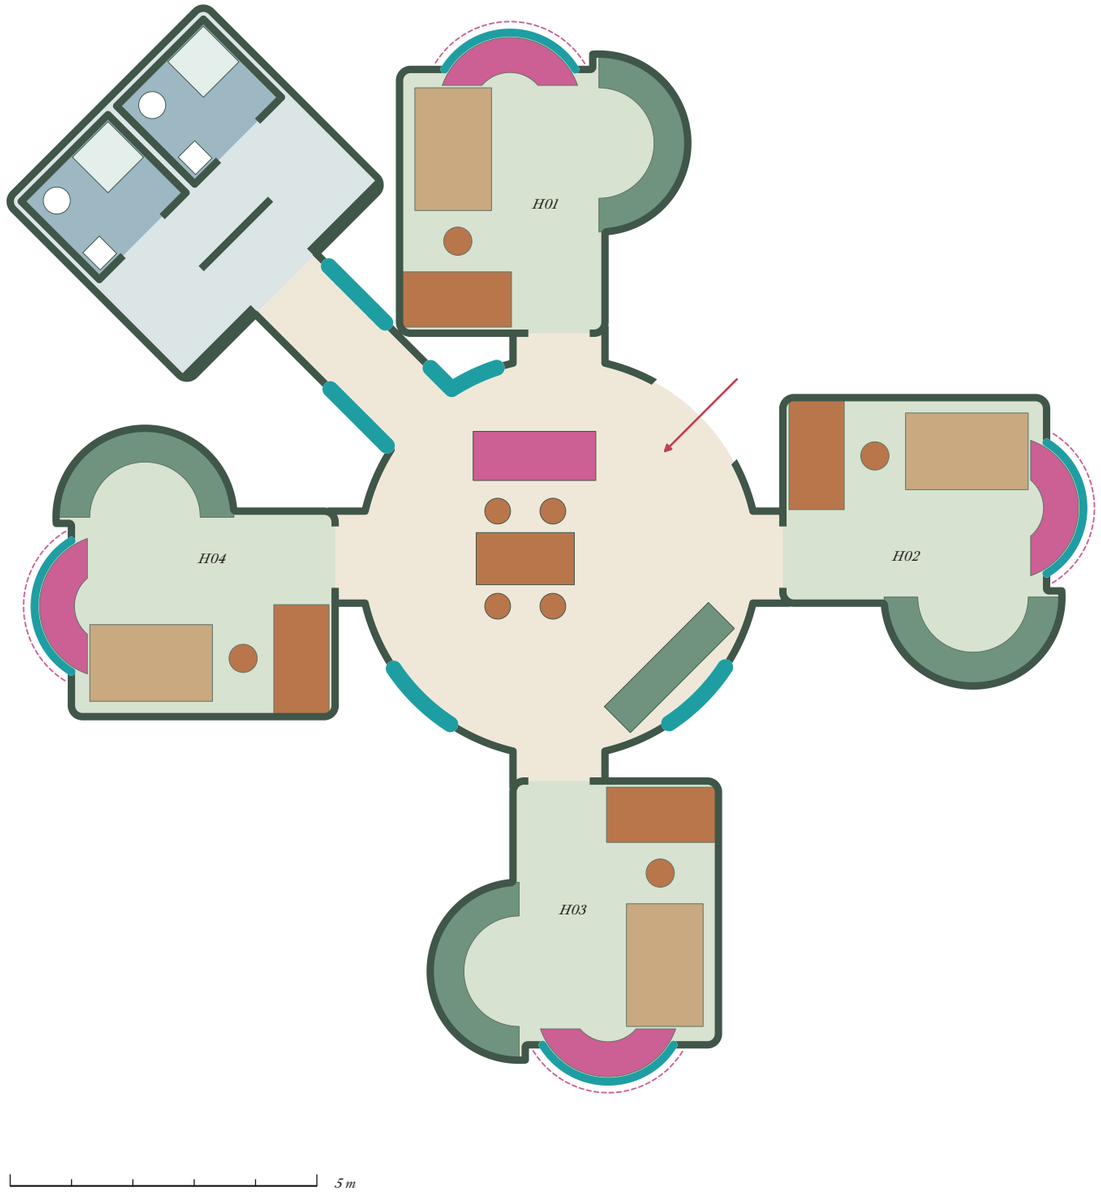

Planta. E 1:100

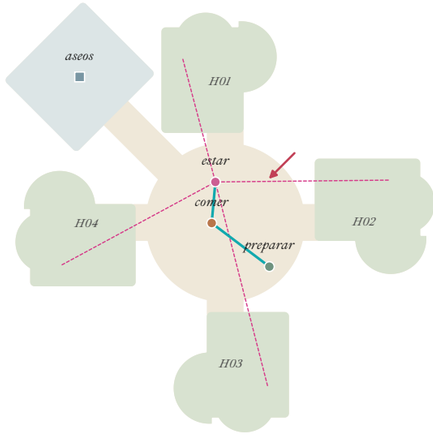


Lectura de la planta. Turquesa: preparar, comer y estar, cerca. Rosa: lo que el estar no debe invadir. E 1:250

09

Casas de ocho

Cinco maneras de juntar dos casas.

Dos casas de cuatro pueden juntarse de muchas maneras, y cada una dice algo distinto sobre cómo se vive en grupo. La pareja con umbral conserva dos cocinas y dos mesas y comparte solo un lugar de encuentro. Las uniones de la V01 convierten el encuentro en la casa: una sala mayor o un suelo continuo para ocho. Las de la V03 ensayan una plaza entre dos círculos o una estancia en diagonal. En todas, cada persona llega a su habitación sin atravesar la de nadie y los aseos siguen en el borde.

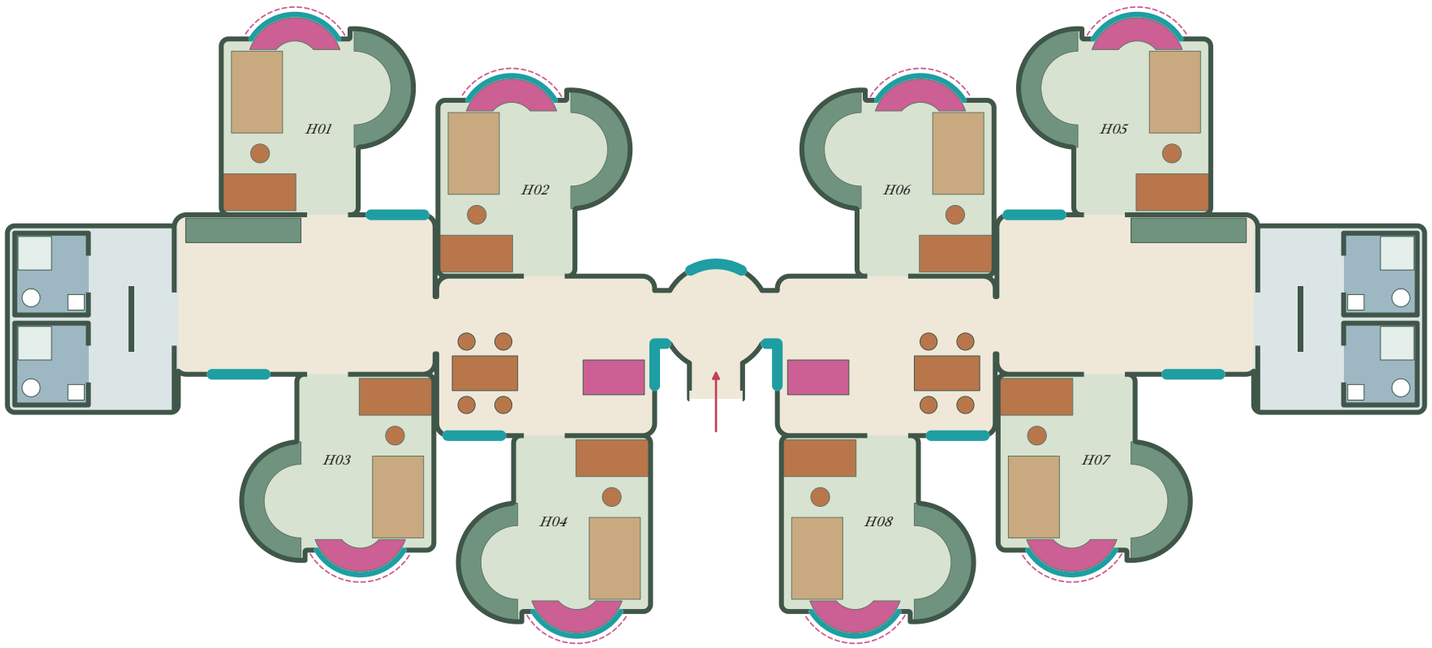

Planta. E 1:150


Pareja con umbral

V02 · ocho residentes

Dos casas conservan sus espacios compartidos —dos cocinas, dos comedores de cuatro— y se encuentran en un umbral común, un pequeño círculo con su propia entrada.

Es la unión con más autonomía entre grupos. El encuentro no lleva ningún servicio en su centro: los aseos quedan en los extremos exteriores.

282,30 m² de suelo · 303,21 m² de envolvente

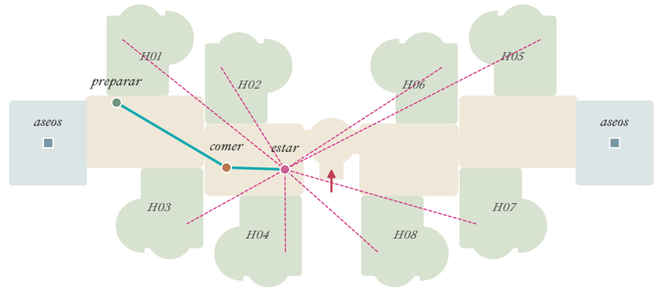

Lectura de la planta. Turquesa: preparar, comer y estar, cerca. Rosa: lo que el estar no debe invadir. E 1:330


Encuentro mayor

V01 · ocho residentes


El encuentro se convierte en una sala para ocho. Recibir, comer y reunirse ocurren desde una llegada común, con una mesa grande para todas.

Hay una cocina principal, una despensa, una mesa de trabajo y un estar. Los cuatro aseos se reparten entre los dos bordes filtrados y los ocho dormitorios siguen siendo individuales.

295,31 m² de suelo · 315,48 m² de envolvente

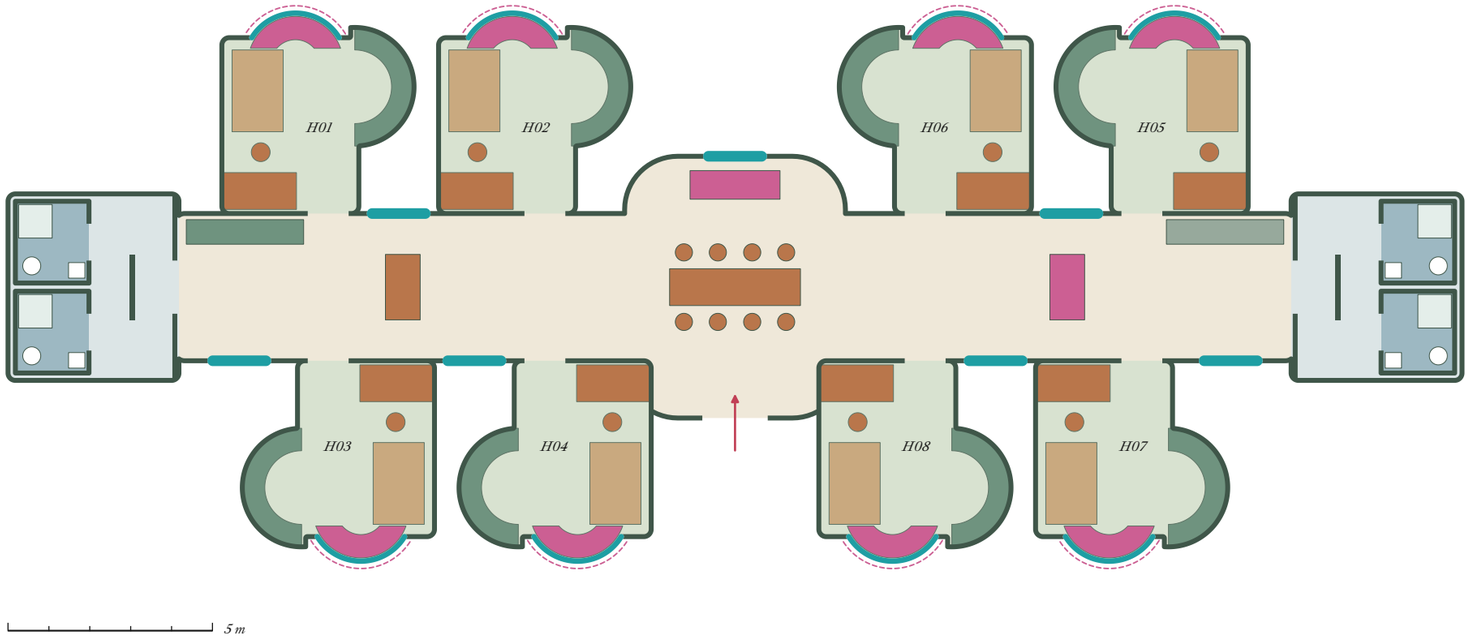

Planta. E 1:150

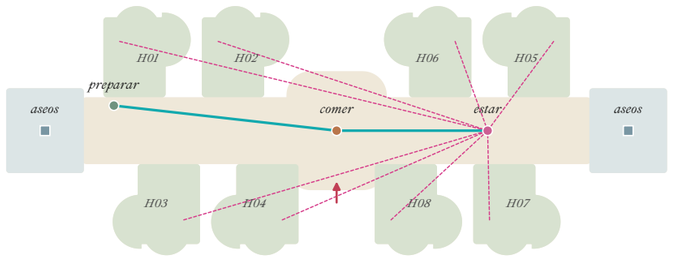

Lectura de la planta. Turquesa: preparar, comer y estar, cerca. Rosa: lo que el estar no debe invadir. E 1:330


Casa común continua

V01 · ocho residentes


Un suelo común continuo enlaza cocina, trabajo, comida y estar sin ninguna puerta entre las dos casas de origen. La mesa admite a las ocho.

Dos dormitorios se desplazan 0,90 m para liberar la llegada y el paso alrededor de la mesa, sin reducir cuerpos ni muebles. Los servicios quedan en los dos extremos.

274,39 m² de suelo · 294,20 m² de envolvente

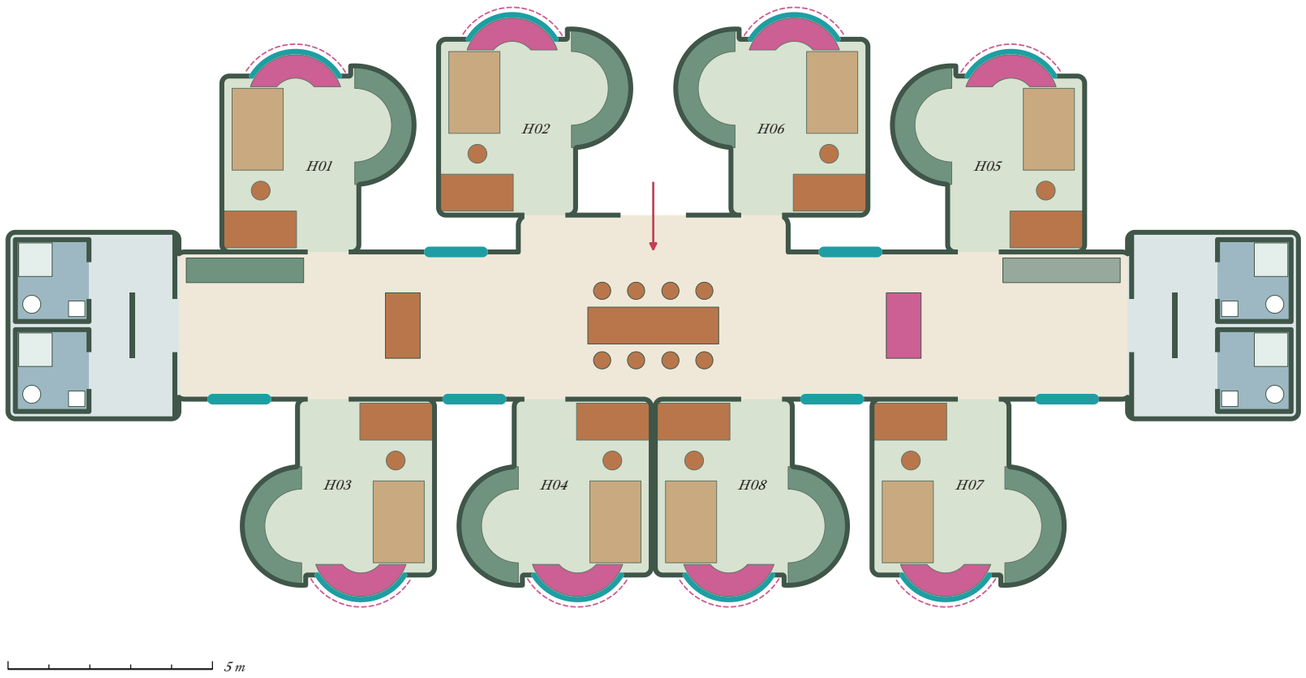

Planta. E 1:150

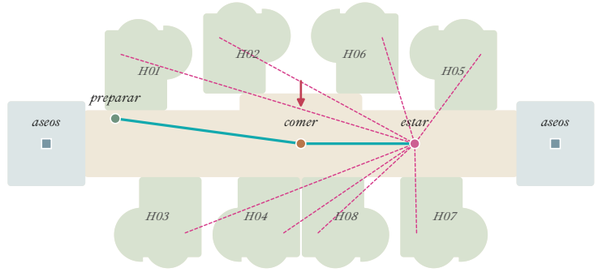

Lectura de la planta. Turquesa: preparar, comer y estar, cerca. Rosa: lo que el estar no debe invadir. E 1:330


Plaza entre estancias

V03 · ocho residentes


Una plaza circular de 3,05 m de radio pone en relación los dos círculos libres. Las dos cocinas pertenecen al grupo de ocho y la mesa común se coloca en diagonal en mitad de la plaza.

Los servicios se apartan al borde exterior de cada extremo. Es la unión de mayor intensidad formal y también la de mayor superficie.

310,37 m² de suelo · 335,46 m² de envolvente

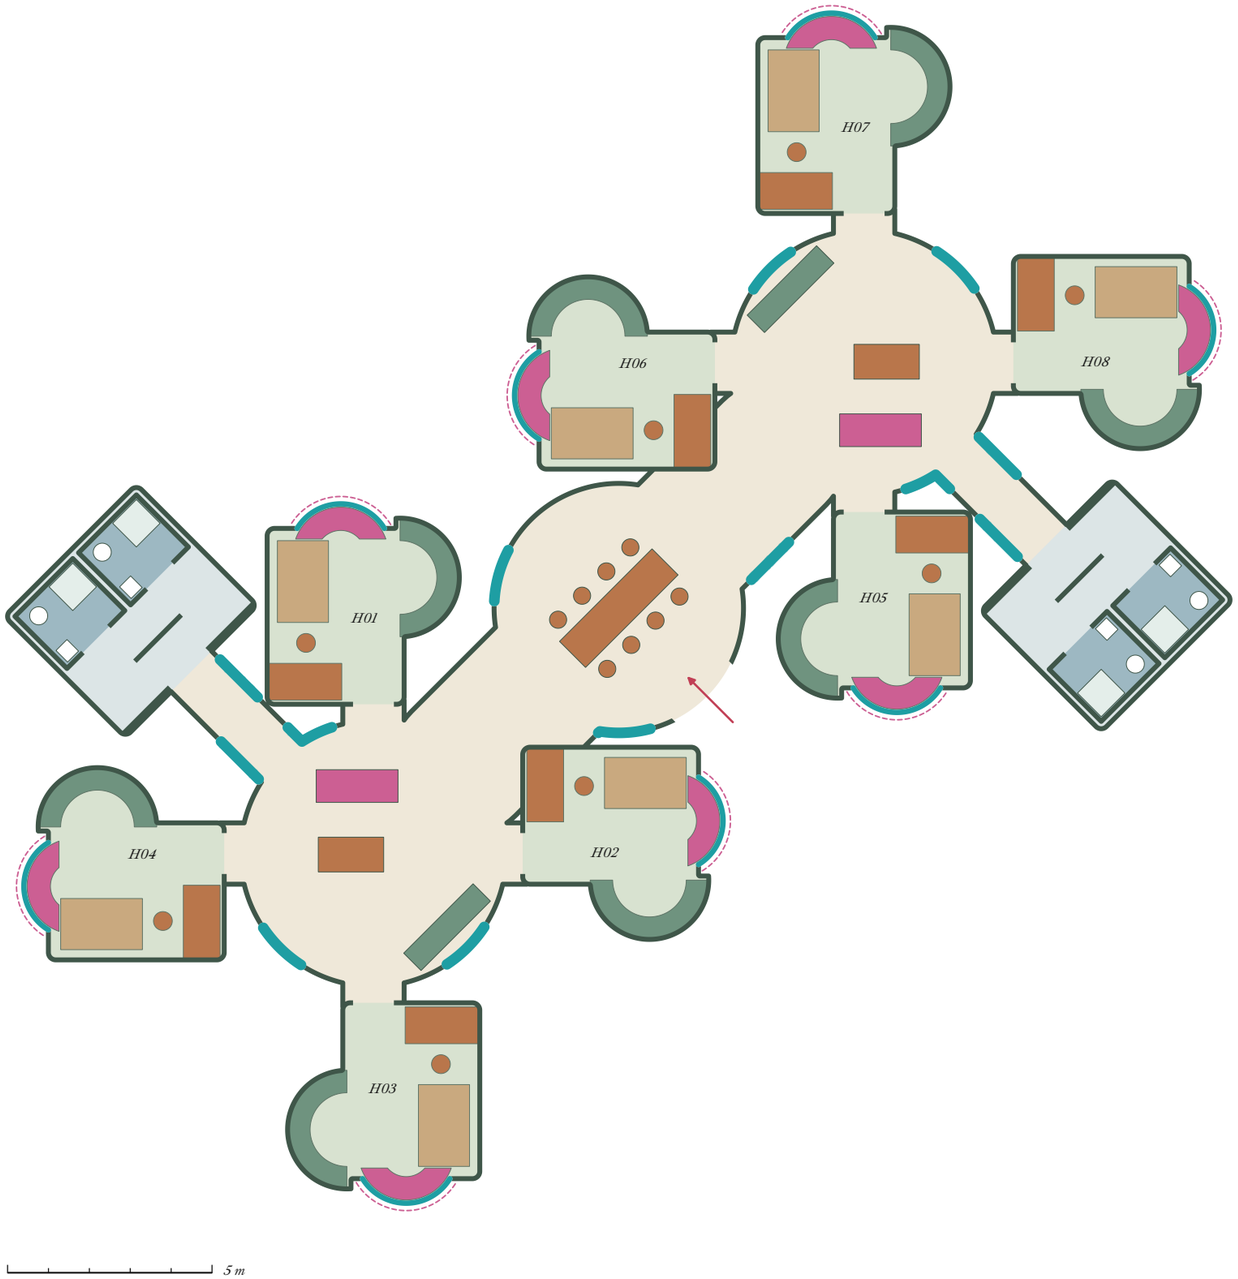

Planta. E 1:150

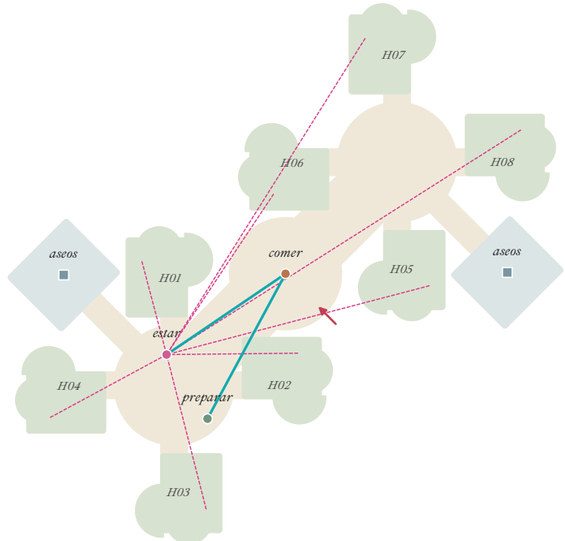

Lectura de la planta. Turquesa: preparar, comer y estar, cerca. Rosa: lo que el estar no debe invadir. E 1:330


Continuidad diagonal

V03 · ocho residentes


La convivencia se prolonga por un interior en diagonal de 4,50 m de ancho entre los dos círculos, sin aseos en su centro. La mesa de ocho queda en mitad de la continuidad.

El tramo se ensancha lo necesario para rodear la mesa. Es una unión larga, que atraviesa la casa de un extremo a otro.

305,44 m² de suelo · 329,47 m² de envolvente

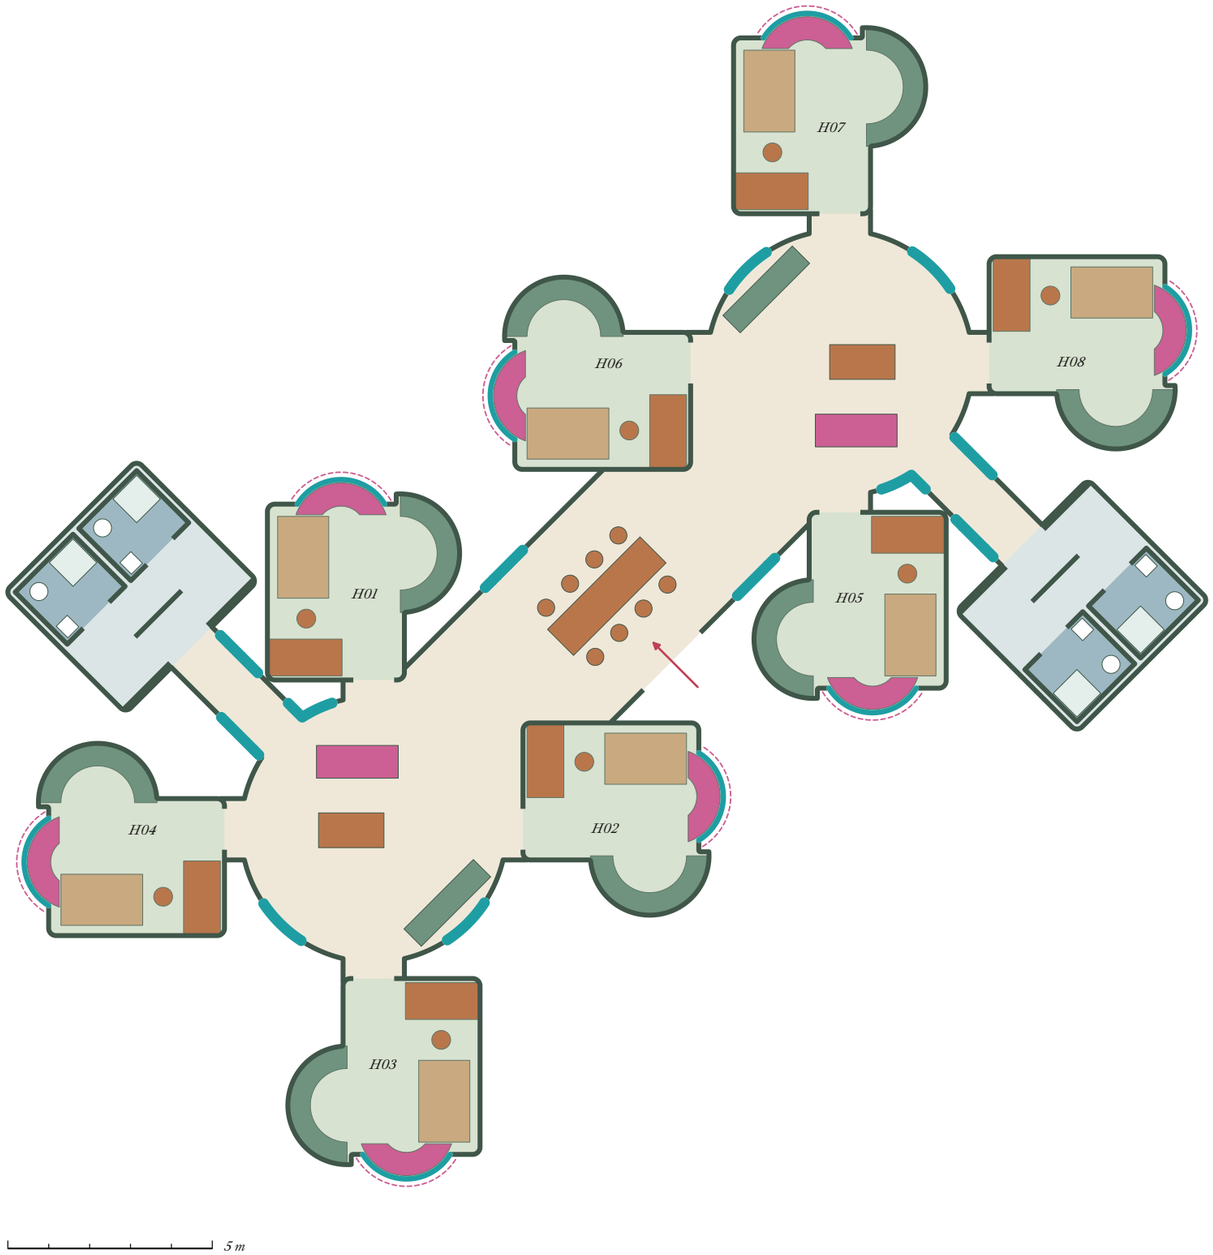

Planta. E 1:150

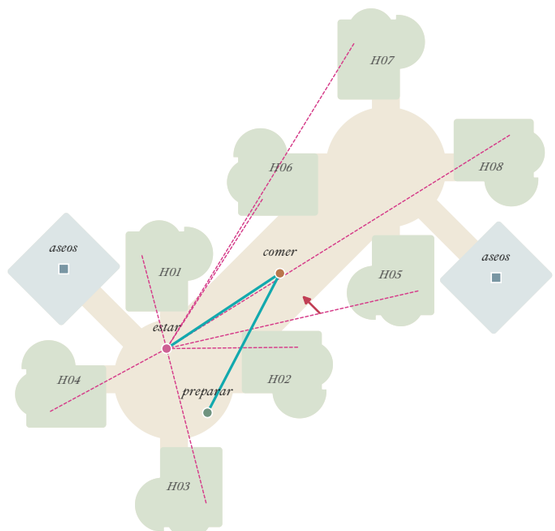

Lectura de la planta. Turquesa: preparar, comer y estar, cerca. Rosa: lo que el estar no debe invadir. E 1:330

10


Superficies

Lo que cuesta cada manera de convivir.

organización		*residentes*	*suelo m²*	*envolvente m²*	*aseos*
Convivencia continua	V01 U	4	134,17	144,28	2
Dos ámbitos	V02 U	4	137,67	147,80	2
Centro libre	V03 U	4	132,53	144,83	2
Pareja con umbral	V02 P	8	282,30	303,21	4
Encuentro mayor	V01 D	8	295,31	315,48	4
Casa común continua	V01 S	8	274,39	294,20	4
Plaza entre estancias	V03 D	8	310,37	335,46	4
Continuidad diagonal	V03 S	8	305,44	329,47	4

Por persona, la casa común continua se queda en 36,8 m², casi lo mismo que una casa de cuatro; la plaza entre estancias llega a 41,9.


Para cuarenta residentes hacen falta cinco grupos de ocho. Con la casa común continua la envolvente suma 1.471 m², dentro de los 1.500 m² del enunciado pero con poco margen para escaleras, zócalo y estructura. Con la plaza entre estancias, 1.677 m².

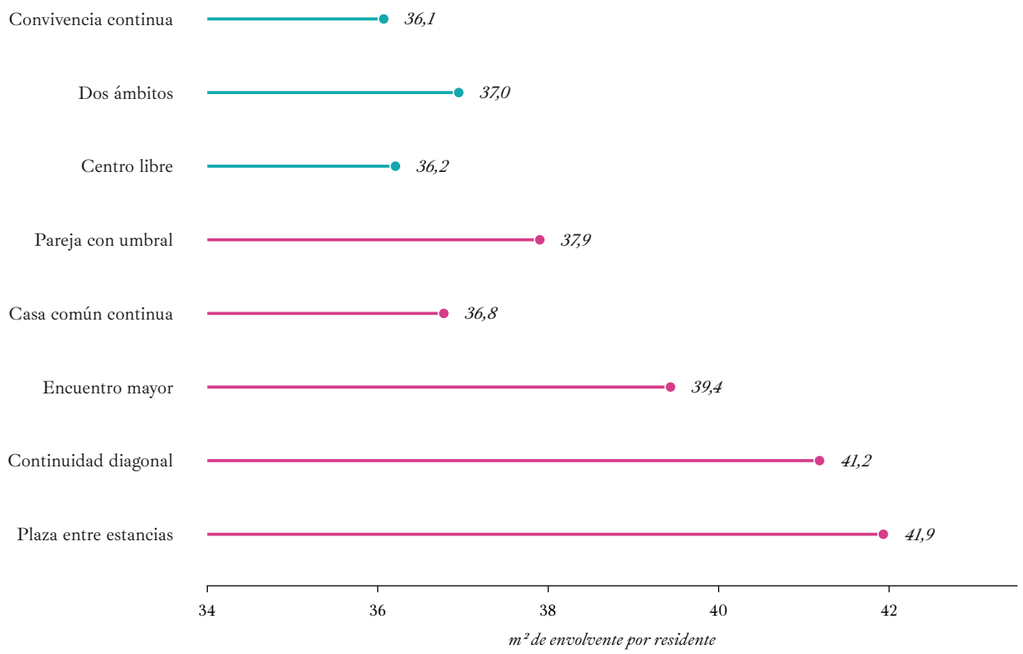

Cada decisión de convivencia tiene un precio en suelo. Las tres casas de cuatro ocupan entre 132 y 138 m²; las de ocho, entre 274 y 310 m². Los vestíbulos de servicio y los encuentros se pagan en superficie: entre la unión más compacta y la más expansiva hay 36 m² por grupo.

Suelo geométrico: incluye las huellas de las divisiones; no es superficie útil. Envolvente: el suelo expandido 12 cm.

Lo privado y lo común

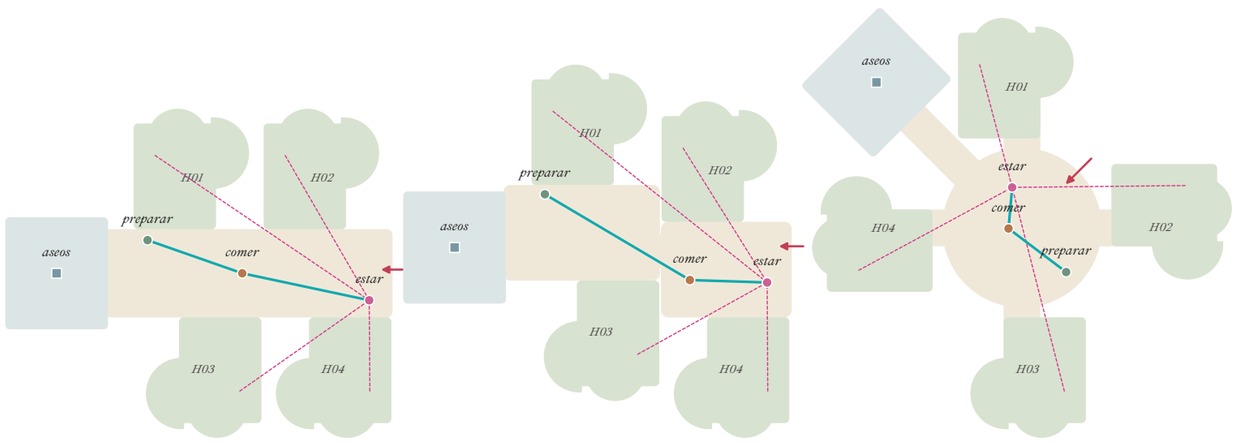

a *Convivencia continua · E 1:250*

b *Dos ámbitos · E 1:250*

c *Centro libre · E 1:250*

d *Casa común continua · E 1:330*

e *Continuidad diagonal · E 1:330*

Lo privado

Dormir, vestirse, guardar la ropa, trabajar en el tablero y retirarse en la bow. La cama nunca ocupa el eje de la puerta.

Lo compartido

Preparar comida, comer, conversar, recibir y limpiar. El vestíbulo de los aseos es una transición de servicio, no una estancia.

Dos grupos

En la pareja con umbral, cada casa conserva su cocina y su mesa; el umbral es el único lugar de las ocho.

Un grupo

En el encuentro mayor y en la casa común continua, la llegada, la comida, el trabajo y la estancia pertenecen a las ocho, y nadie atraviesa otra habitación para llegar a la suya.

Dos centros

En la plaza y en la diagonal, el centro de cada ámbito vuelve a ser habitable. Las dos cocinas pueden formar dos subgrupos dentro del grupo, y eso también es una manera de convivir.

Acuerdos

Compartir requiere acuerdos de uso, de cuidado y de retirada. Una planta abierta no los garantiza, ni obliga a estar siempre en grupo.

Tres casas de cuatro y cinco maneras de juntarlas. El siguiente paso es llevarlas a la parcela, compactar los servicios sin devolverlos al centro y probar la luz en sección.

G3 Proyectos · Vivienda temporal para jóvenes en El Rastro · Universidad Europea de Madrid · Octubre 2026.

Las escenas son inventadas para el proyecto. Parcela: Catastro, referencia 0134911VK4703C. Sol: modelo 2,5D con alturas vecinas estimadas por número de plantas.

Plantas dibujadas en metros desde la geometría del proyecto. Suelo geométrico: incluye las huellas de las divisiones; no es superficie útil. Envolvente: el suelo expandido 12 cm.

Tipografía: Ibarra Real Nova.

