
V01 · unidad de cuatro personas

PLANTA · E 1:100 · corte +1,20 m · pavimento +0,00 m

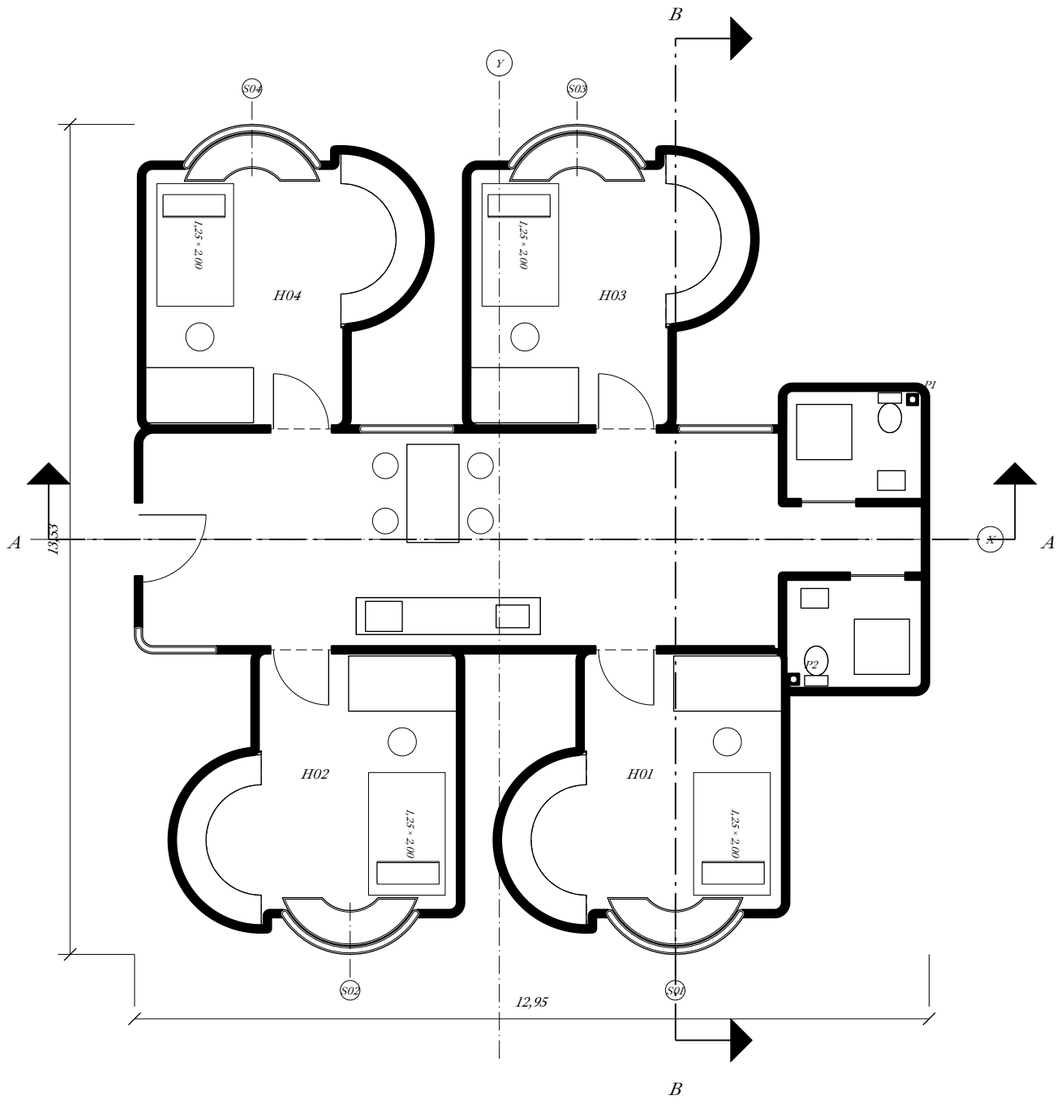

PROGRAMA

4 personas / 4 dormitorios

Pavimento geométrico: 122,69 m²

2 baños en borde continuo

LECTURA DEL DIBUJO

Negro sólido: material seccionado

0,18 mm: carpinterías y equipamiento

0,13 mm: proyección visible

Discontinua: elementos sobre el corte

Trazo-punto: ejes de referencia

S: simetría local de la bow window

CRITERIOS APLICADOS

Baños integrados en la envolvente

Correderas en baños; sin barrido interior

Sofás retirados de estas plantas

Montantes dentro del borde de servicios

Huecos exteriores sin bajantes superpuestas

Sin simetría global acreditada


X/Y: referencias; no son ejes estructurales

Recta: entrada y dormitorios a la calle (izquierda), baños al fondo

0 1 2 5 m

V02 · unidad de cuatro personas

PLANTA · E 1:100 · corte +1,20 m · pavimento +0,00 m

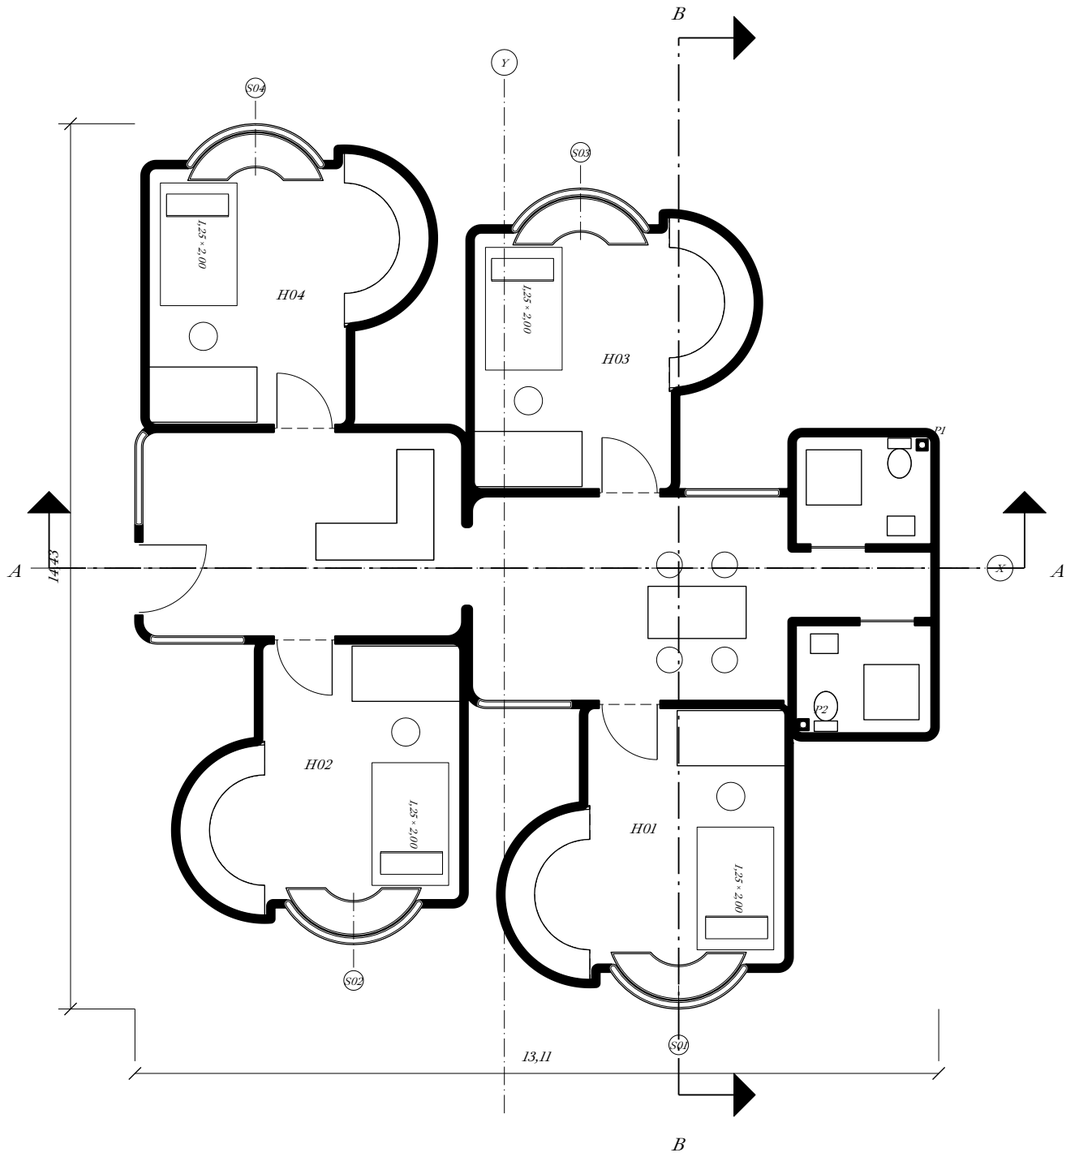

PROGRAMA

4 personas / 4 dormitorios

Pavimento geométrico: 121,49 m²

2 baños en borde continuo

LECTURA DEL DIBUJO

Negro sólido: material seccionado

0,18 mm: carpinterías y equipamiento

0,13 mm: proyección visible

Discontinua: elementos sobre el corte

Trazo-punto: ejes de referencia

S: simetría local de la bow window

CRITERIOS APLICADOS

Baños integrados en la envolvente

Correderas en baños; sin barrido interior

Sofás retirados de estas plantas

Montantes dentro del borde de servicios

Huecos exteriores sin bajantes superpuestas

Sin simetría global acreditada


X/Y: referencias; no son ejes estructurales

Recta: entrada y dormitorios a la calle (izquierda), baños al fondo

0 1 2 5 m

V03 · unidad de cuatro personas

PLANTA · E 1:100 · corte +1,20 m · pavimento +0,00 m

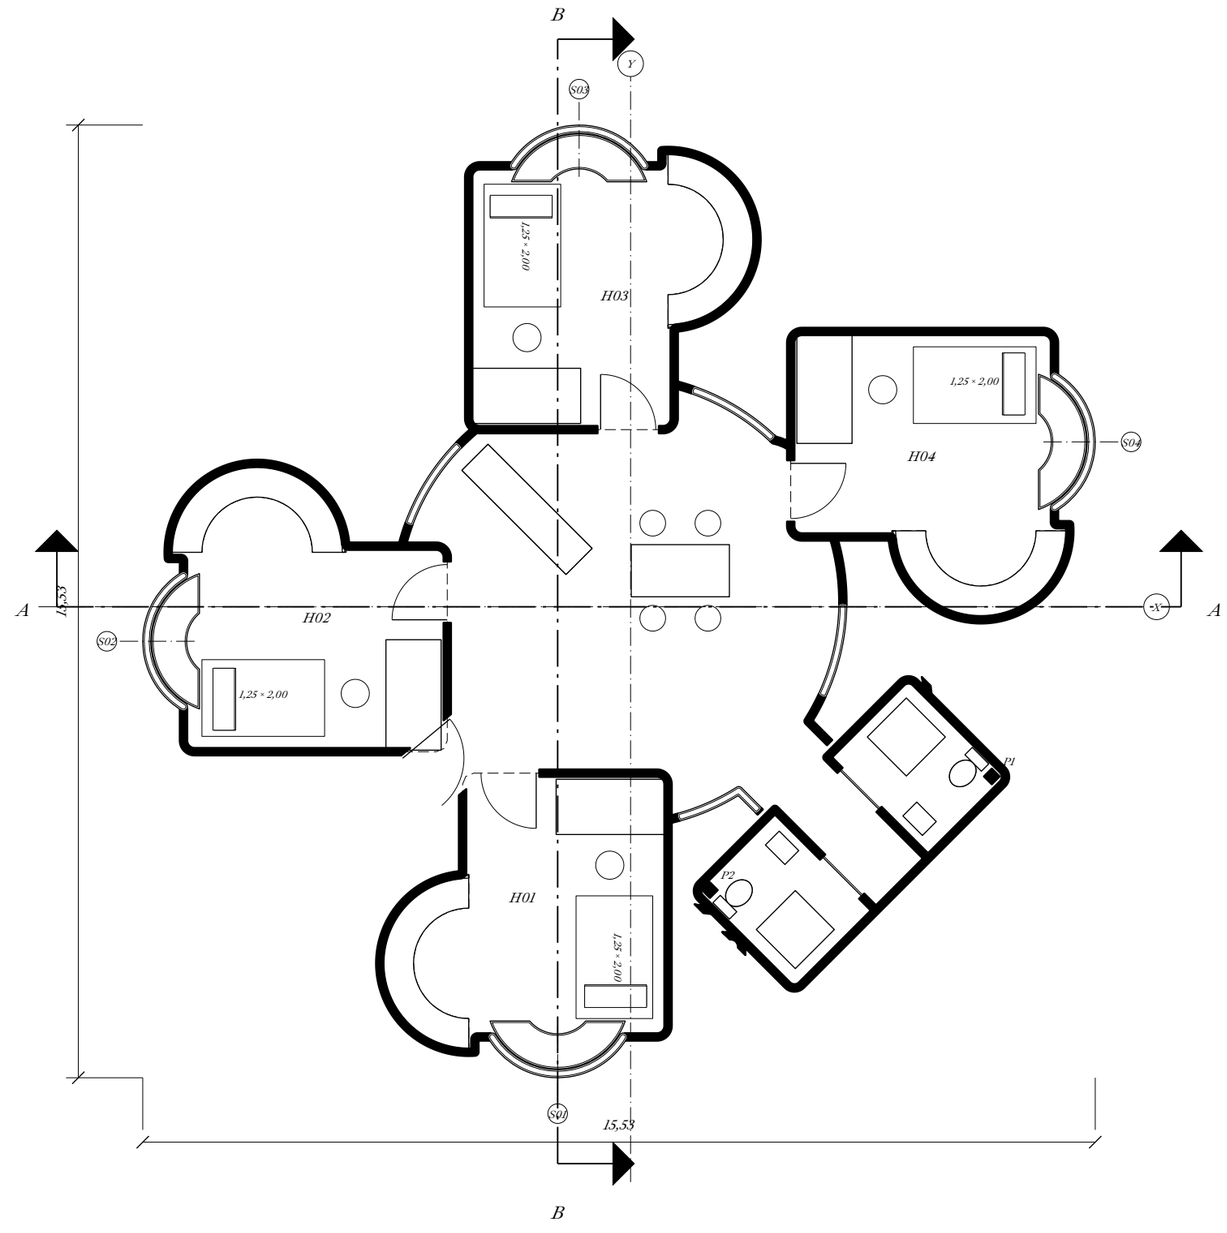

PROGRAMA

4 personas / 4 dormitorios

Pavimento geométrico: 121,08 m²

2 baños en borde continuo

LECTURA DEL DIBUJO

Negro sólido: material seccionado

0,18 mm: carpinterías y equipamiento

0,13 mm: proyección visible

Discontinua: elementos sobre el corte

Trazo-punto: ejes de referencia

S: simetría local de la bow window

CRITERIOS APLICADOS

Baños integrados en la envolvente

Correderas en baños; sin barrido interior

Sofás retirados de estas plantas

Montantes dentro del borde de servicios

Huecos exteriores sin bajantes superpuestas

Sin simetría global acreditada


X/Y: referencias; no son ejes estructurales

Recta: entrada y dormitorios a la calle (izquierda), baños al fondo

0 1 2 5 m

E02 · dos unidades / ocho personas / planta elevada

PLANTA · E1:100 · corte +5,40 m · pavimento +4,20 m

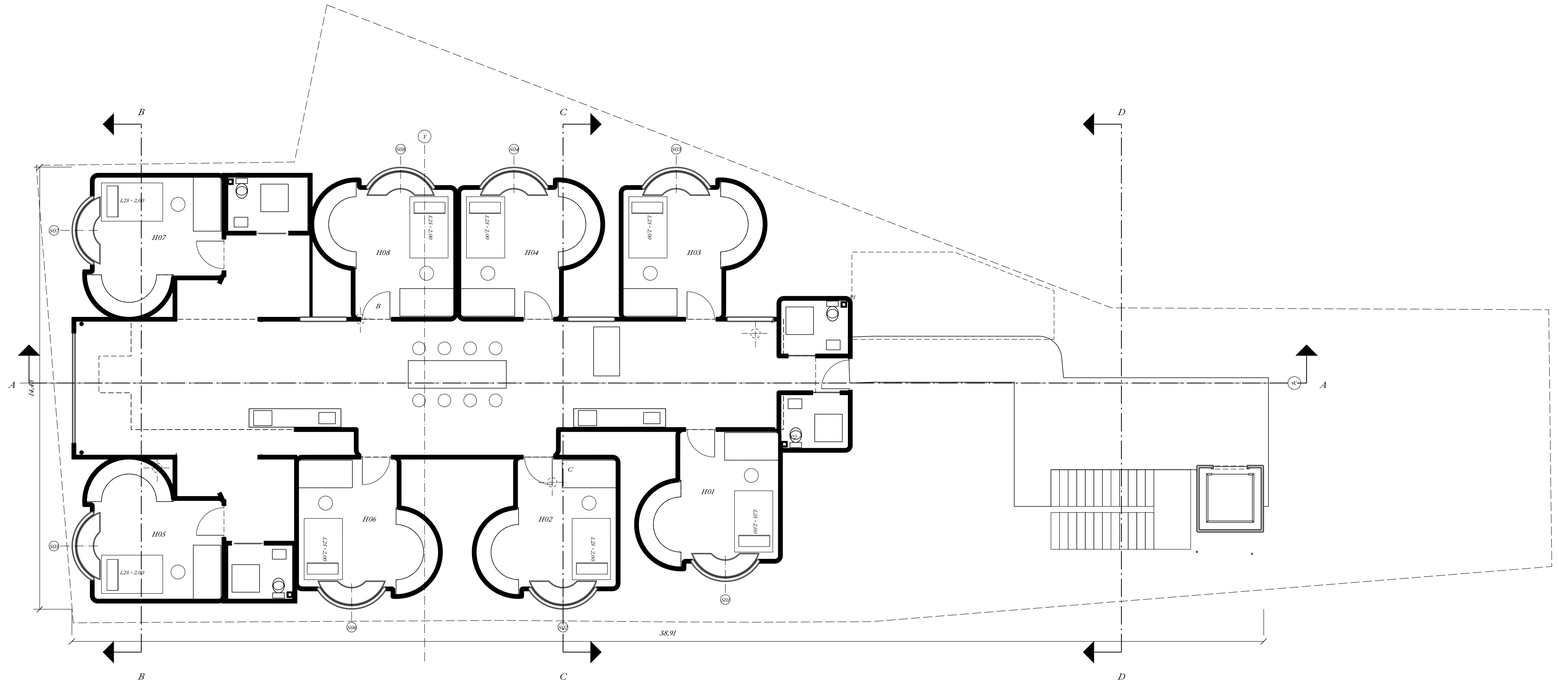

Corte negro 0,35 mm / carpintería 0,18 mm / proyección 0,13 mm / superior discontinua 0,10 mm


X/Y: referencia geométrica. Puntos A-D: apoyos medidos del modelo, sin validación estructural.

P: patinillos del borde de servicios. Sofás retirados. Escalera y ascensor conservan su posición.

0 1 2 5 m

Parcela · planta baja pública / biblioteca, estudio y trabajo compartido

PLANTA · E 1:100 · corte +1,20 m · pavimento +0,00 m

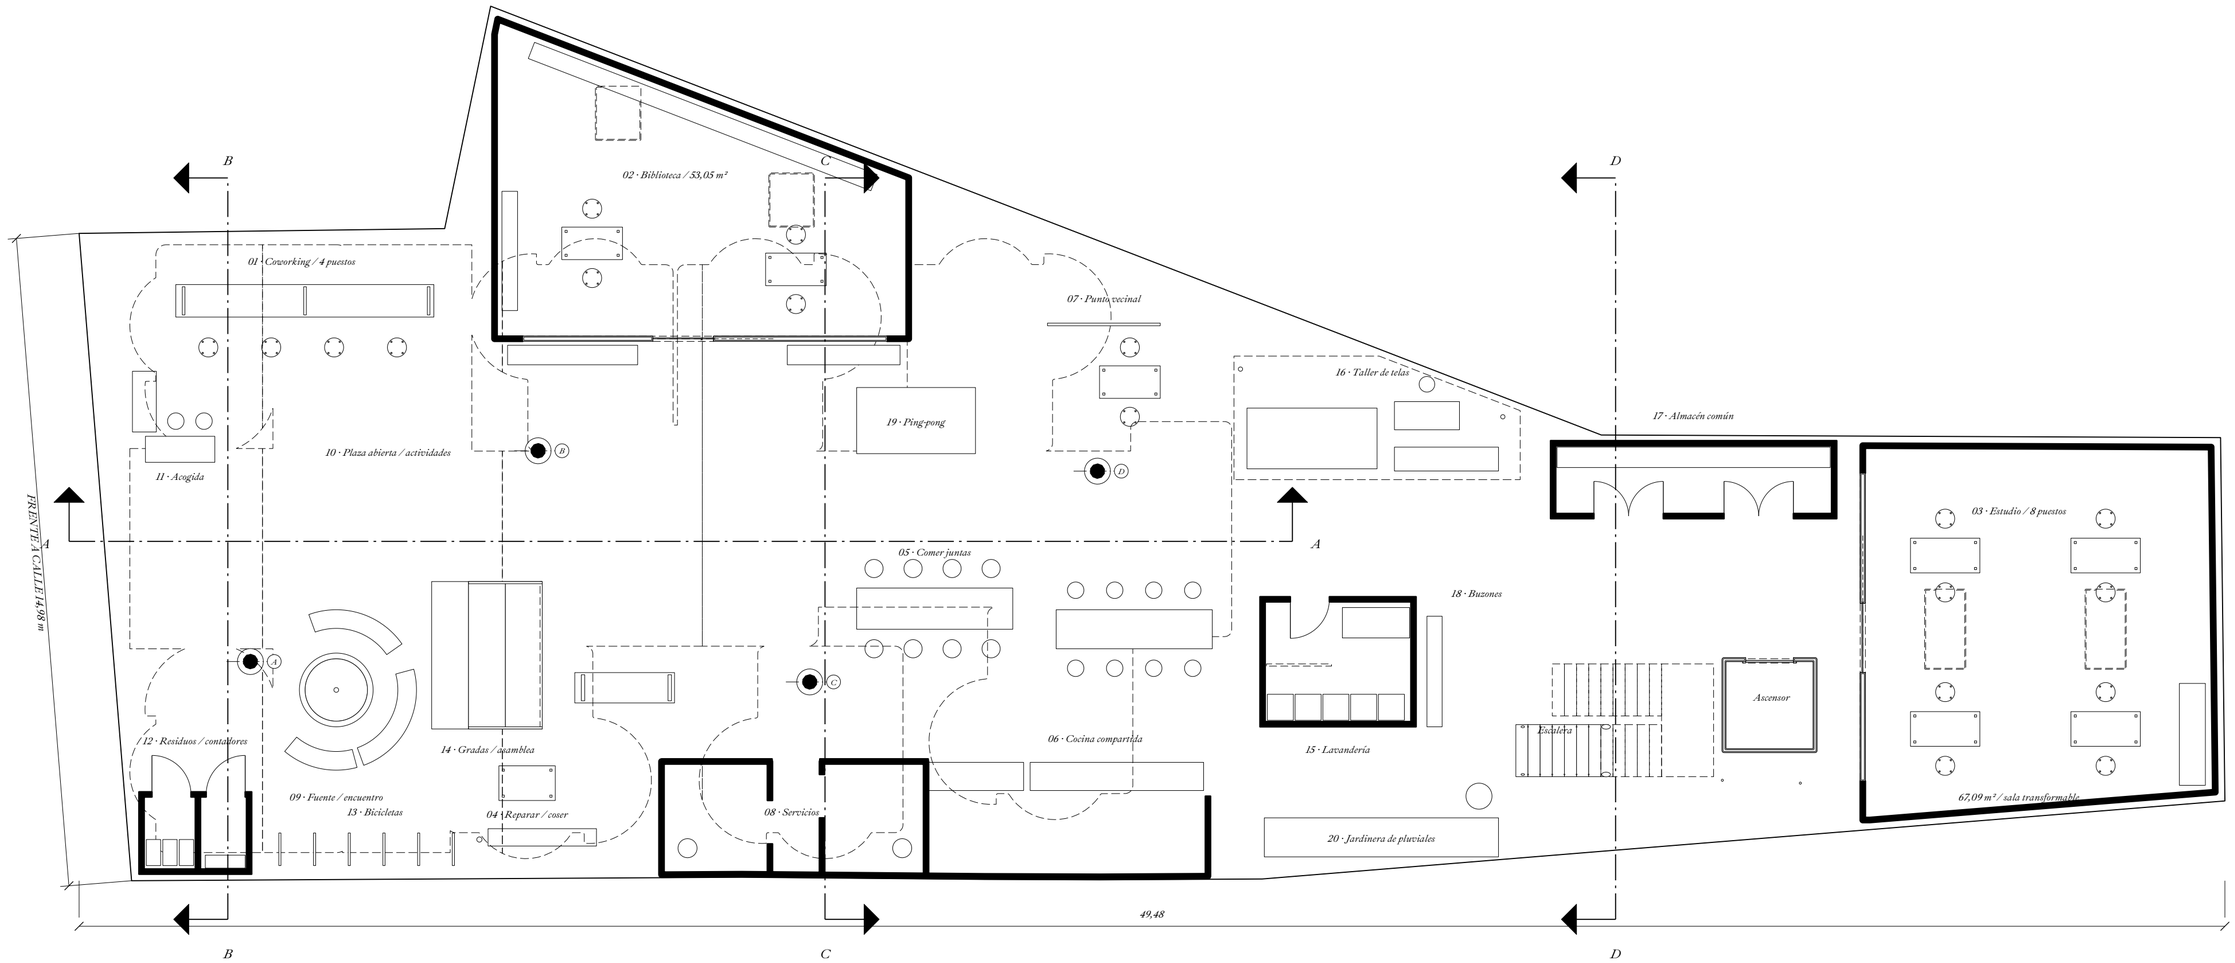

Corte negro 0,35 mm / carpintería 0,18 mm / proyección 0,13 mm / superior discontinua 0,10 mm


X/Y: referencia geométrica. Puntos A-D: apoyos medidos del modelo, sin validación estructural.

Biblioteca y estudio con luz cenital. Mesas plegables / paneles móviles. Planta baja sin vivienda privada.

0 1 2 5 m

Parcela · planta baja pública / exposición vecinal del domingo

PLANTA · E 1:100 · corte +1,20 m · pavimento +0,00 m

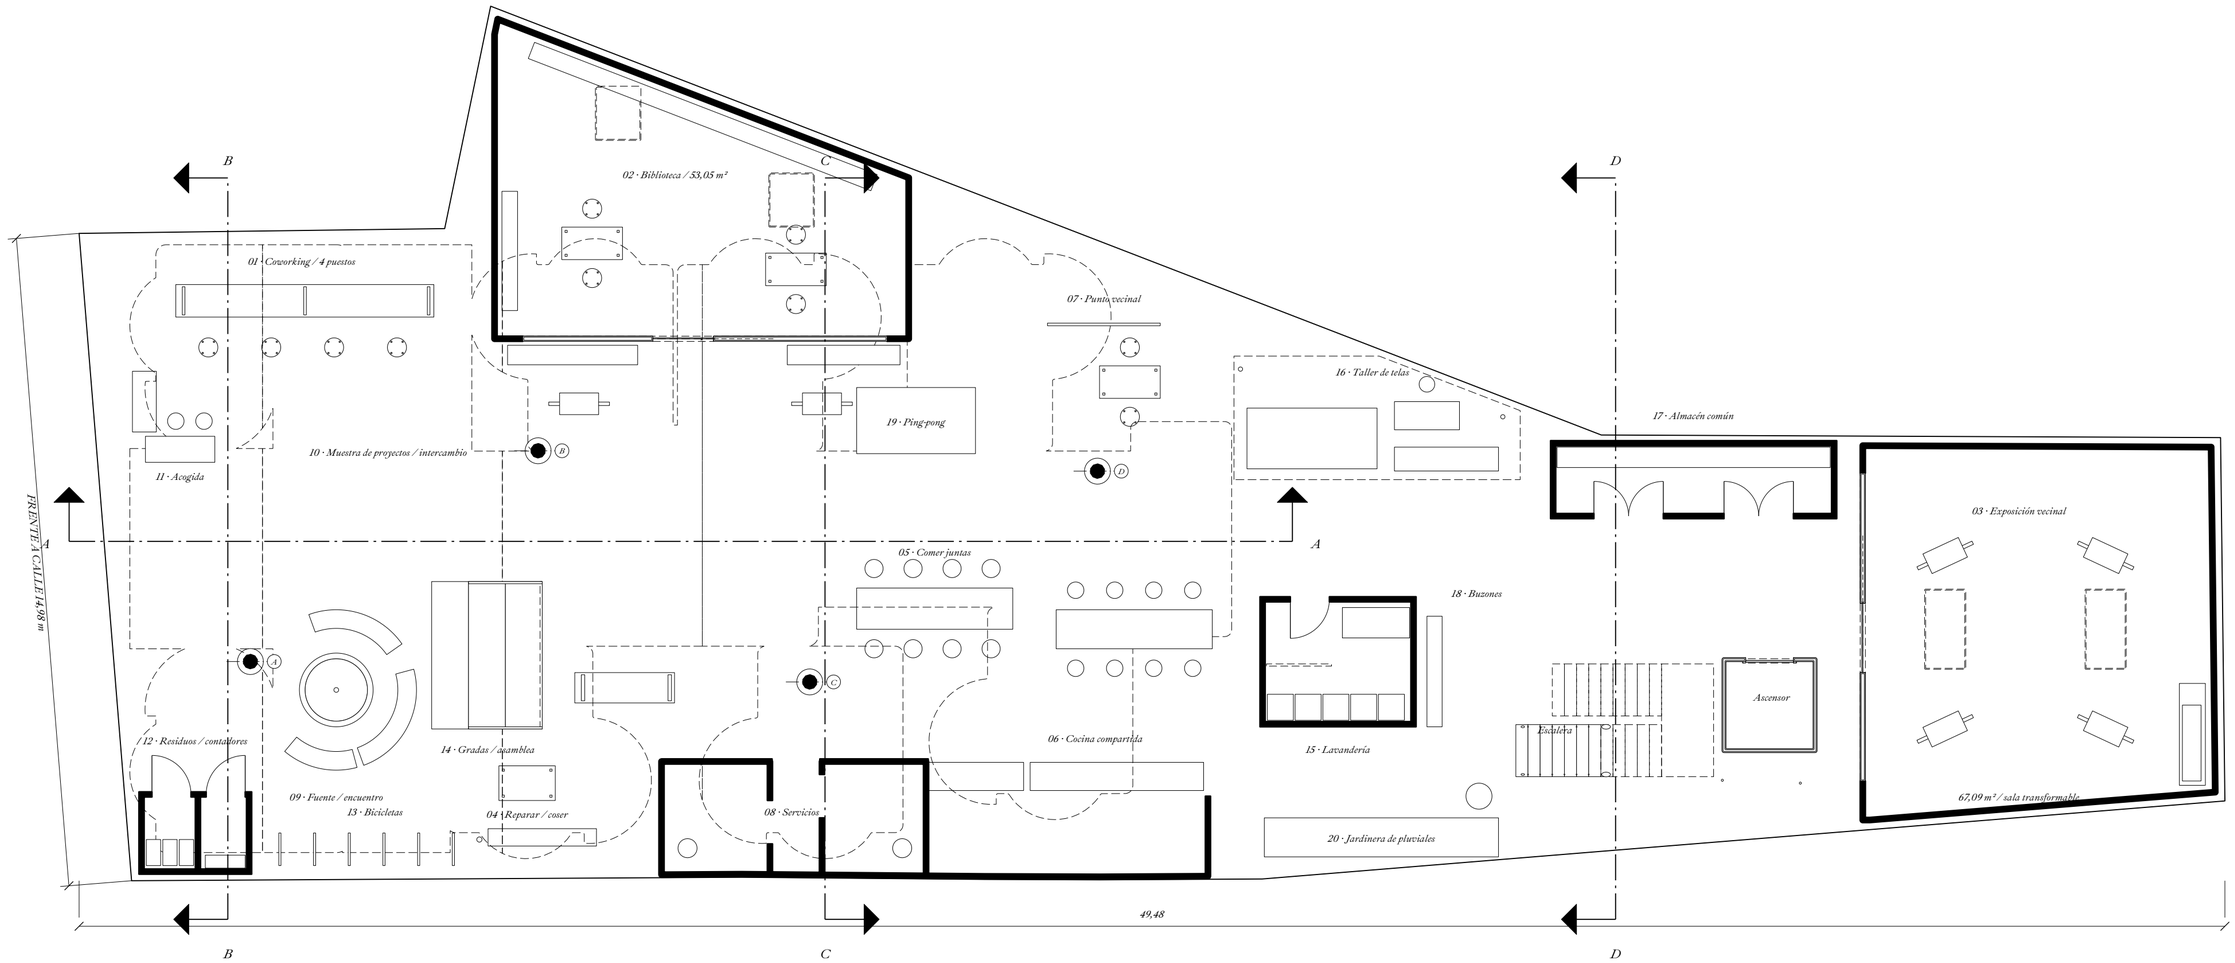

Corte negro 0,35 mm / carpintería 0,18 mm / proyección 0,13 mm / superior discontinua 0,10 mm

X/Y: referencia geométrica. Puntos A-D: apoyos medidos del modelo, sin validación estructural.

Biblioteca y estudio con luz cenital. Mesas plegables / paneles móviles. Planta baja sin vivienda privada.

0 1 2 5 m