

V01 · unidad de cuatro personas

SECCIONES · E 1:50 · corte exacto desde Rhino · cota de pavimento +0,00 m

SECCIÓN A · longitudinal por el eje X, mirando a norte

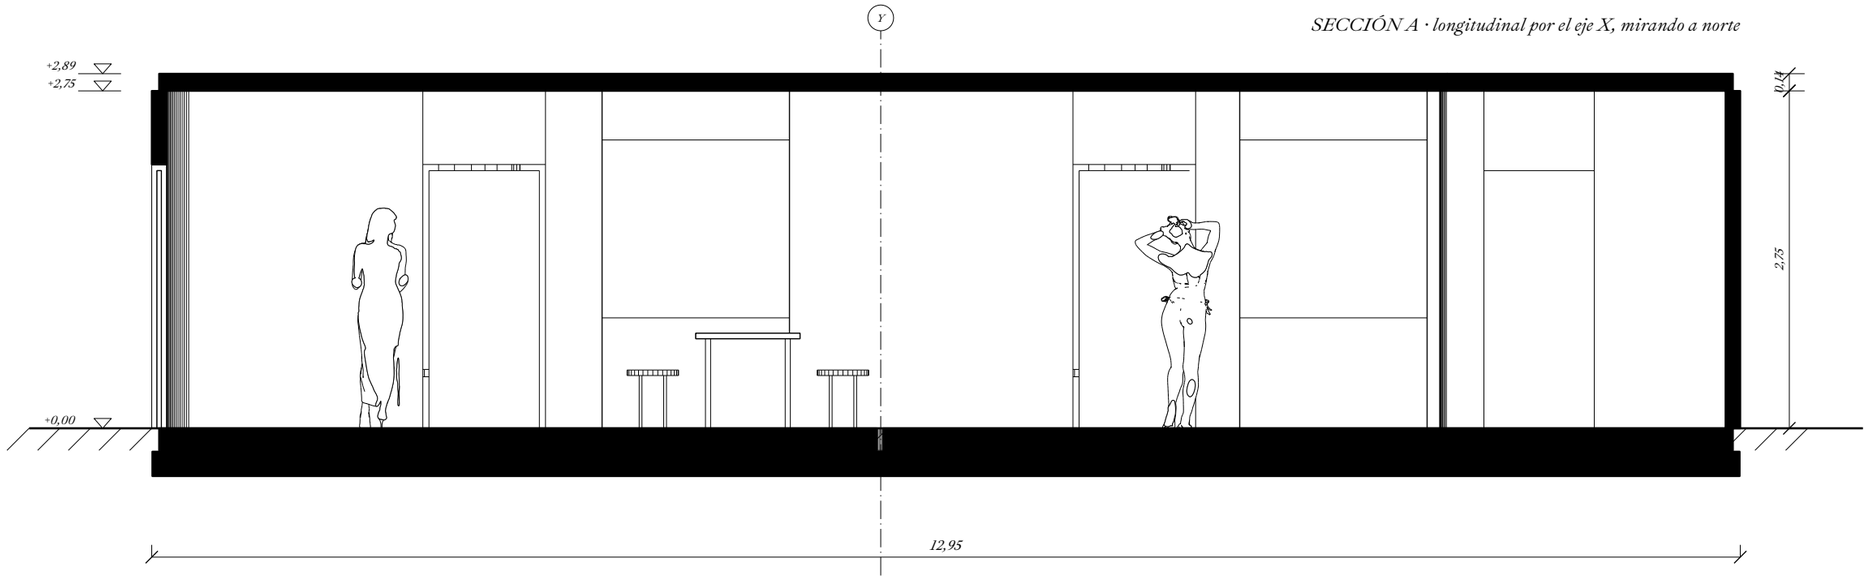

SECCIÓN B · transversal por la bow window S01 (x = 8,52), mirando a levante

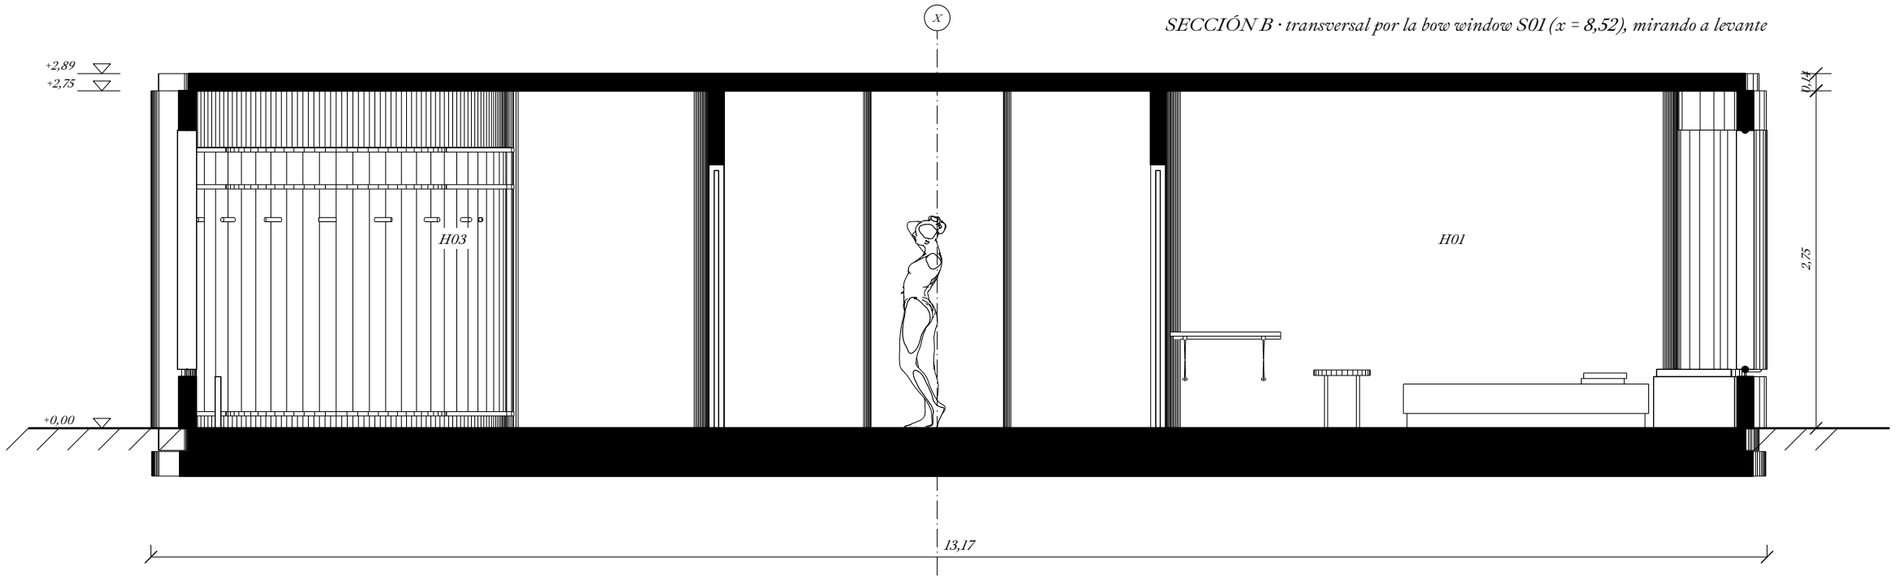

LECTURA DEL DIBUJO

Negro sólido: material seccionado

0,18 mm: carpinterías y equipamiento cortado

Proyección: 0,10 / 0,07 / 0,05 mm según fondo

Trazo-punto: ejes de la planta

ORIGEN DE LA GEOMETRÍA

Corte: intersección exacta sólido / plano

Proyección: líneas ocultas de Rhino

Personas: figuras del modelo (PERSONAS.3dm)

Cotas en metros, medidas en el modelo

CTE

DB SUA: altura libre de paso ≥ 2,20 m

Alturas leídas en la cadena de la derecha

Sobretecho textil retirado del dibujo

0 1 2 5 m


G3 · revisión arquitectónica medida desde Rhino · anteproyecto

S01


V02 · unidad de cuatro personas

SECCIONES · E 1:50 · corte exacto desde Rhino · cota de pavimento +0,00 m

SECCIÓN A · longitudinal por el eje X, mirando a norte

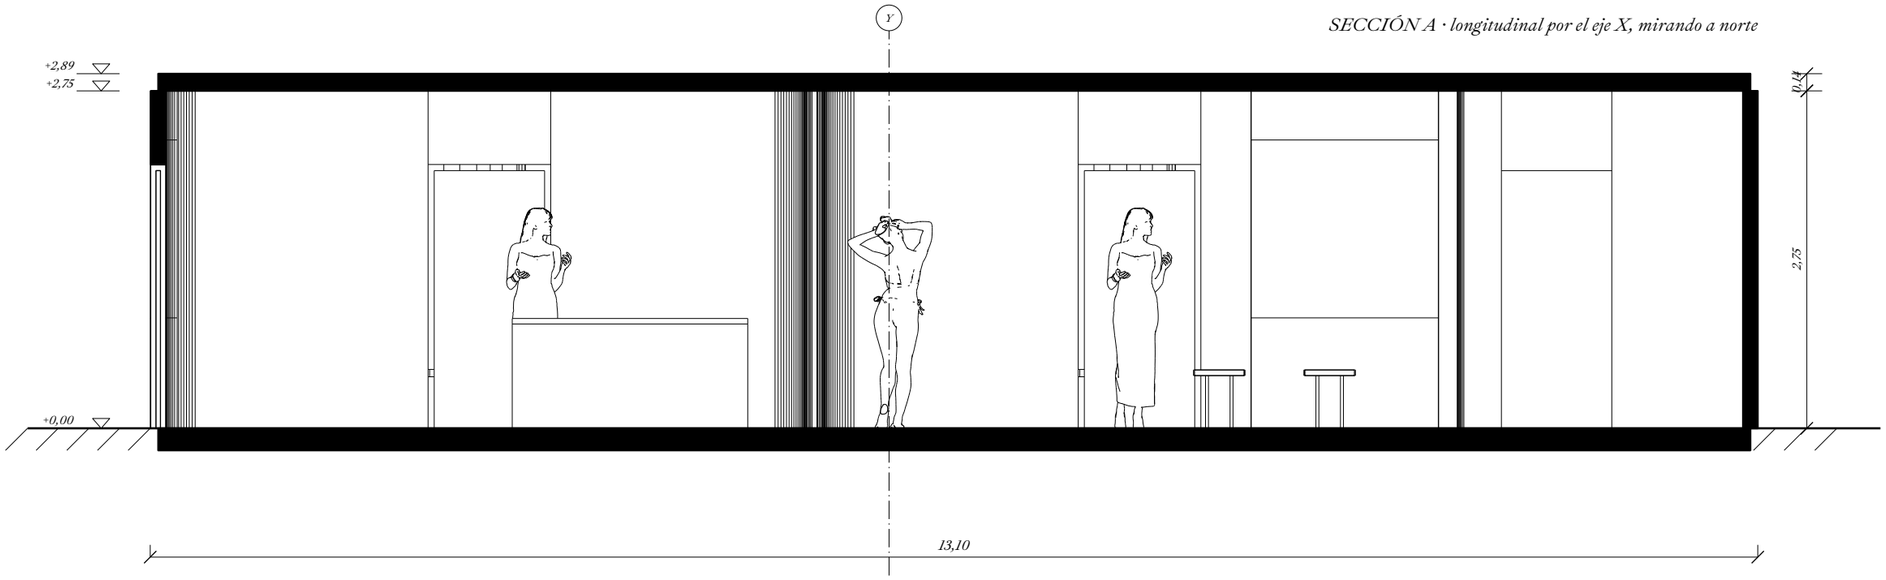

SECCIÓN B · transversal por la bow window S01 (x = 36,94), mirando a levante

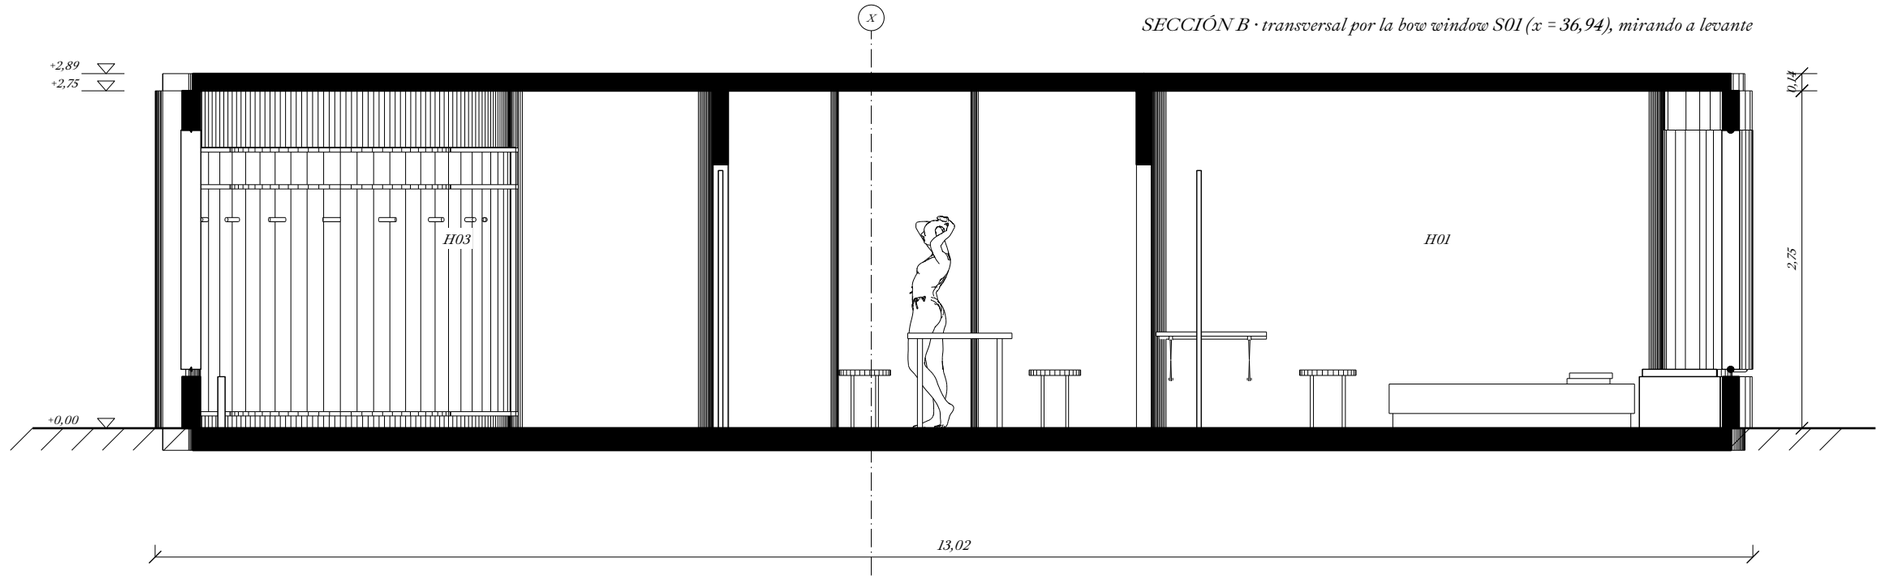

LECTURA DEL DIBUJO

Negro sólido: material seccionado

0,18 mm: carpinterías y equipamiento cortado

Proyección: 0,10 / 0,07 / 0,05 mm según fondo

Trazo-punto: ejes de la planta

ORIGEN DE LA GEOMETRÍA

Corte: intersección exacta sólido / plano

Proyección: líneas ocultas de Rhino

Personas: figuras del modelo (PERSONAS.3dm)

Cotas en metros, medidas en el modelo

CTE

DB SUA: altura libre de paso ≥ 2,20 m

Alturas leídas en la cadena de la derecha

Sobretecho textil retirado del dibujo

0 1 2 5 m


G3 · revisión arquitectónica medida desde Rhino · anteproyecto

S02


V03 · unidad de cuatro personas

SECCIONES · E 1:50 · corte exacto desde Rhino · cota de pavimento +0,00 m

SECCIÓN A · longitudinal por el eje X, mirando a norte

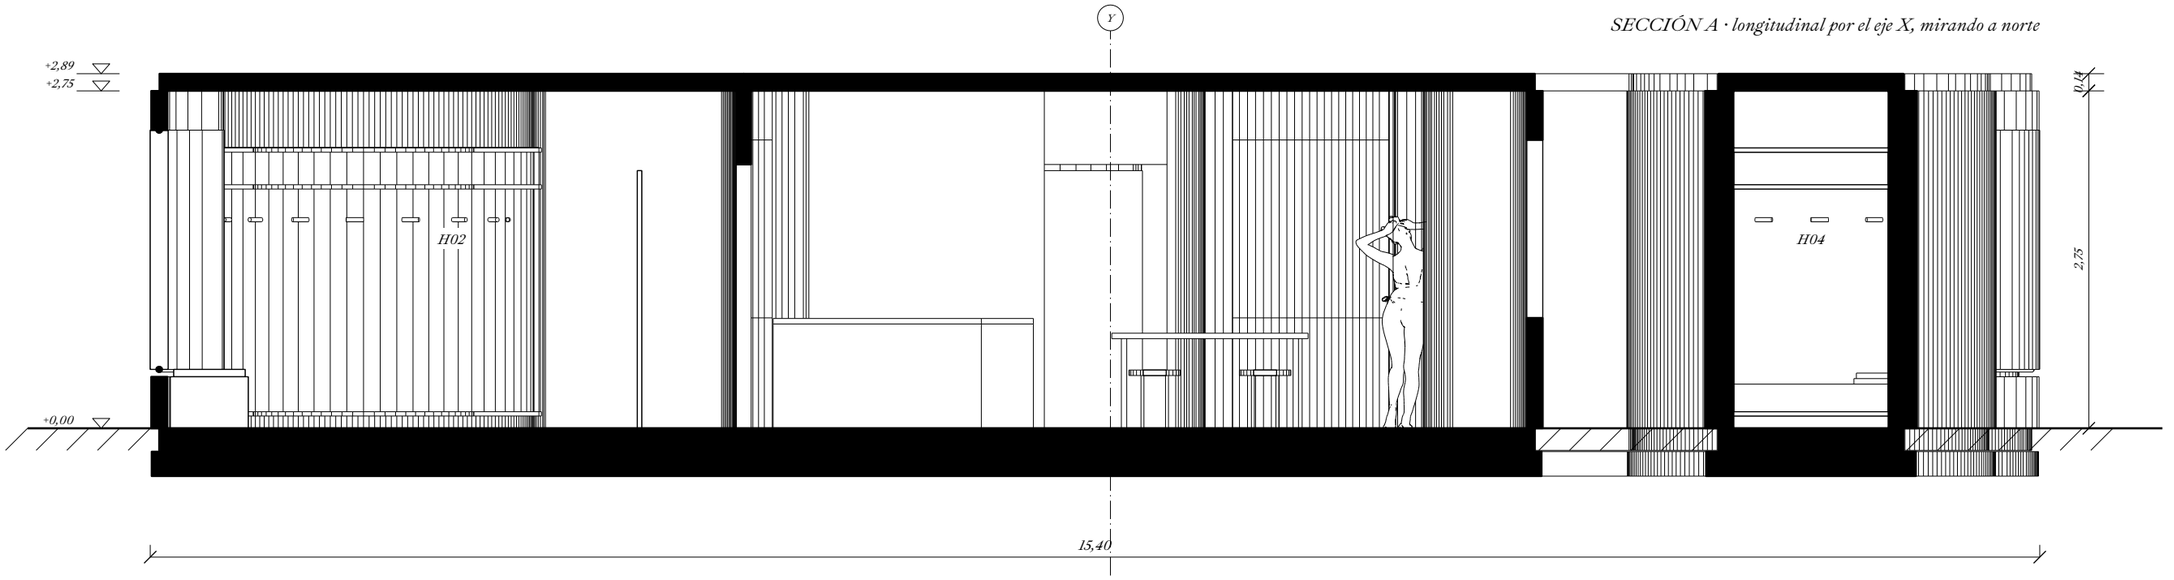

SECCIÓN B · transversal por la bow window S01 (x = 62,38), mirando a levante

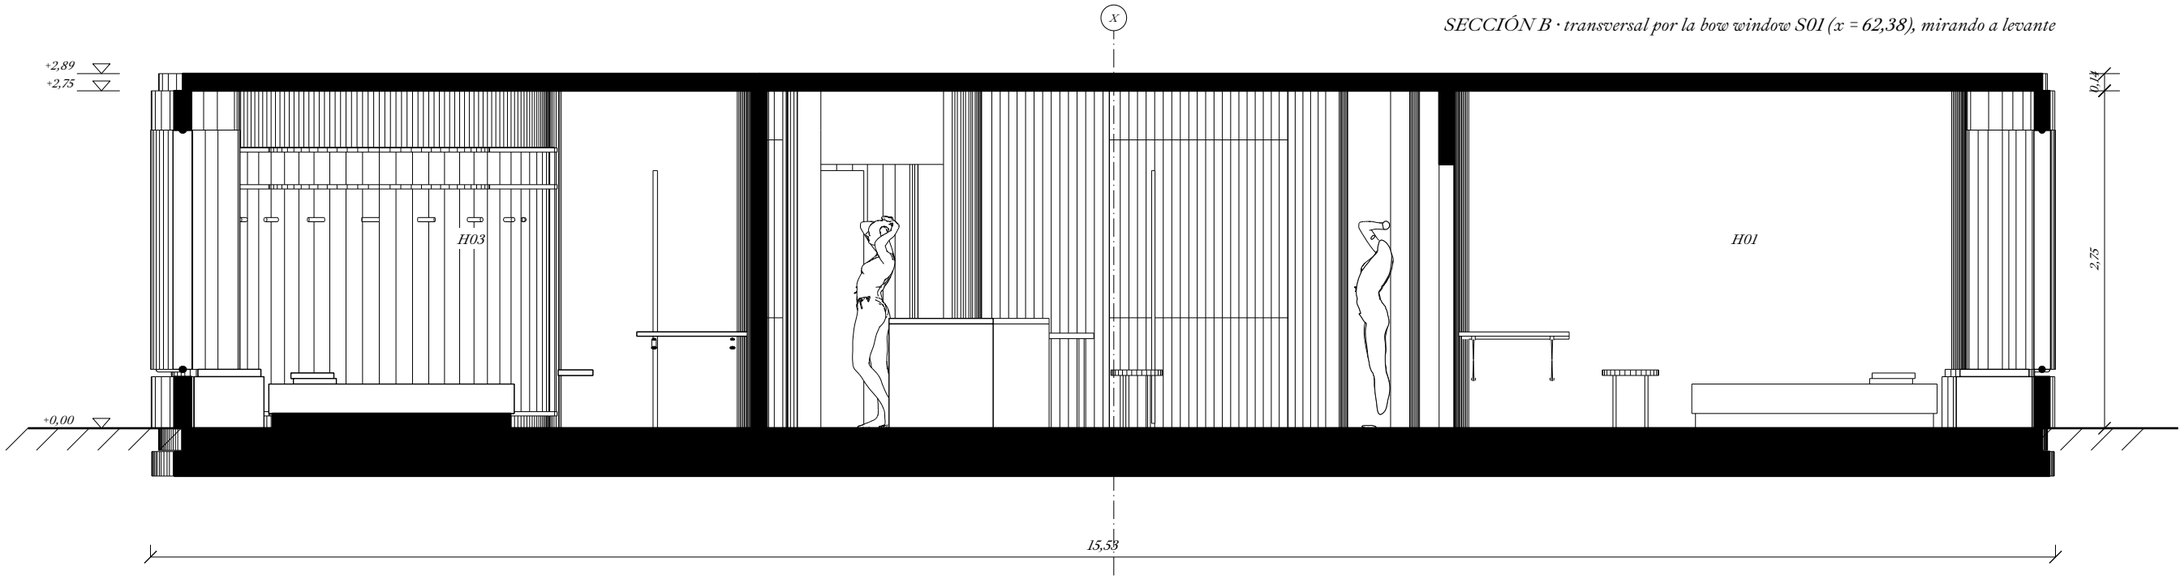

LECTURA DEL DIBUJO

Negro sólido: material seccionado

0,18 mm: carpinterías y equipamiento cortado

Proyección: 0,10 / 0,07 / 0,05 mm según fondo

Trazo-punto: ejes de la planta

ORIGEN DE LA GEOMETRÍA

Corte: intersección exacta sólido / plano

Proyección: líneas ocultas de Rhino

Personas: figuras del modelo (PERSONAS.3dm)

Cotas en metros, medidas en el modelo

CTE

DB SUA: altura libre de paso ≥ 2,20 m

Alturas leídas en la cadena de la derecha

Sobretecho textil retirado del dibujo

0 — 1 — 2 — 5 m


G3 · revisión arquitectónica medida desde Rhino · anteproyecto

S03


E02 · dos unidades / ocho personas / planta elevada

SECCIONES · E 1:100 · corte exacto desde Rhino · pavimento planta baja +0,00 m / planta elevada +4,20 m


SECCIÓN A · longitudinal por el eje X, mirando a norte

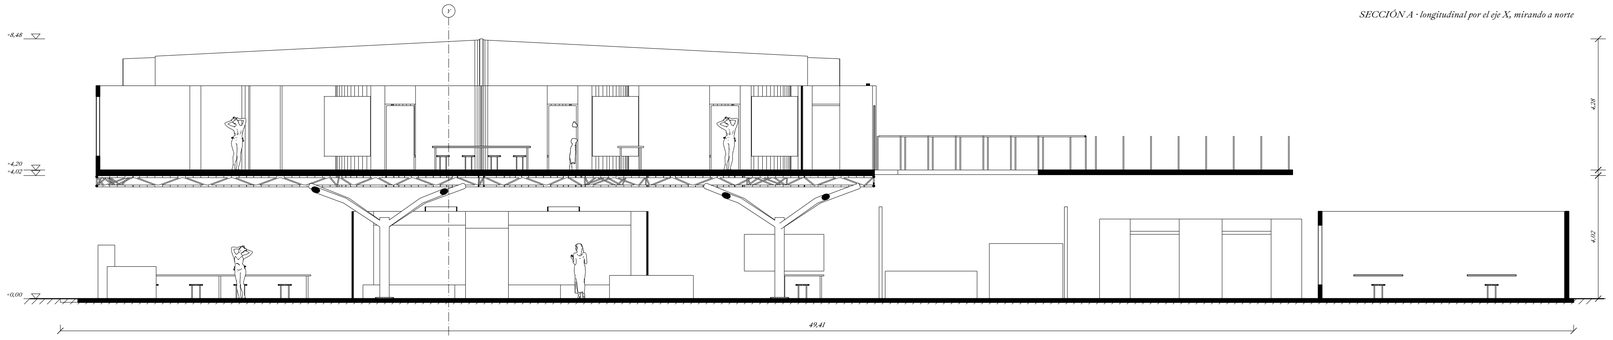


SECCIÓN B · transversal por H07 y H05, mirando a la calle

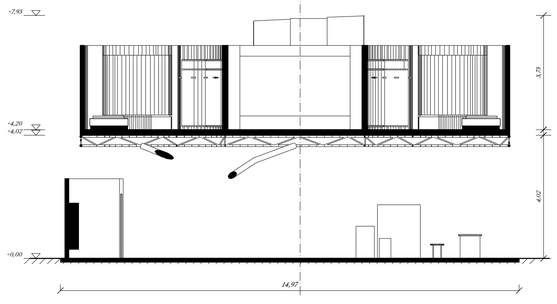

SECCIÓN C · transversal por la bow window S02 y la biblioteca (x = 28,75)

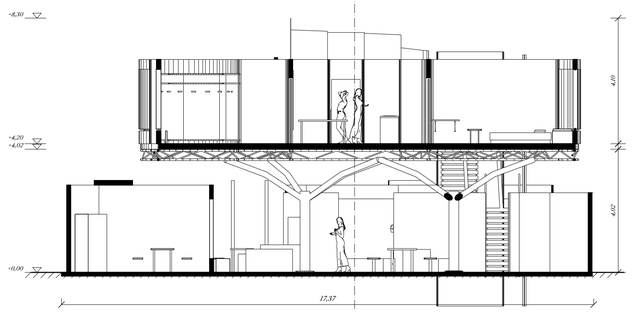

SECCIÓN D · transversal por la escalera, mirando al edificio

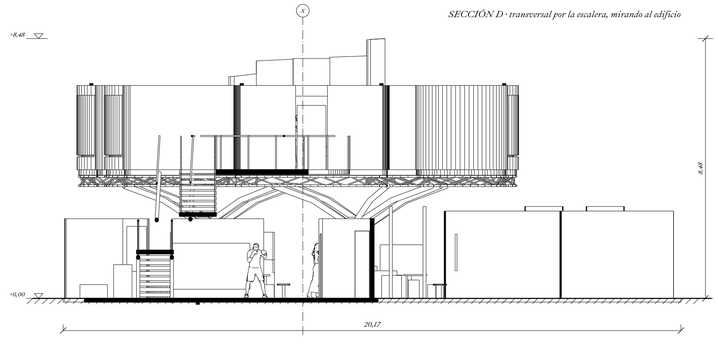

Corte negro 0,35 mm / carpintería y equipamiento cortado 0,18 mm / proyección visible 0,13 mm / ejes trazo-punto

Corte: intersección exacta de cada sólido de Rhino con el plano. Proyección: HiddenLineDrawing de Rhino de lo que queda detrás del plano.

Cotas y niveles medidos en el modelo. DB SUA: altura libre > 2,20 m en la planta baja bajo la bandeja y en las habitaciones.

0 1 2 5 m

G5 · revisión arquitectónica medida desde Rhino · anteproyecto