

# *V01 · unidad de cuatro personas*

*SECCIONES · E 1:50 · corte exacto desde Rhino · cota de pavimento +0,00 m*

*SECCIÓN A · longitudinal por el eje X, mirando a norte*

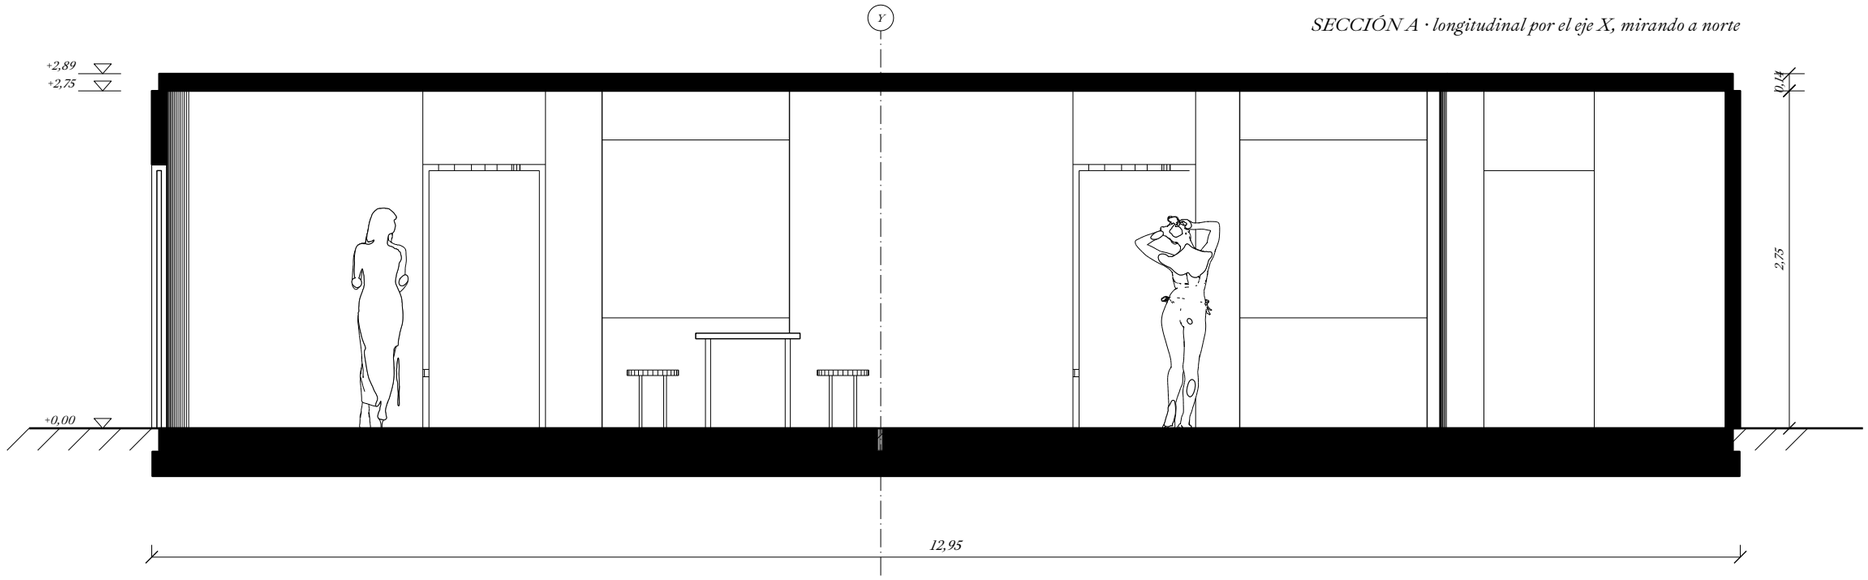


*SECCIÓN B · transversal por la bow window S01 (x = 8,52), mirando a levante*

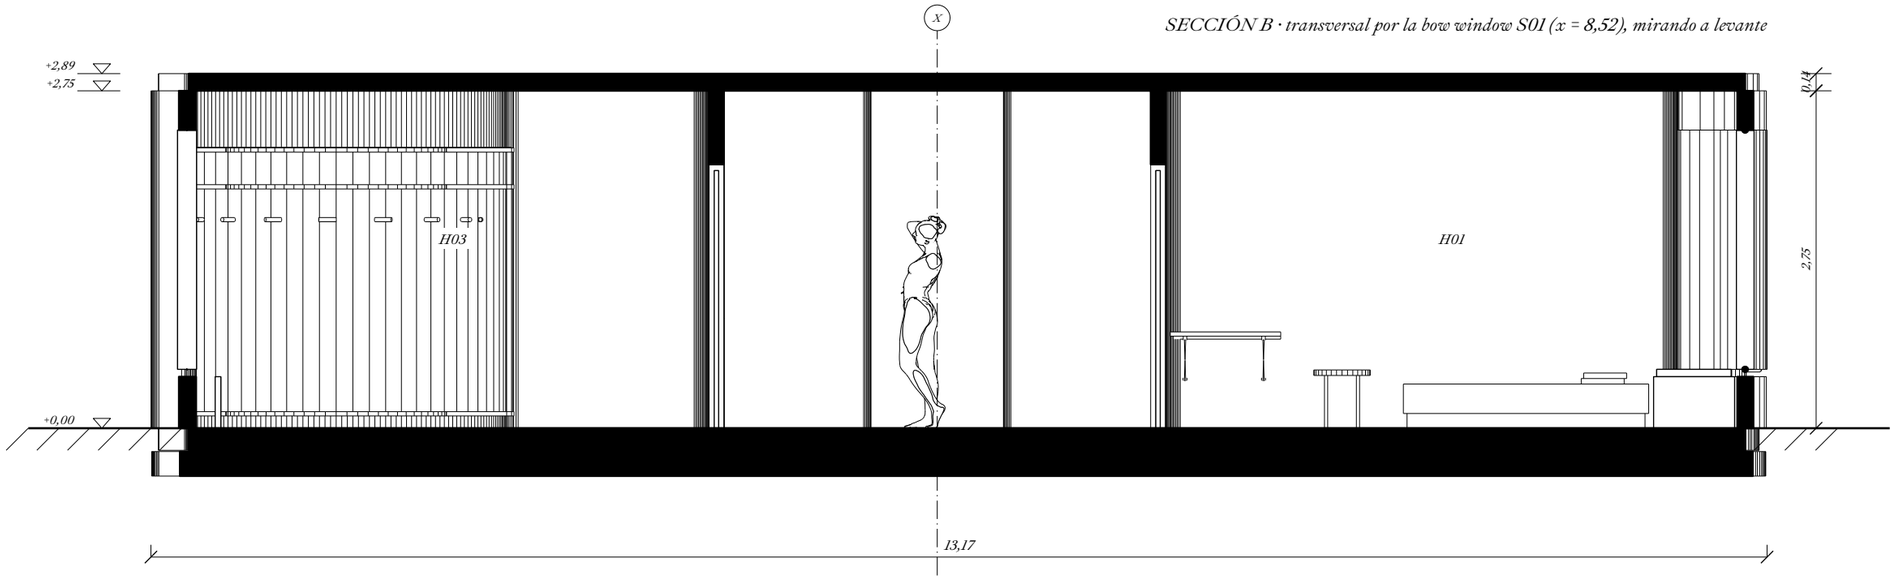


## *LECTURA DEL DIBUJO*

*Negro sólido: material seccionado*

*0,18 mm: carpinterías y equipamiento cortado*

*Proyección: 0,10 / 0,07 / 0,05 mm según fondo*

*Trazo-punto: ejes de la planta*

## *ORIGEN DE LA GEOMETRÍA*

*Corte: intersección exacta sólido / plano*

*Proyección: líneas ocultas de Rhino*

*Personas: figuras del modelo (PERSONAS.3dm)*

*Cotas en metros, medidas en el modelo*

## *CTE*

*DB SUA: altura libre de paso ≥ 2,20 m*

*Alturas leídas en la cadena de la derecha*

*Sobretecho textil retirado del dibujo*

*0 1 2 5 m*

*G3 · revisión arquitectónica medida desde Rhino · anteproyecto*

*S01*