

V02 · unidad de cuatro personas

SECCIONES · E 1:50 · corte exacto desde Rhino · cota de pavimento +0,00 m

SECCIÓN A · longitudinal por el eje X, mirando a norte

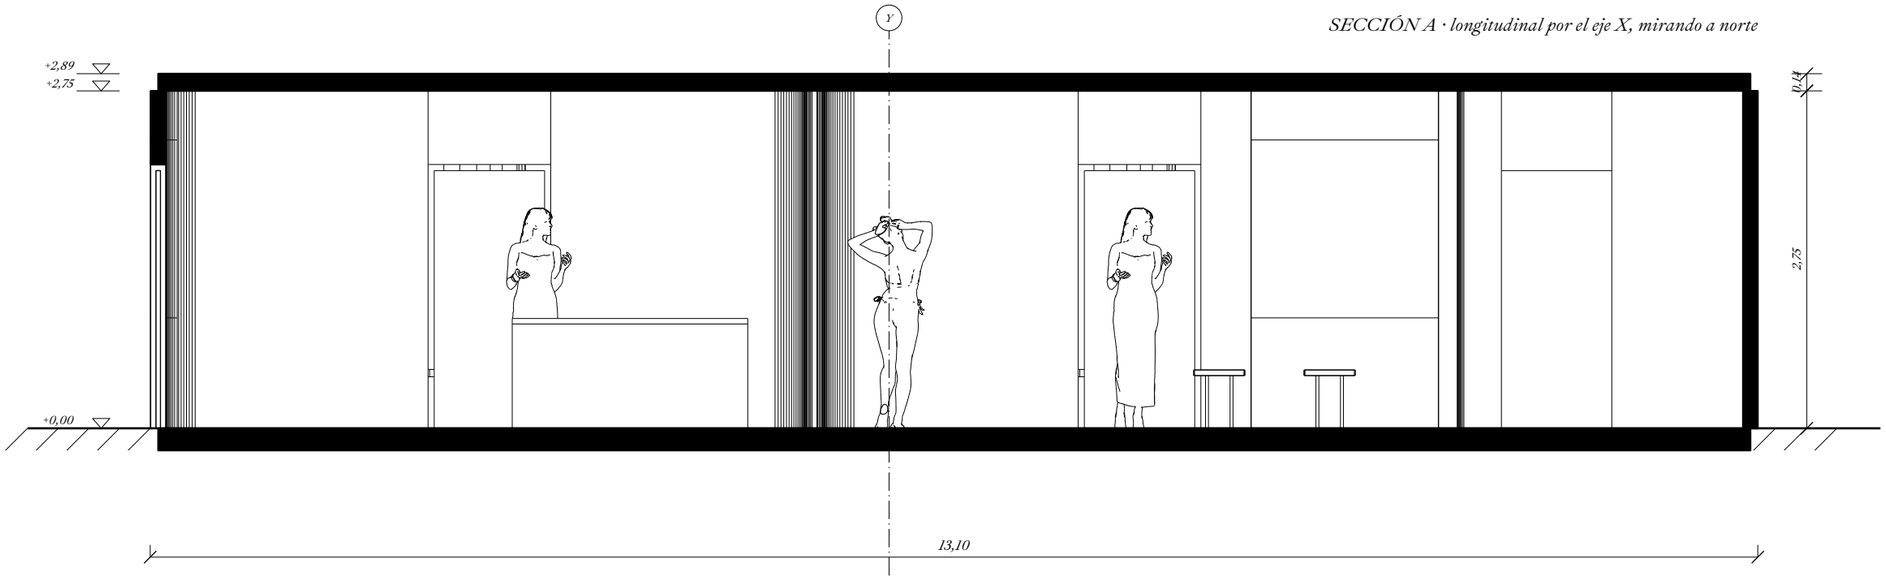

SECCIÓN B · transversal por la bow window S01 (x = 36,94), mirando a levante

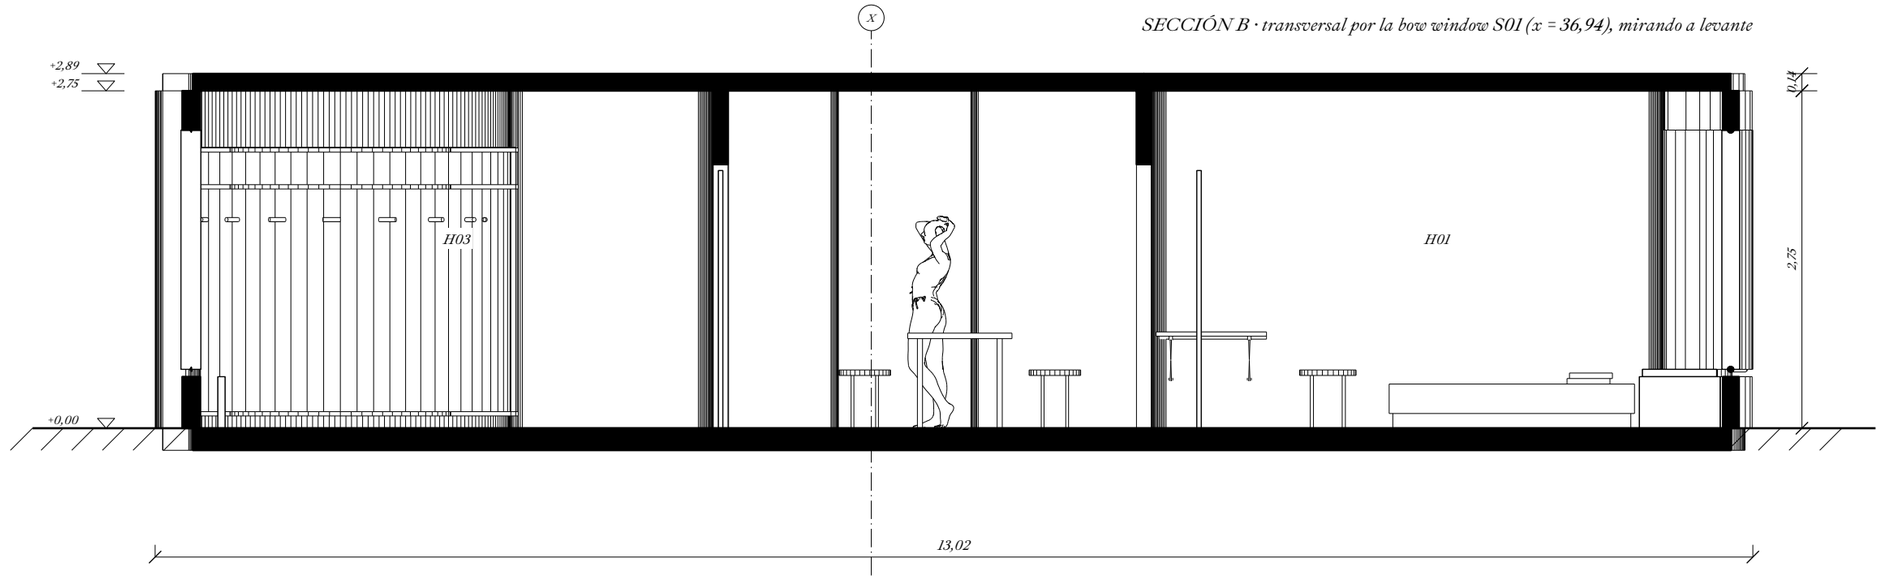

LECTURA DEL DIBUJO

Negro sólido: material seccionado

0,18 mm: carpinterías y equipamiento cortado

Proyección: 0,10 / 0,07 / 0,05 mm según fondo

Trazo-punto: ejes de la planta

ORIGEN DE LA GEOMETRÍA

Corte: intersección exacta sólido / plano

Proyección: líneas ocultas de Rhino

Personas: figuras del modelo (PERSONAS.3dm)

Cotas en metros, medidas en el modelo

CTE

DB SUA: altura libre de paso ≥ 2,20 m

Alturas leídas en la cadena de la derecha

Sobretecho textil retirado del dibujo

0 1 2 5 m

G3 · revisión arquitectónica medida desde Rhino · anteproyecto

S02