

E02 · dos unidades / ocho personas / planta elevada

SECCIONES · E 1:100 · corte exacto desde Rhino · pavimento planta baja +0,00 m / planta elevada +4,20 m


SECCIÓN A · longitudinal por el eje X, mirando a norte

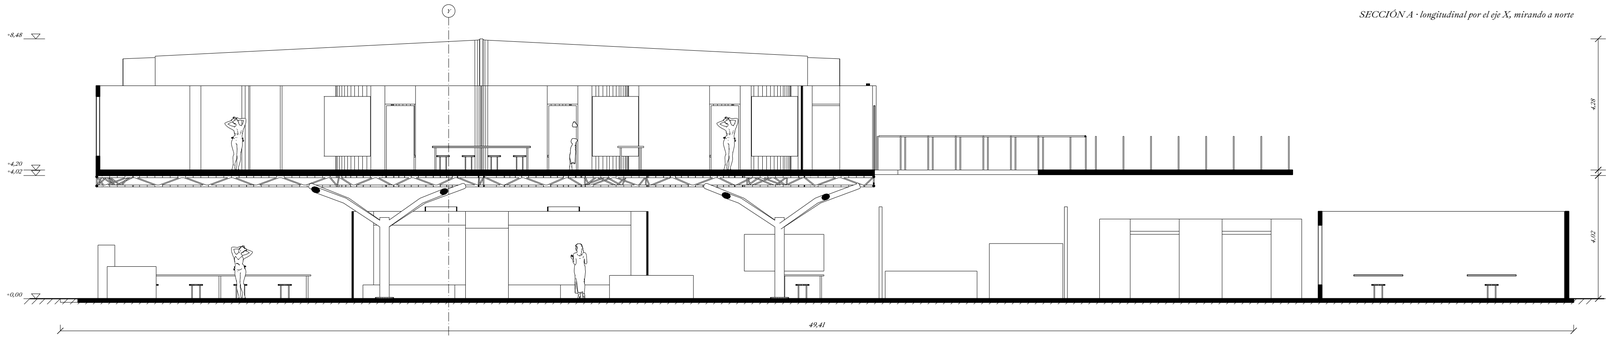


SECCIÓN B · transversal por H07 y H05, mirando a la calle

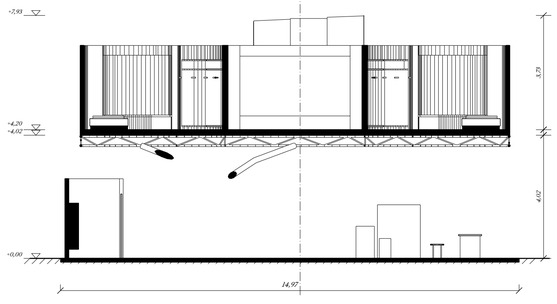

SECCIÓN C · transversal por la bow window S02 y la biblioteca (x = 28,75)

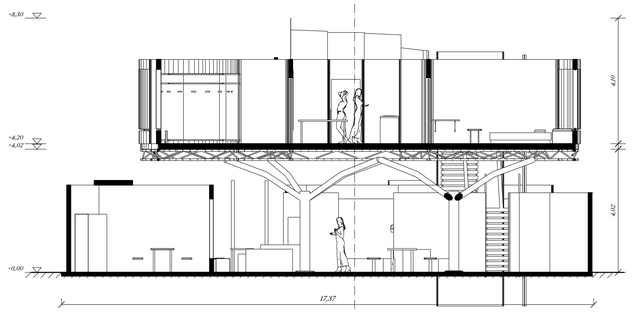

SECCIÓN D · transversal por la escalera, mirando al edificio

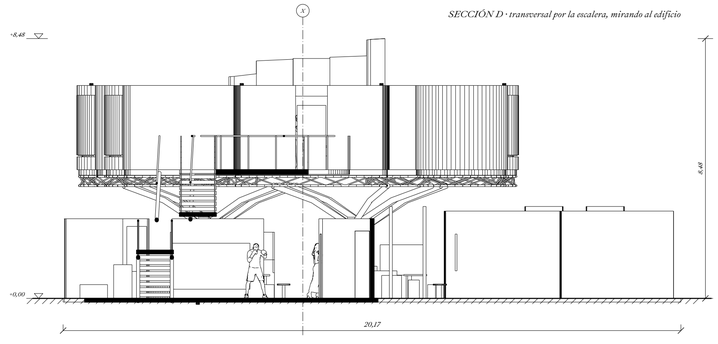

Corte negro 0,35 mm / carpintería y equipamiento cortado 0,18 mm / proyección visible 0,13 mm / ejes trazo-punto

Corte: intersección exacta de cada sólido de Rhino con el plano. Proyección: HiddenLineDrawing de Rhino de lo que queda detrás del plano.

Cotas y niveles medidos en el modelo. DB SUA: altura libre > 2,20 m en la planta baja bajo la bandeja y en las habitaciones.

0 1 2 5 m

G5 · revisión arquitectónica medida desde Rhino · anteproyecto