
E02 · dos unidades / ocho personas / planta elevada

PLANTA · E1:100 · corte +5,40 m · pavimento +4,20 m

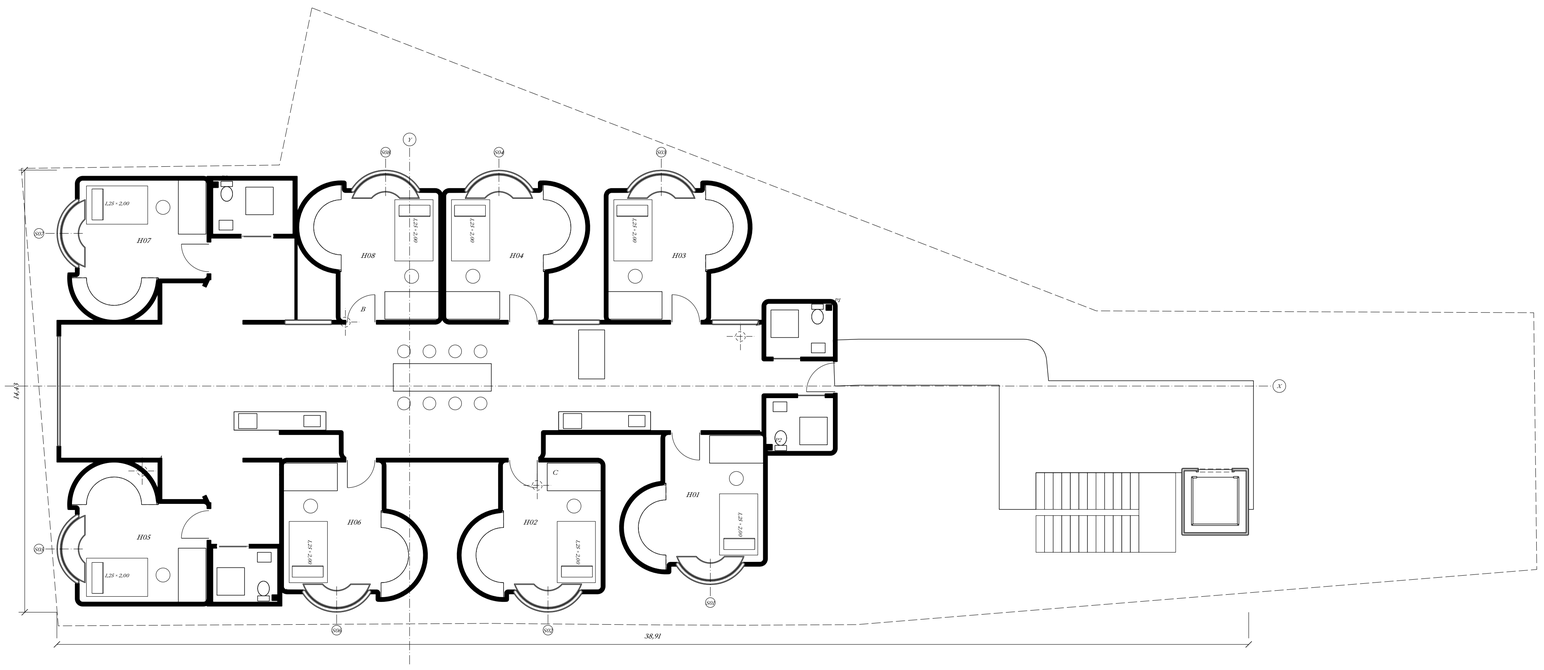

Corte negro 0,35 mm / carpintería 0,18 mm / proyección 0,13 mm / superior discontinua 0,10 mm


X/Y: referencia geométrica. Puntos A-D: apoyos medidos del modelo, sin validación estructural.

P: patinillo del borde de servicios. Sofás retirados. Escalera y ascensor conservan su posición.

0 1 2 5 m

Parcela · planta baja pública / biblioteca, estudio y trabajo compartido

PLANTA · E 1:100 · corte +1,20 m · pavimento +0,00 m

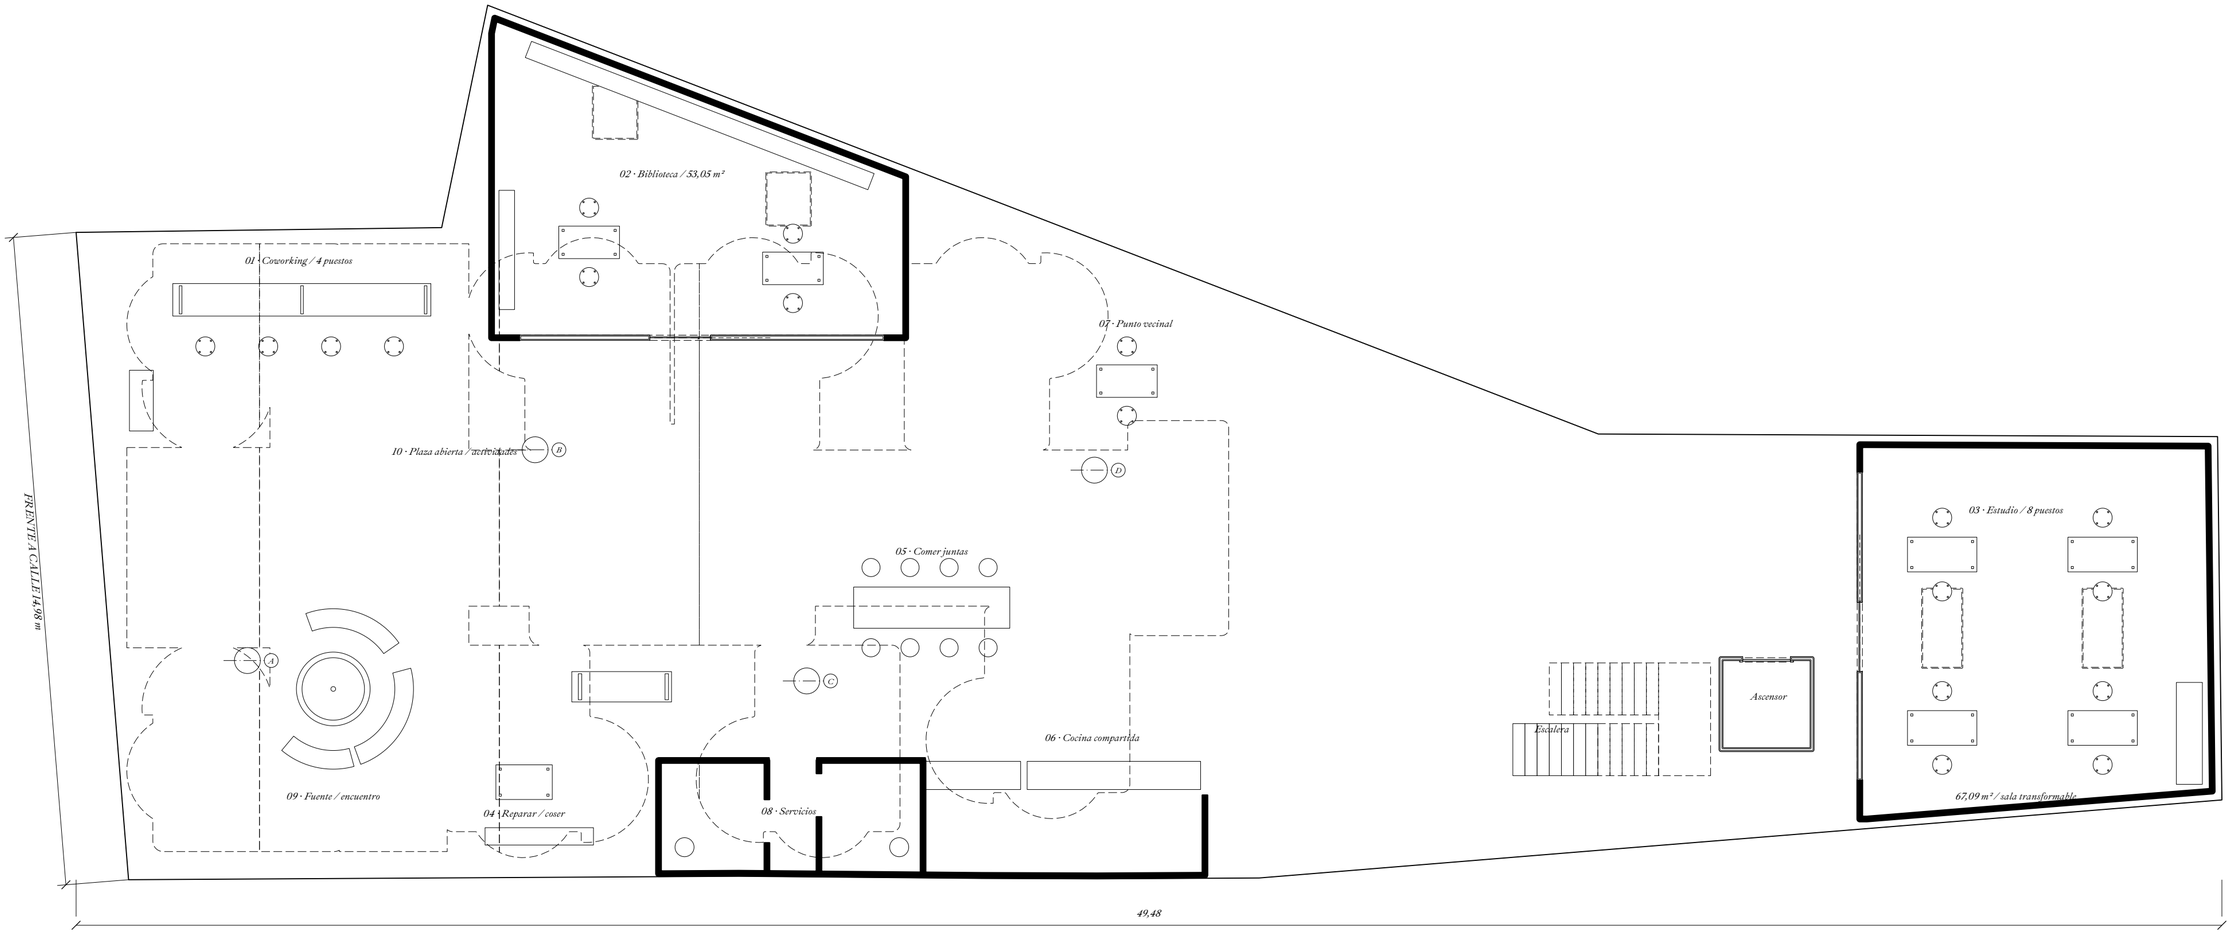

Corte negro 0,35 mm / carpintería 0,18 mm / proyección 0,13 mm / superior discontinua 0,10 mm


X/Y: referencia geométrica. Puntos A-D: apoyos medidos del modelo, sin validación estructural.

Biblioteca y estudio con luz cenital. Mesas plegables / paneles móviles. Planta baja sin vivienda privada.

0 1 2 5 m

Parcela · planta baja pública / exposición vecinal del domingo

PLANTA · E 1:100 · corte +1,20 m · pavimento +0,00 m

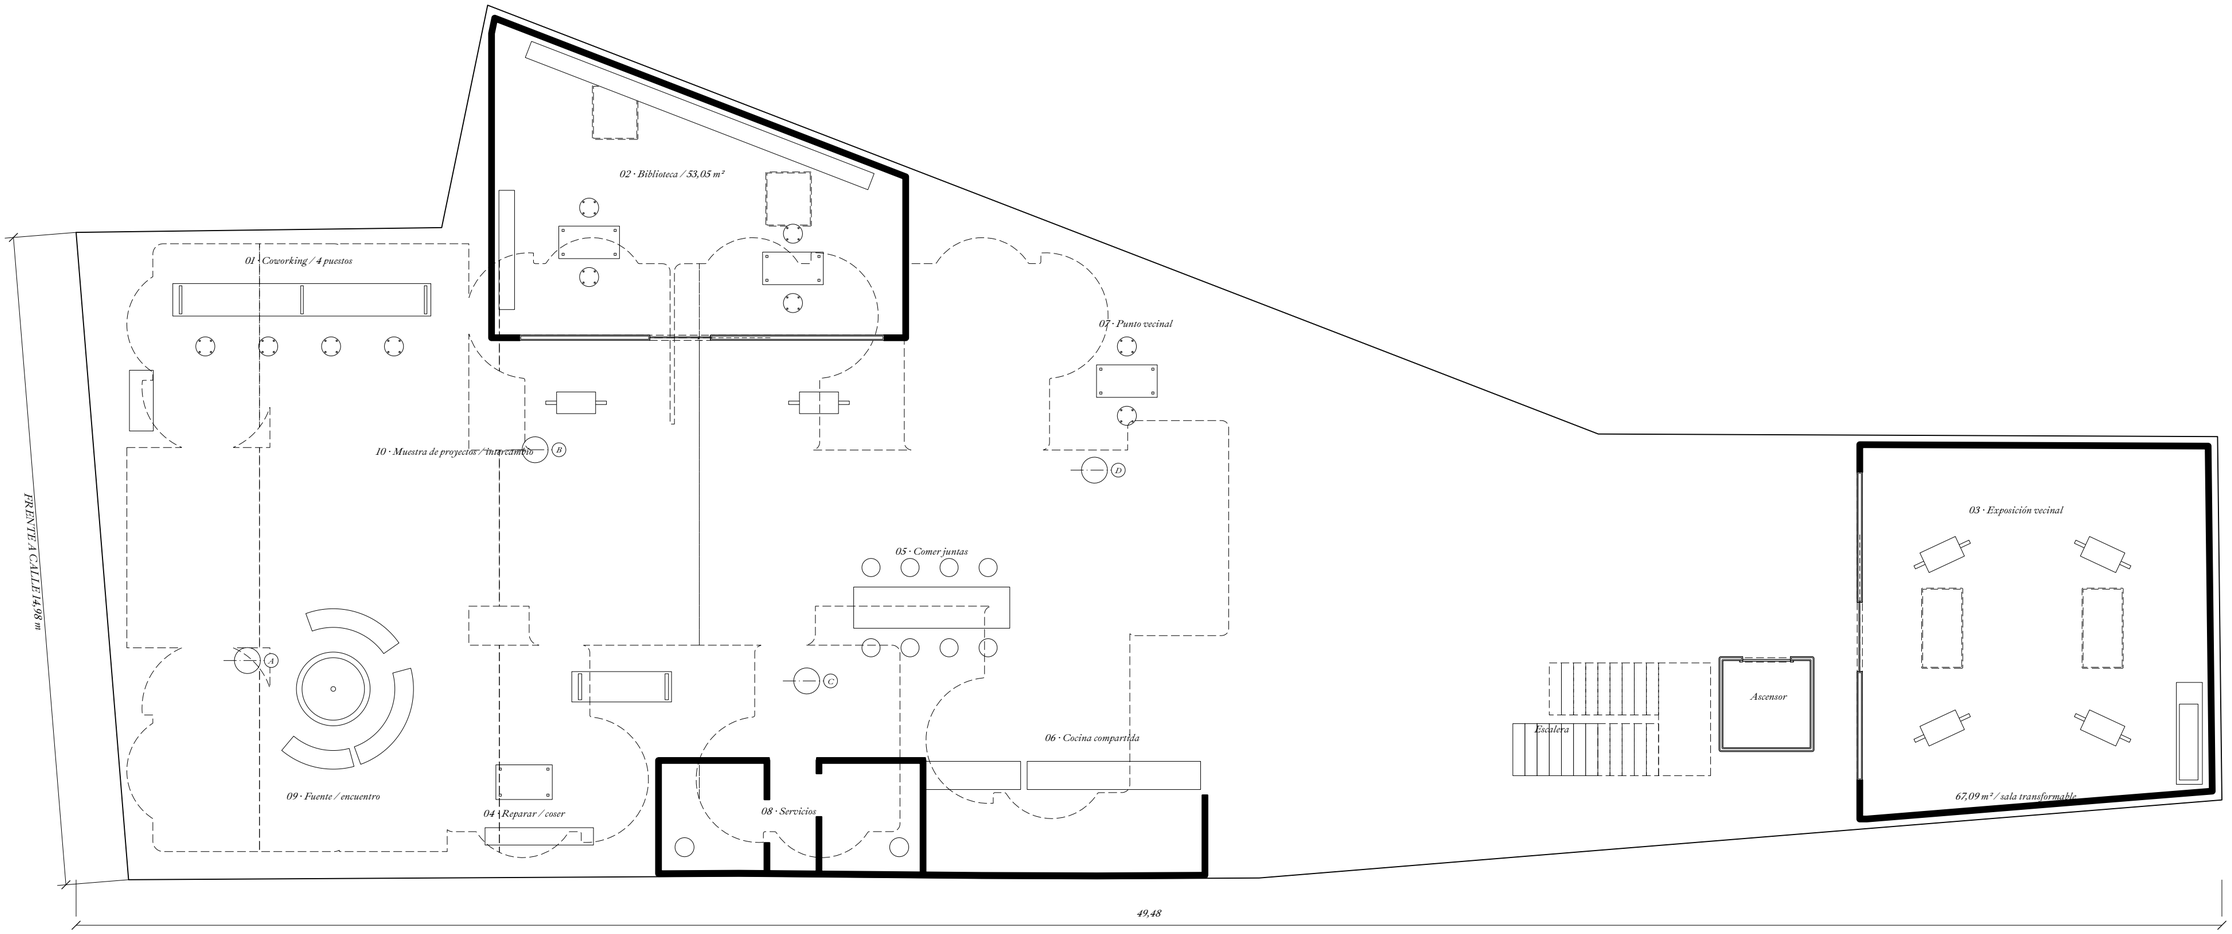

Corte negro 0,35 mm / carpintería 0,18 mm / proyección 0,13 mm / superior discontinua 0,10 mm

X/Y: referencia geométrica. Puntos A-D: apoyos medidos del modelo, sin validación estructural.

Biblioteca y estudio con luz cenital. Mesas plegables / paneles móviles. Planta baja sin vivienda privada.

0 1 2 5 m