
E02 · dos unidades / ocho personas / planta elevada

PLANTA · E 1:100 · corte +5,40 m · pavimento +4,20 m

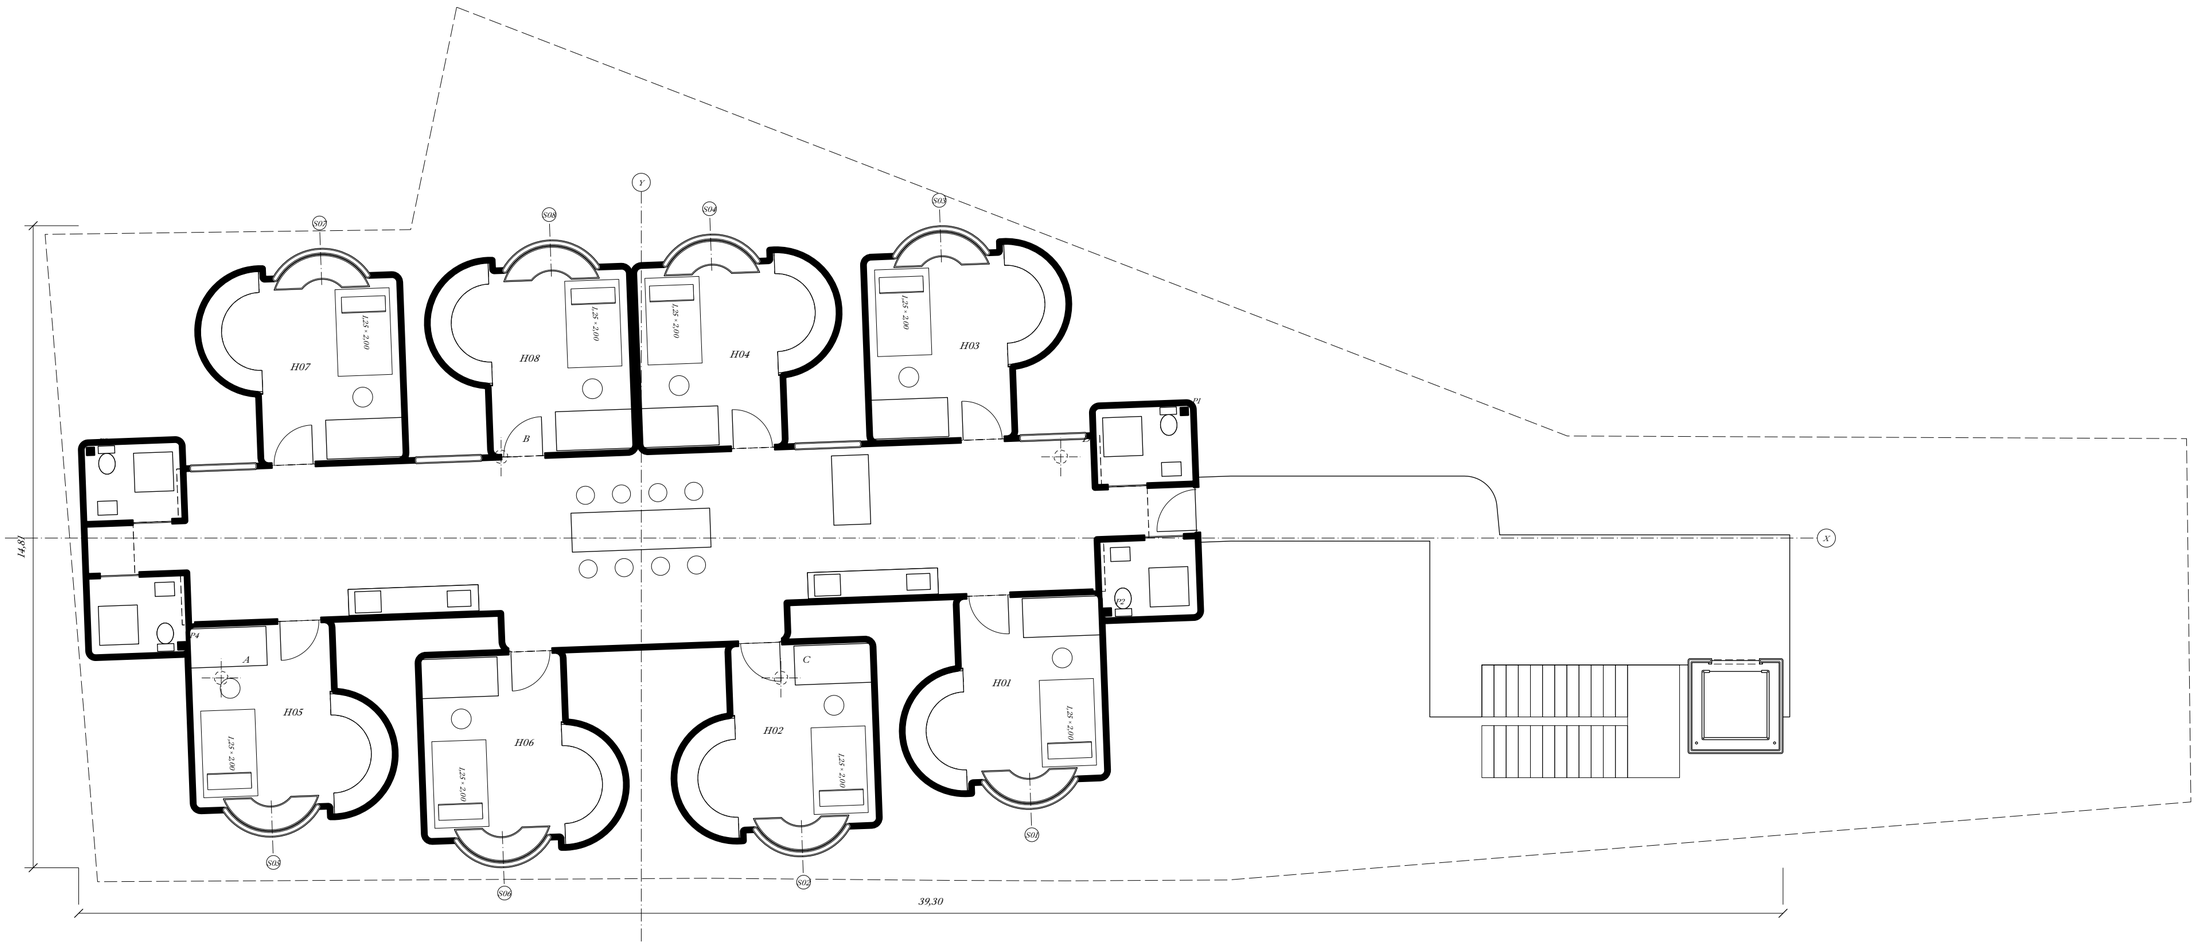

Corte negro 0,35 mm / carpintería 0,18 mm / proyección 0,13 mm / superior discontinua 0,10 mm

X/Y: referencia geométrica. Puntos A-D: apoyos medidos del modelo, sin validación estructural.

P: patinillos del borde de servicios. Sofás retirados. Escalera y ascensor conservan su posición.

0 1 2 5 m