FASE 01 · DOCUMENTO PILOTO · P.01

REFUGIO CLIMÁTICO
PUERTA DEL SOL

PLANTA GENERAL · 1:300 (A1) · norte arriba · contexto real OSM · fuente geometria_maestra.json · 07-2026

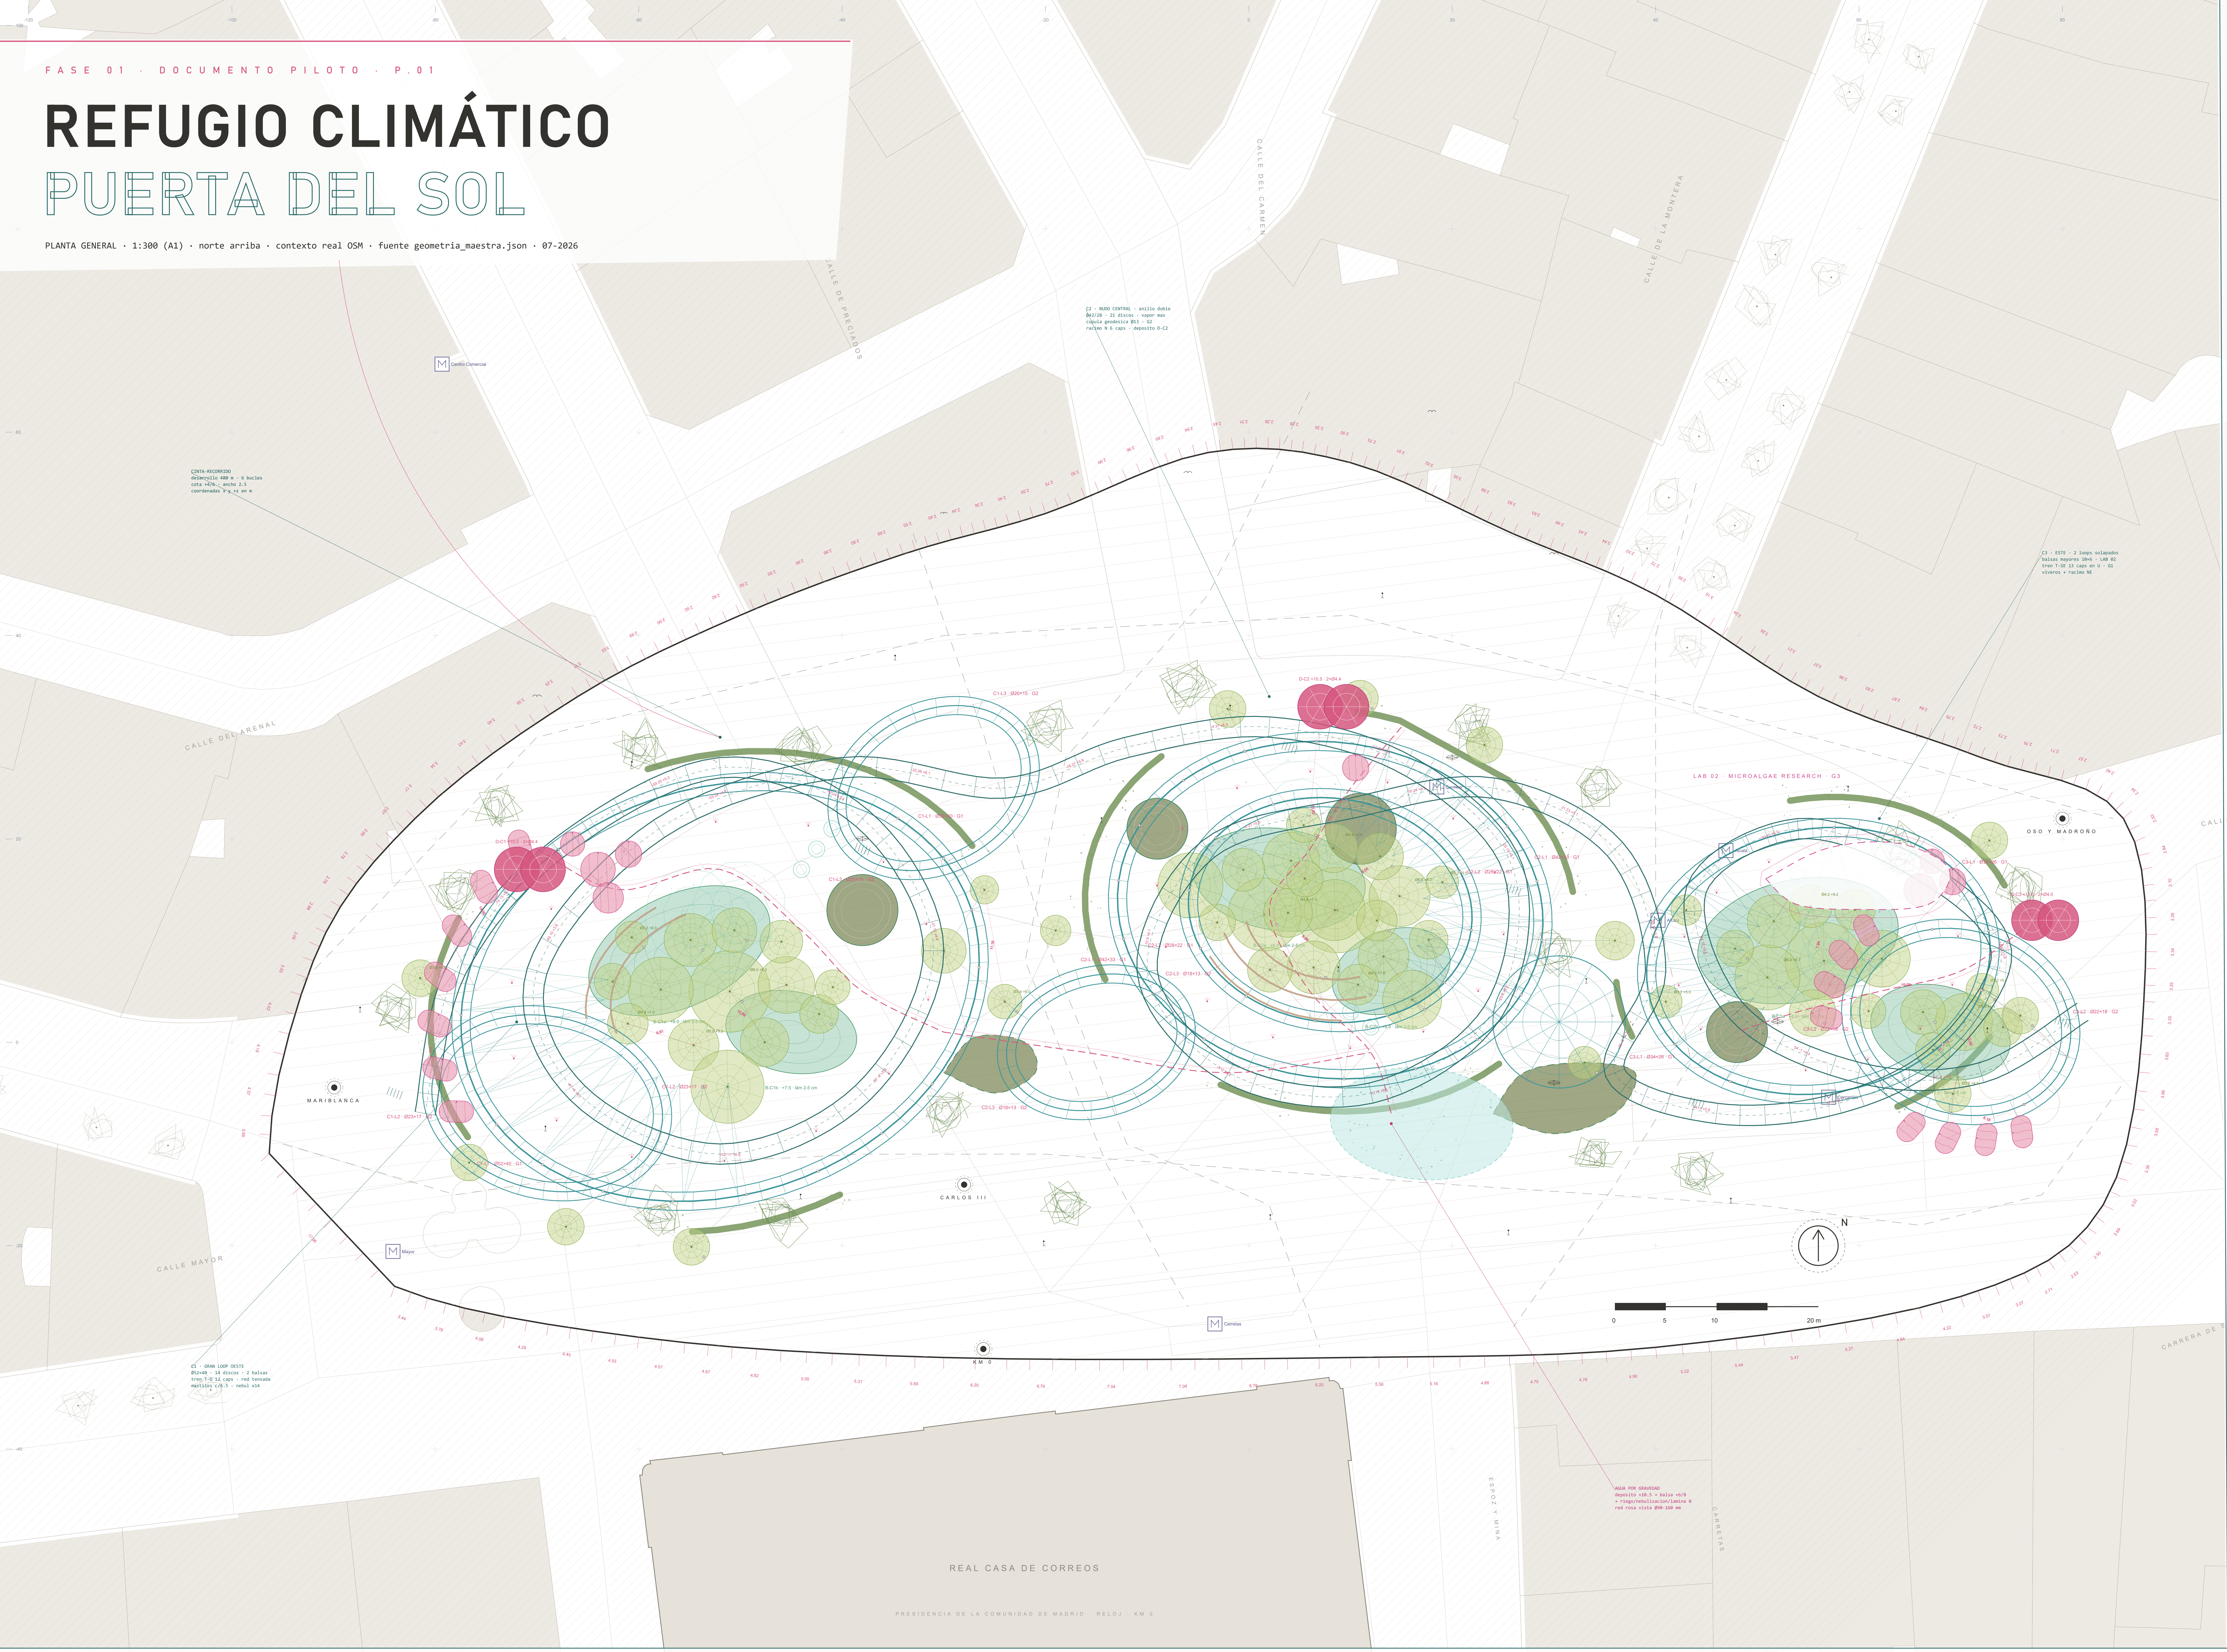
CALLE DEL CARMEN
CALLE DE LA MONTERA
CALLE DE PRECIADOS
CALLE DEL ARENAL
CALLE DE ALCALÁ
CALLE MAYOR
CARRERA DE SAN JERÓNIMO
ESPOZ Y MINA
CARRETAS
Centro Comercial
Alcalá
Mayor
Carretas
LAB 02 · MICROALGAE RESEARCH · G3
C3-L1 · Ø34×26 · G1
D-C3 +10.5 · 2×Ø4.0
Ø4.2 +9.2
OSO Y MADROÑO
MARIBLANCA
CARLOS III
KM 0
N
0
5
10
20 m
REAL CASA DE CORREOS
PRESIDENCIA DE LA COMUNIDAD DE MADRID · RELOJ · KM 0

C2 · NUDO CENTRAL · anillo doble
Ø42/28 · 21 discos · vapor max
cupula geodesica Ø13 · G2
racimo N 6 caps · deposito D-C2

CINTA-RECORRIDO
desarrollo 480 m · 6 bucles
cota +4/6 · ancho 2.5
coordenadas x y +z en m

C3 · ESTE · 2 loops solapados
balsas mayores 10×6 · LAB 02
tren T-SE 13 caps en U · G1
viveros + racimo NE

C1 · GRAN LOOP OESTE
Ø52×40 · 14 discos · 2 balsas
tren T-O 12 caps · red tensada
mastiles c/6.5 · nebul x14

AGUA POR GRAVEDAD
deposito +10.5 → balsa +6/8
→ riego/nebulizacion/lamina 0
red rosa vista Ø90-160 mm

LEYENDA

●	**loop estructural**	haz de 3 anillos · traviesas c/2 m
●	**red tensada**	malla de cables con nudos
●	**cinta-recorrido**	doble carril +4/6 · coordenadas x y +z
●	**disco-canopy**	malla radial Ø3–8 · lám. microalgas
●	**balsa elevada**	oleaje · cota +6/8
●	**estanque de cultivo**	en suelo · murete 45 cm
●	**lámina jugable**	+ vapor de nebulización
●	**cápsula neumática**	gajos y válvula · suelo/media
●	**depósito +10.5**	radios = zunchos TPU
●	**red hidráulica vista**	boquillas en abanico
●	**micro-cotas**	distancias reales en metros
●	**vegetación**	garabato = copa · puntos = matas
●	**banco-jardinera**	madera en arco
●	**mástil ramificado**	+ abanico de cables
●	**Metro / Cercanías**	bocas conservadas
●	**monumento**	triple diana · figuras y fauna

CERTEZA

───	G1 — confirmado
───	G2 — muy probable
– –	G3 — inferido
· · · ·	G4 — reserva F02

ESTRATOS

+10/12	depósitos · red alta
+5/10	discos · balsas · loops
+4/6	cinta-recorrido
+2/4	cápsulas media · riego
±0	suelo público continuo

SECCIÓN TIPO

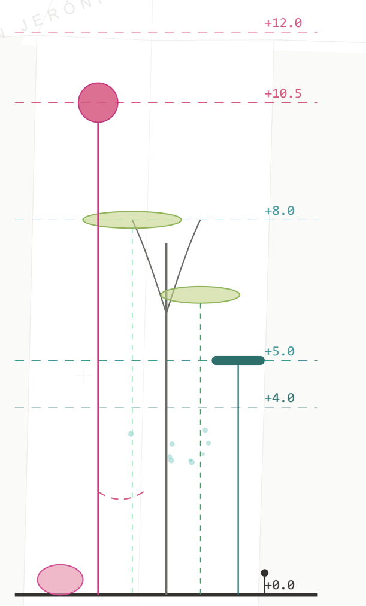
+12.0
+10.5
+8.0
+5.0
+4.0
+0.0

P.01
IRAXXXDIOS

PLAZA 10.957 M² · INTERVENCIÓN 163×51 M · DOSEL 1.890 M² · 67 DISCOS · 6 BALSAS · 5 ESTANQUES · 8 LOOPS + CÚPULA · CINTA 480 M / 6 BUCLES · 38 CÁPSULAS · 13 DEPÓSITOS · 42 BOQUILLAS · 98 MÁSTILES · 39+20 ÁRBOLES · BANDA CORREOS 15 M · ALTURA MÁX 12 M · AGUA POR GRAVEDAD

REFUGIO CLIMÁTICO PUERTA DEL SOL · FASE 01 · 07-2026 · iraxxxdios · contexto OpenStreetMap (ODbL) · toda cifra dibujada procede de geometria_maestra.json (1 u = 1 m)