

CLEAR_HEIGHT_MAP · altura libre sobre el suelo pisable

Distancia vertical desde el pavimento hasta la cara inferior del primer elemento (dosel, loops, estructura, cables, depósitos, vegetación, cinta). Sólo celdas pisables.

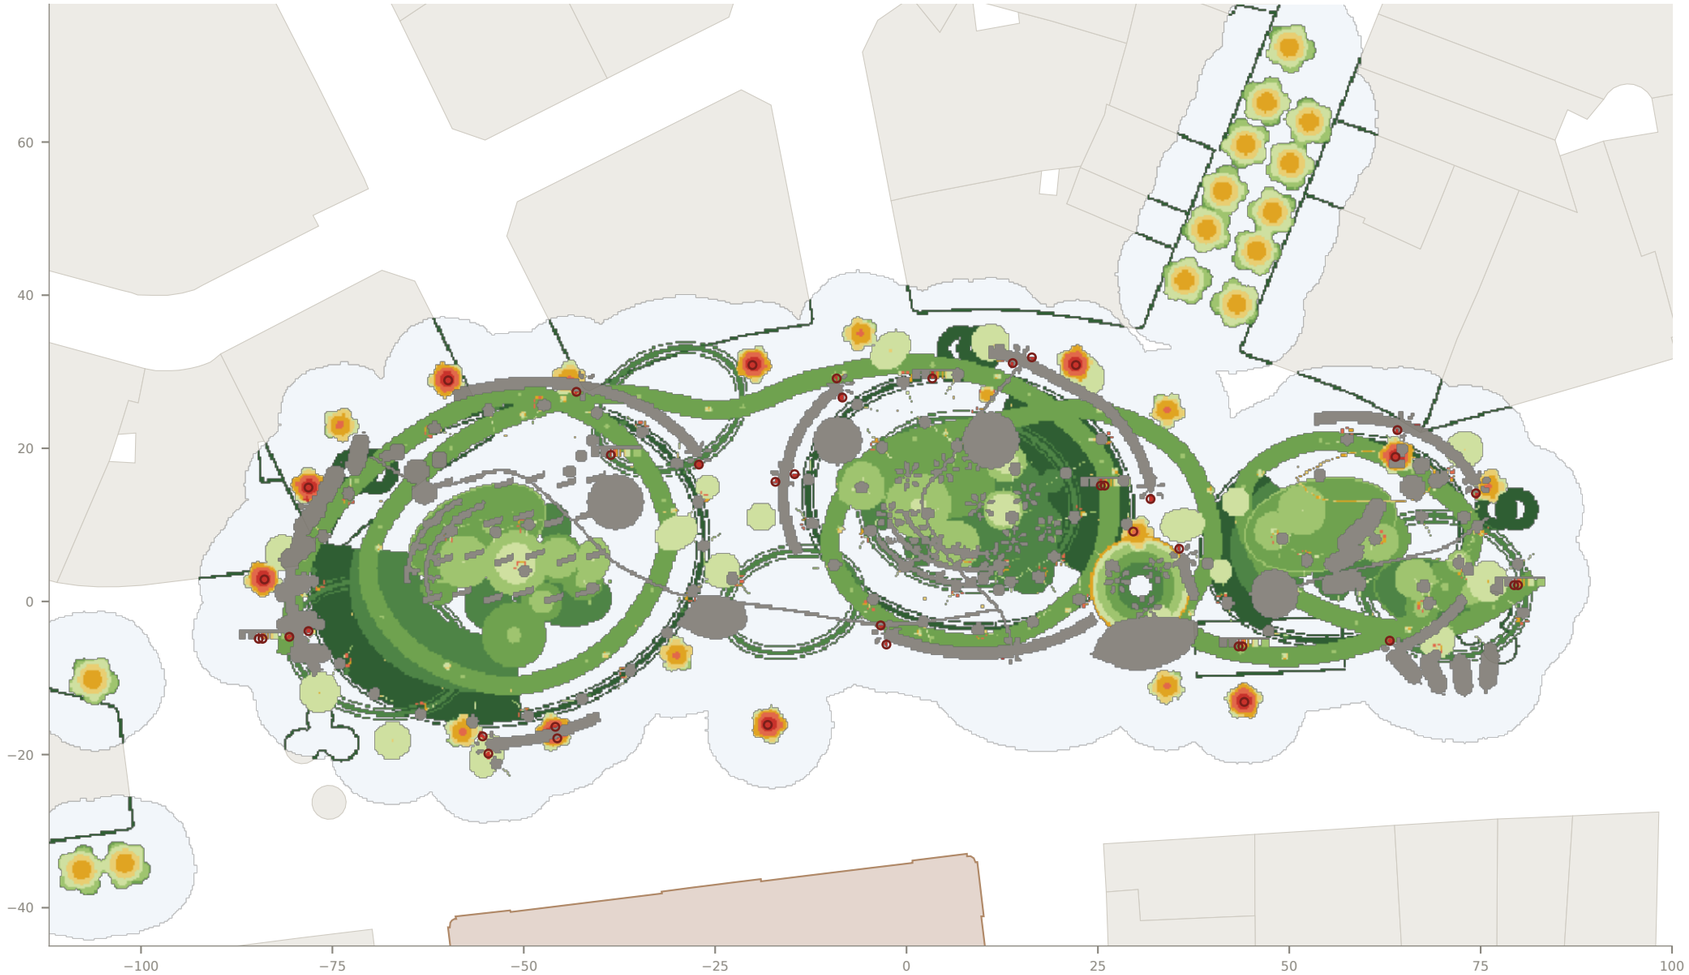

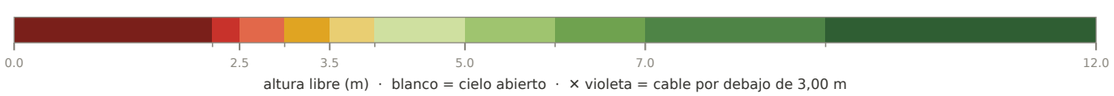

FIRME h	x,y	m²	elemento
2.31	43,-6	0.25	STEP
2.31	-85,-5	0.25	STEP
2.31	79,2	0.25	STEP
2.31	25,15	0.25	STEP
2.31	-39,19	0.25	STEP
2.31	3,29	0.25	STEP
2.70	44,-6	0.25	STEP
2.70	-84,-5	0.25	STEP
2.70	80,2	0.25	STEP
2.70	26,15	0.25	STEP
2.70	-38,19	0.25	STEP
2.70	4,29	0.25	STEP

VEG. h	x,y	m²	bloque
2.21	-84,3	3.25	VEG2_ARBOL_A
2.21	-18,-16	3.25	VEG2_ARBOL_A
2.21	64,19	1.94	VEG2_ARBOL_A
2.21	44,-13	3.25	VEG2_ARBOL_A
2.21	22,31	3.25	VEG2_ARBOL_A
2.21	-20,31	3.25	VEG2_ARBOL_A
2.21	-60,29	3.25	VEG2_ARBOL_A
2.21	-78,15	3.25	VEG2_ARBOL_A
2.22	-3,-3	0.31	VEG2_TROPICAL


Suelo pisable en el ámbito: 9901 m². Bajo algún elemento: 3825 m² (39 %). Mediana del gálibo: 6.00 m.

HALLAZGO CENTRAL DEL CAPÍTULO. La regla 7 del HEIGHT_SYSTEM exige 3,00 m «bajo cualquier elemento FIRME sobre paso». Separando las dos cosas: bajo elemento firme el gálibo sólo baja de 3,00 m en 3.2 m² de los 3825 m² cubiertos (0.08 %), con mínimo 2.31 m, y todo ello ocurre bajo las zancas de las escaleras de la cinta. El mínimo absoluto de 2.21 m NO es estructura: son copas de arbolado E02 (VEG2_ARBOL_A), 33.4 m² por debajo de 2,50 m — una cuestión de poda de formación, no de gálibo estructural. El dosel, los loops, la cinta y las cápsulas cumplen.


CLEAR_HEIGHT_MAP · secciones automáticas en los mínimos de gálibo

Corte real del modelo con la persona de referencia de 1,70 m. Arriba: mínimos bajo elemento firme. Abajo: mínimos bajo copa de arbolado.


corte y = -5.9 · mínimo 2.31 m en x = 43.4 · STEP

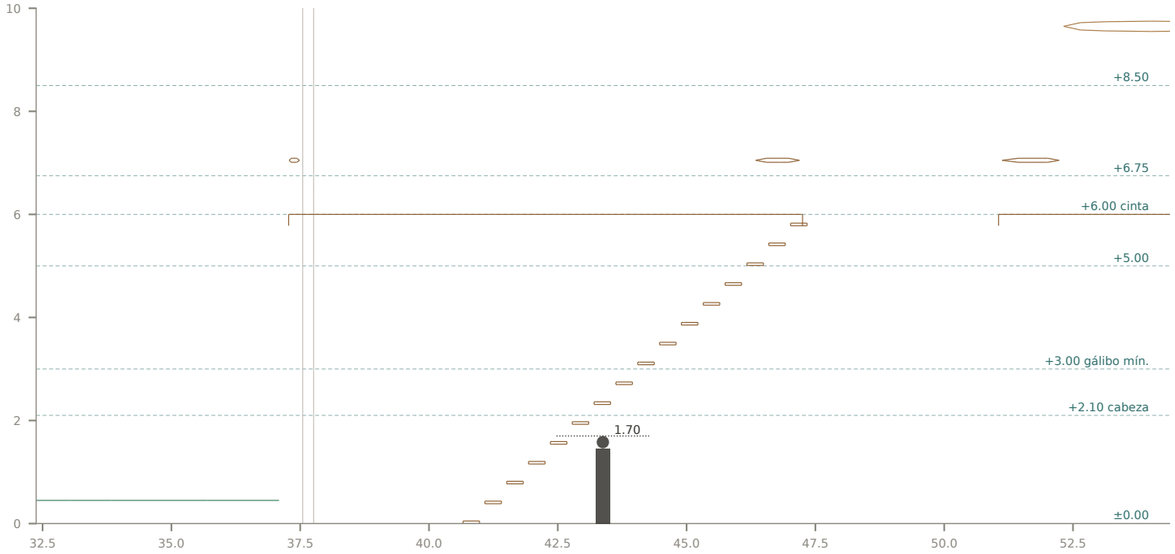

corte y = -4.9 · mínimo 2.31 m en x = -84.6 · STEP

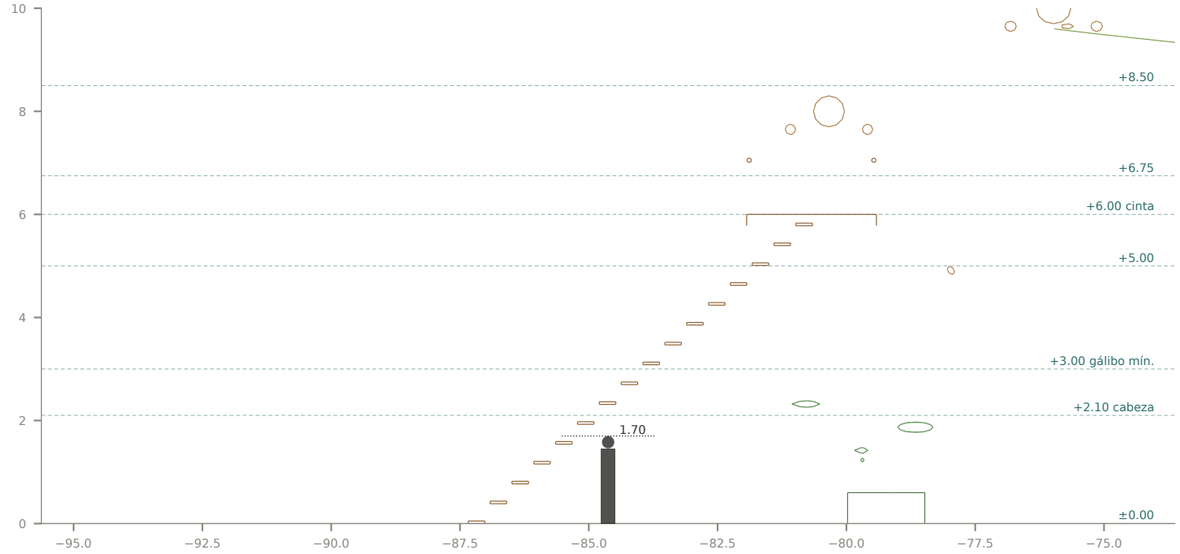

corte y = 2.9 · mínimo 2.21 m en x = -83.9 · VEG2_ARBOL_A

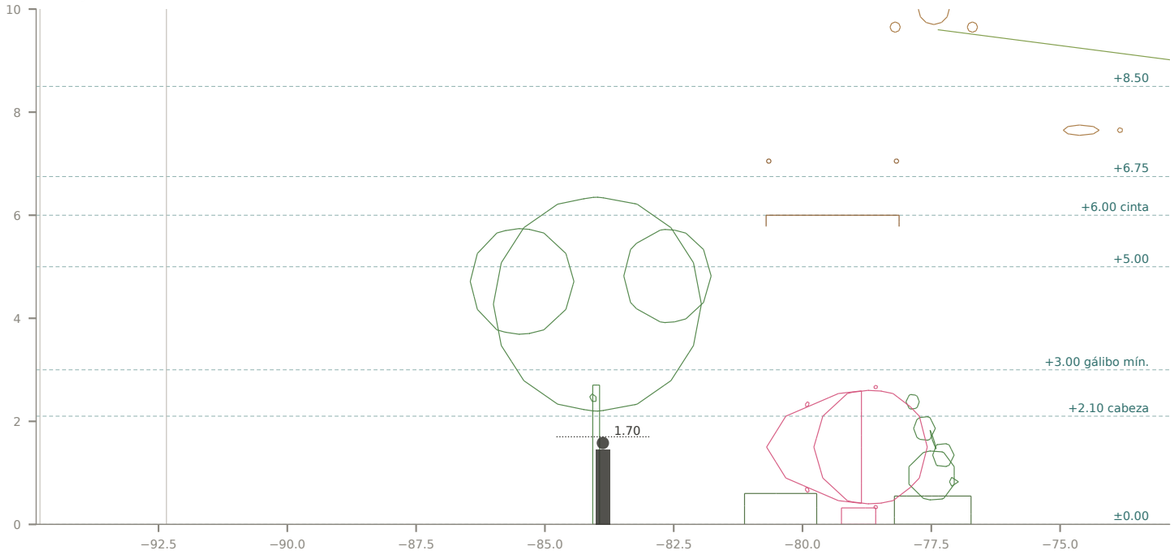

corte y = -16.1 · mínimo 2.21 m en x = -18.1 · VEG2_ARBOL_A

