

CLEAR_HEIGHT_MAP · altura libre sobre el suelo pisable

Distancia vertical desde el pavimento hasta la cara inferior del primer elemento (dosel, loops, estructura, cables, depósitos, vegetación, cinta). Sólo celdas pisables.

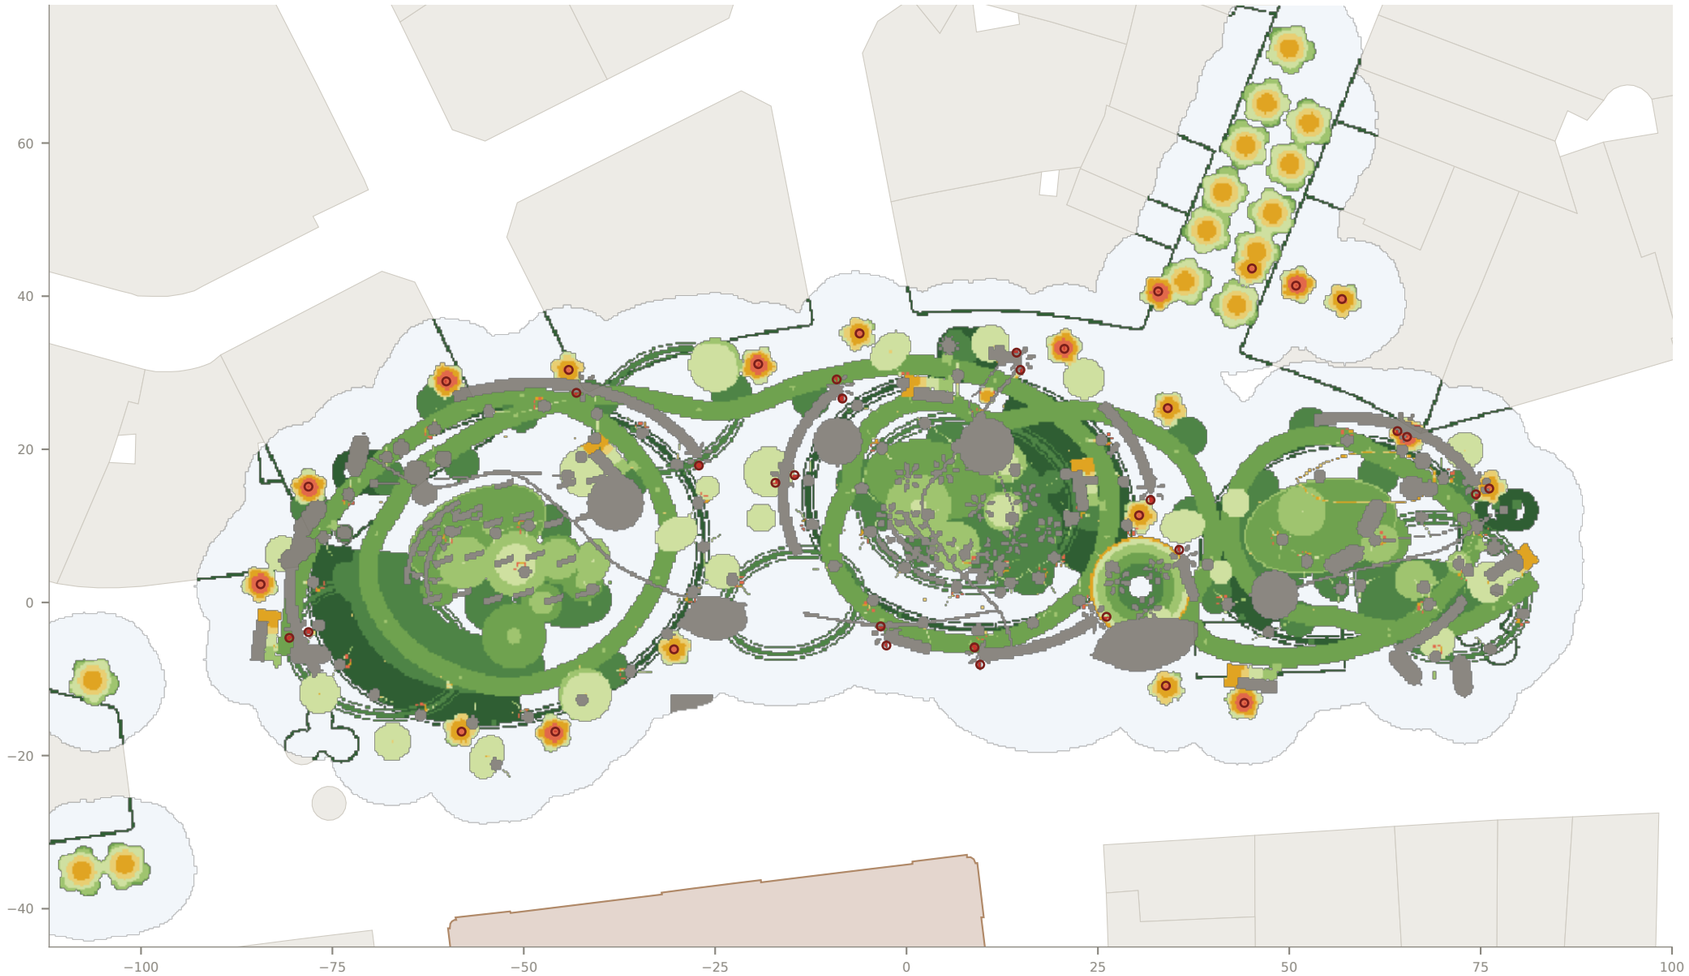

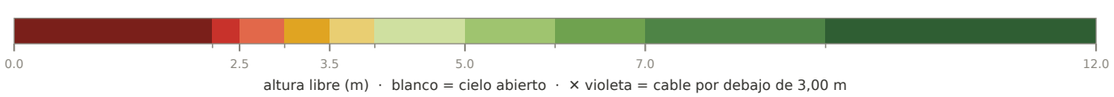

altura libre (m) · blanco = cielo abierto · × violeta = cable por debajo de 3,00 m

FIRME h	x,y	m²	elemento

VEG. h	x,y	m²	bloque
2.22	-3,-3	0.31	VEG2_TROPICAL
2.22	-81,-5	0.44	VEG2_TROPICAL
2.22	-27,18	0.44	VEG2_TROPICAL
2.22	74,14	0.31	VEG2_TROPICAL
2.23	-3,-6	0.38	VEG2_TROPICAL
2.23	-43,27	0.31	VEG2_TROPICAL
2.23	-9,29	0.31	VEG2_TROPICAL
2.23	10,-8	0.44	VEG2_TROPICAL
2.23	-78,-4	0.38	VEG2_TROPICAL

Suelo pisable en el ámbito: 9994 m². Bajo algún elemento: 4230 m² (42 %). Mediana del gálibo: 6.00 m.


HALLAZGO CENTRAL DEL CAPÍTULO. La regla 7 del HEIGHT_SYSTEM exige 3,00 m «bajo cualquier elemento FIRME sobre paso». Separando las dos cosas: bajo elemento firme el gálibo sólo baja de 3,00 m en 0.2 m² de los 4230 m² cubiertos (0.01 %), con mínimo 2.90 m, y todo ello ocurre bajo las zancas de las escaleras de la cinta. El mínimo absoluto de 2.22 m NO es estructura: son copas de arbolado E02 (VEG2_ARBOL_A), 8.3 m² por debajo de 2,50 m — una cuestión de poda de formación, no de gálibo estructural. El dosel, los loops, la cinta y las cápsulas cumplen.

FASE 03B.5 · AUDITORÍA GEOMÉTRICA Y DE VIABILIDAD

CLEAR_HEIGHT_MAP · secciones automáticas en los mínimos de gálibo

Corte real del modelo con la persona de referencia de 1,70 m. Arriba: mínimos bajo elemento firme. Abajo: mínimos bajo copa de arbolado.

corte y = -3.1 · mínimo 2.22 m en x = -3.4 · VEG2_TROPICAL

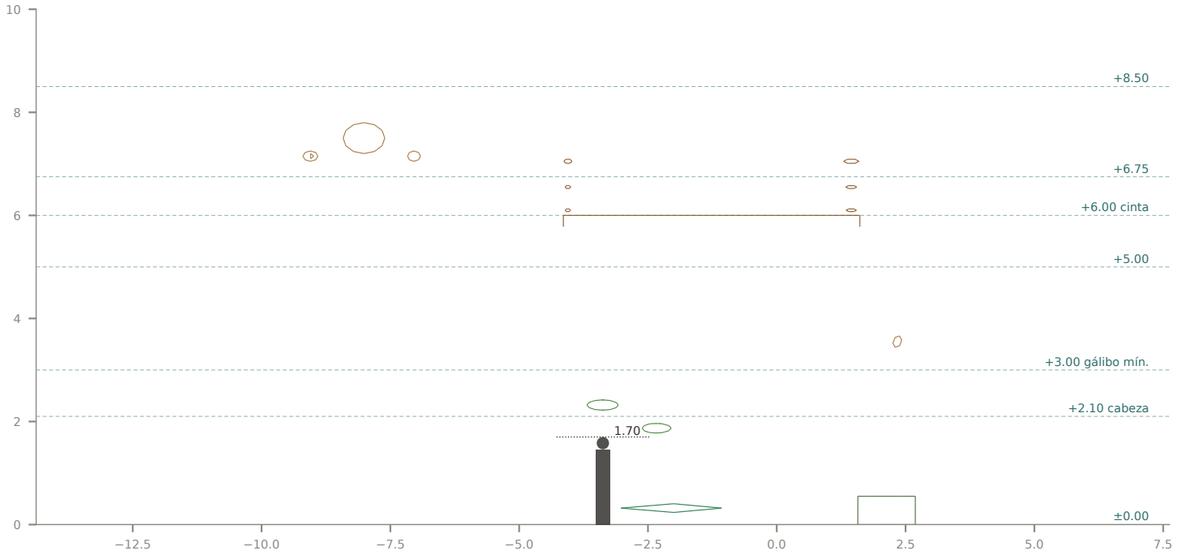

corte y = -4.6 · mínimo 2.22 m en x = -80.6 · VEG2_TROPICAL

