

PATH_WIDTH_MAP · anchura libre de la red peatonal

Anchura libre local = 2 × distancia al obstáculo más próximo en la banda de cuerpo 0,05–2,10 m. Rejilla 0,25 m. Clasificación provisional del propio análisis (sin norma aplicada todavía).

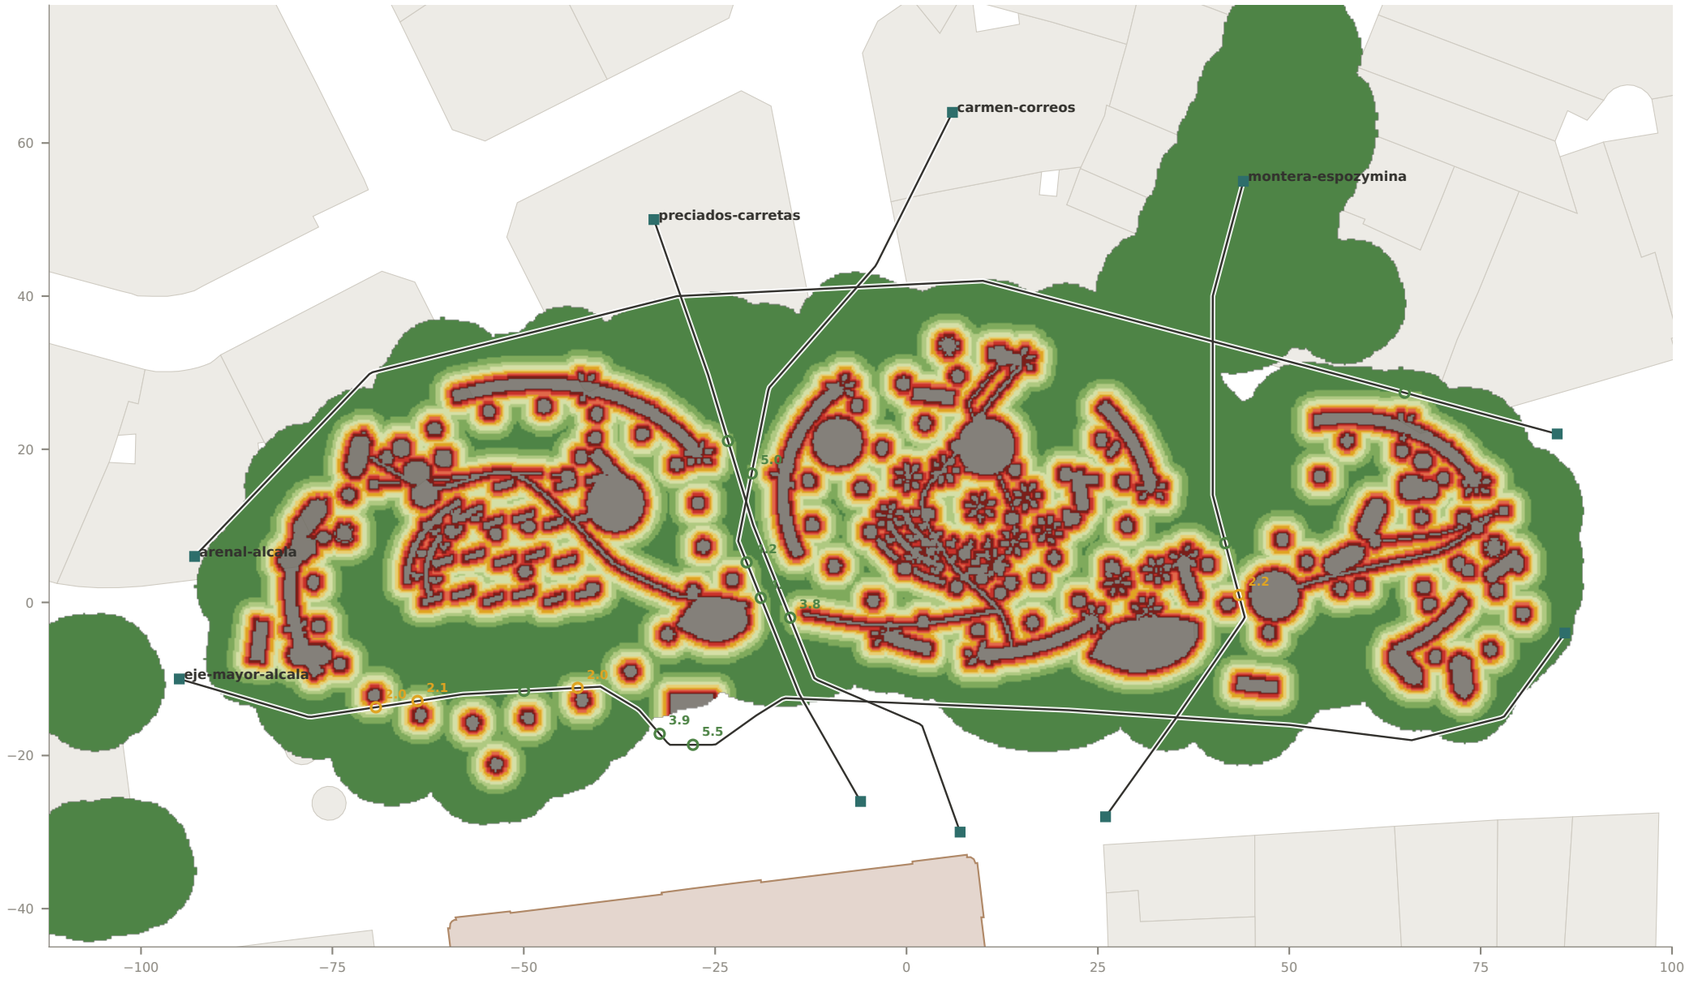

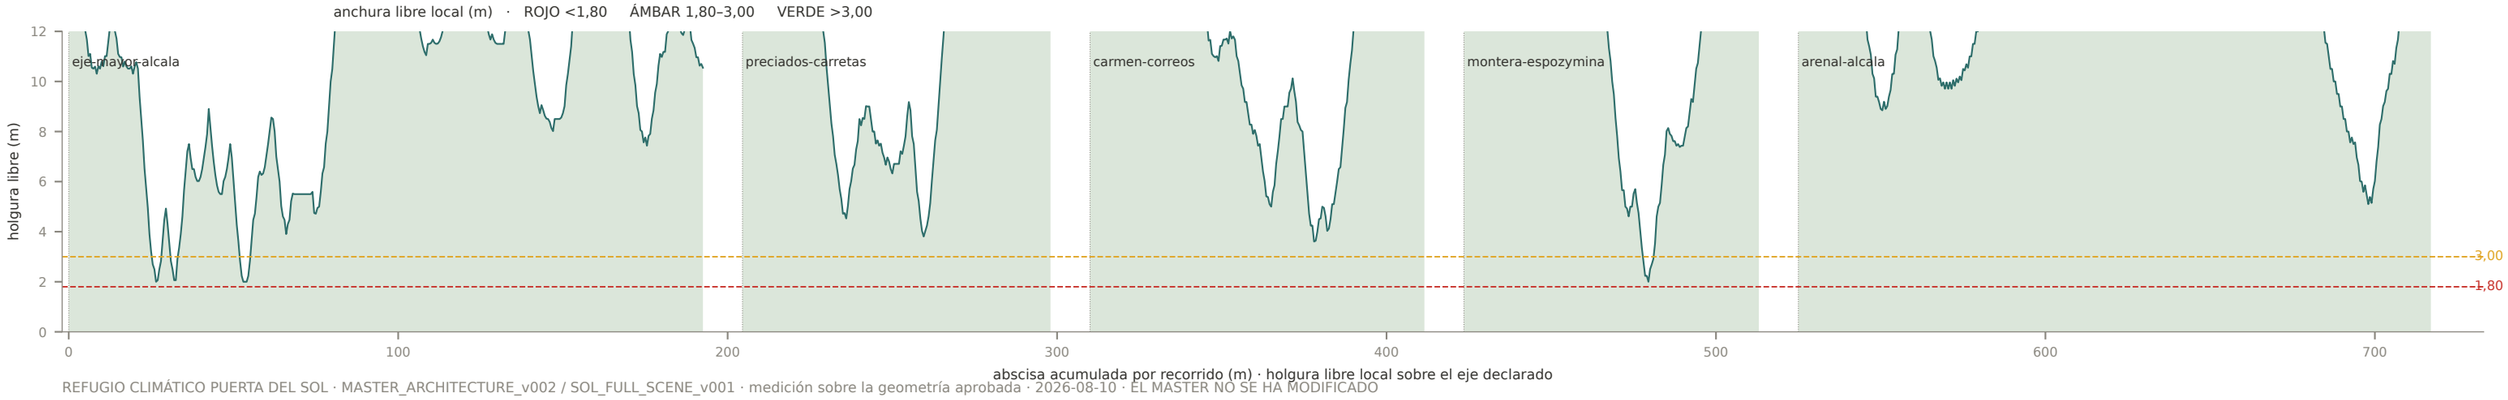



recorrido	L(m)	mín	p05	p50	holg.mín
eje-mayor-alcala	192	12.25	29.00	38.0	2.00
preciados-carretas	94	7.50	11.50	38.5	3.81
carmen-correos	102	7.50	10.36	42.6	3.61
montera-espozymina	90	2.00	7.74	48.5	2.00
arenal-alcala	192	32.50	34.00	42.2	5.10

ANCHURA TRANSVERSAL medida por rayos perpendiculares al eje declarado;
«holg. mín» = anchura libre local mínima sobre el eje.

umbral	comp>20m²	mayor	% suelo
0.90 m	2	9205 m²	93 %
1.20 m	2	8735 m²	88 %
1.50 m	2	8580 m²	87 %
1.80 m	3	8270 m²	84 %
2.00 m	4	8091 m²	82 %
2.50 m	2	7722 m²	78 %
3.00 m	1	7233 m²	73 %
4.00 m	2	6502 m²	66 %

FRAGMENTACIÓN: número de componentes conectadas del suelo libre al exigir esa anchura mínima continua.

cuello de botella entre los 10 accesos	peor par	mejor par
libre (puede rodear por la calle)	10.75 m	40.00 m
obligando a cruzar el ámbito	10.75 m	21.00 m

Maximin sobre la rejilla: anchura del punto más estrecho del mejor camino posible entre cada par de accesos. La red está holgadamente conectada; el problema no es la capacidad global sino los puntos locales listados en la página 2.

PATH_WIDTH_MAP · estrechamientos sobre los ejes, pasos estrangulados y bolsas

sobre el eje declarado	s(m)	x,y	holgura
eje-mayor-alcal	26	-69,-14	2.00
eje-mayor-alcal	53	-43,-11	2.00
eje-mayor-alcal	32	-64,-13	2.06
montera-espozym	55	43,1	2.24
preciados-carre	55	-15,-2	3.81
eje-mayor-alcal	66	-32,-17	3.91
carmen-correos	72	-19,1	4.03
carmen-correos	67	-21,5	4.24
preciados-carre	30	-23,21	4.72
carmen-correos	55	-20,17	5.00
eje-mayor-alcal	46	-50,-12	5.50
eje-mayor-alcal	71	-28,-19	5.50
arenal-alcala	172	65,27	5.59
montera-espozym	48	42,8	5.66

pasos estrangulados	x,y <1,20 m	entre familias
0.50	48,-2	PLANTER
0.50	67,1	PLANTER
0.50	-50,5	PLANTER+VEGETATION
0.50	6,7	PLANTER+VEGETATION+WATER
0.50	19,8	PLANTER+VEGETATION
0.50	21,10	FURNITURE+VEGETATION
0.50	11,11	PLANTER+VEGETATION
0.50	67,17	PLANTER+PODS
0.50	-28,18	PLANTER+VEGETATION
0.50	-41,21	STRUCTURE+WATER



10 pasos por debajo de 1,20 m de holgura en todo el ámbito (deduplicados a 2 m).

CRITERIO: se mide la geometría, no la norma. El umbral 1,80 m se usa como referencia de trabajo (cruce de dos personas / silla + peatón) y 3,00 m como umbral de holgura para un espacio público de esta intensidad de uso. La determinación normativa aplicable (Orden VIV/561/2010 y ordenanza municipal) queda pendiente de la fase de verificación normativa: aquí sólo se localiza y cuantifica.