
PATH_WIDTH_MAP · anchura libre de la red peatonal

Anchura libre local = 2 × distancia al obstáculo más próximo en la banda de cuerpo 0,05–2,10 m. Rejilla 0,25 m. Clasificación provisional del propio análisis (sin norma aplicada todavía).

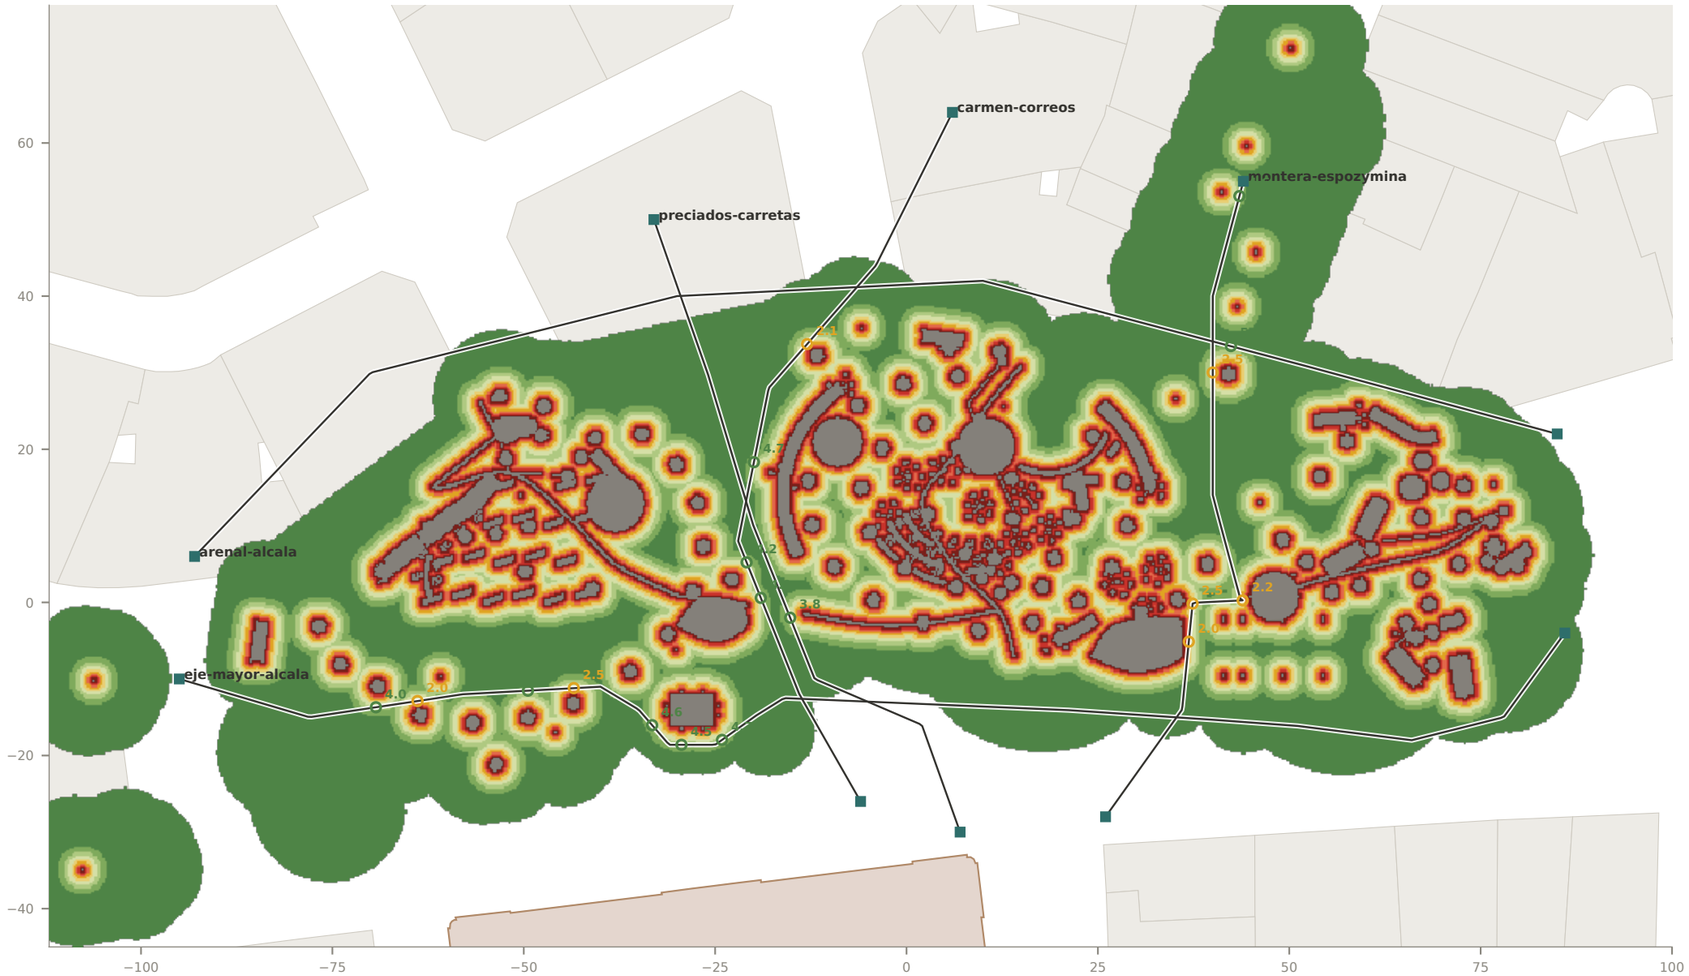

recorrido	L(m)	mín	p05	p50	holg.mín
eje-mayor-alcala	192	14.50	29.00	40.5	2.00
preciados-carretas	94	7.25	12.75	40.8	3.81
carmen-correos	102	7.50	12.50	41.0	2.12
montera-espozymina	94	8.50	10.50	52.2	1.50
arenal-alcala	192	15.25	34.00	47.2	5.52

ANCHURA TRANSVERSAL medida por rayos perpendiculares al eje declarado;
«holg. mín» = anchura libre local mínima sobre el eje.


umbral	comp>20m²	mayor	% suelo
0.90 m	1	9701 m²	94 %
1.20 m	2	9186 m²	90 %
1.50 m	2	9039 m²	88 %
1.80 m	2	8775 m²	86 %
2.00 m	3	8612 m²	84 %
2.50 m	1	8246 m²	80 %
3.00 m	1	7765 m²	75 %
4.00 m	1	7063 m²	68 %

FRAGMENTACIÓN: número de componentes conectadas del suelo libre al exigir esa anchura mínima continua.

cuello de botella entre los 10 accesos	peor par	mejor par
libre (puede rodear por la calle)	6.50 m	40.00 m
obligando a cruzar el ámbito	6.50 m	22.00 m

Maximin sobre la rejilla: anchura del punto más estrecho del mejor camino posible entre cada par de accesos. La red está holgadamente conectada; el problema no es la capacidad global sino los puntos locales listados en la página 2.



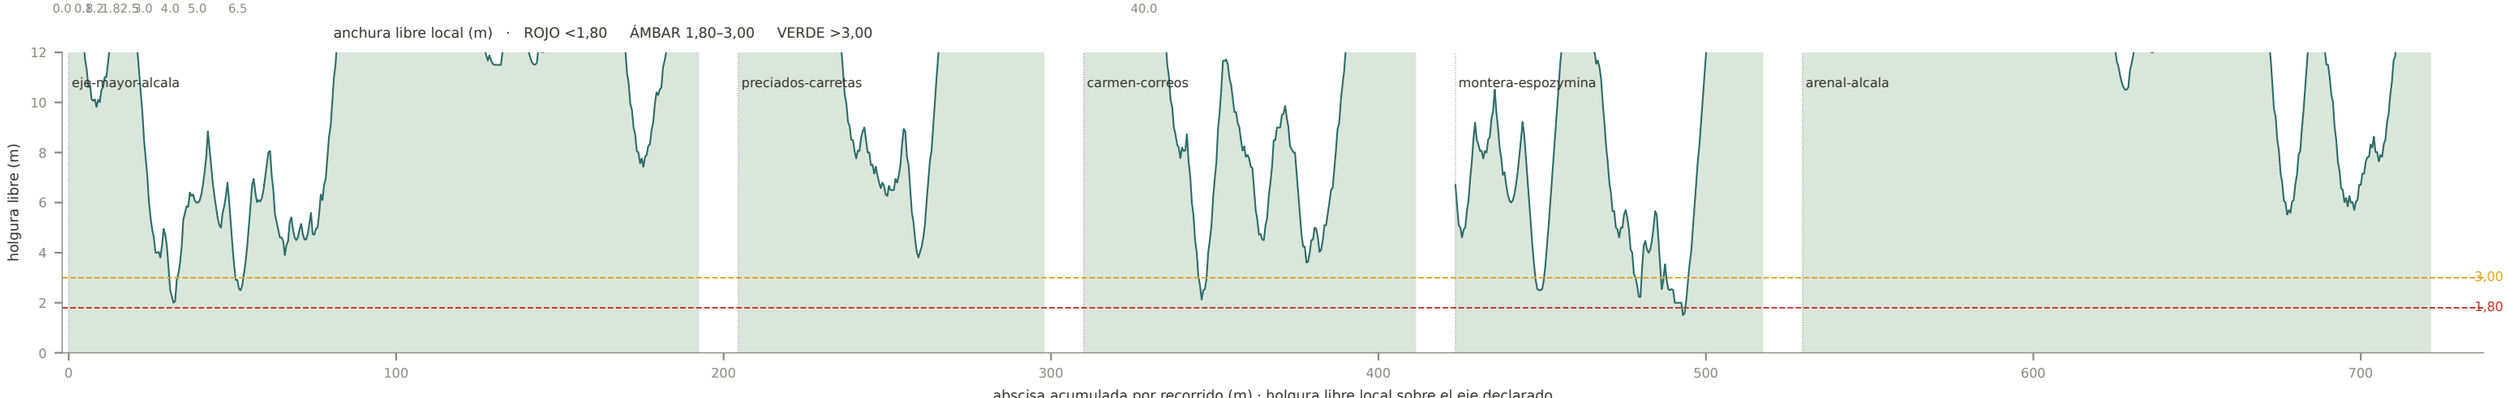

PATH_WIDTH_MAP · estrechamientos sobre los ejes, pasos estrangulados y bolsas

sobre el eje declarado	s(m)	x,y	holgura
eje-mayor-alcal	32	-64,-13	2.00
montera-espozym	68	37,-5	2.00
carmen-correos	36	-13,34	2.12
montera-espozym	56	44,0	2.24
eje-mayor-alcal	52	-43,-11	2.50
montera-espozym	26	40,30	2.50
montera-espozym	63	37,-0	2.55
preciados-carre	55	-15,-2	3.81
eje-mayor-alcal	26	-69,-14	4.00
carmen-correos	72	-19,1	4.03
carmen-correos	67	-21,5	4.24
eje-mayor-alcal	70	-29,-19	4.50
eje-mayor-alcal	64	-33,-16	4.61
montera-espozym	2	43,53	4.61
eje-mayor-alcal	75	-24,-18	4.72
carmen-correos	54	-20,18	4.72
eje-mayor-alcal	46	-49,-12	5.00
arenal-alcala	148	42,33	5.52
montera-espozym	48	42,8	5.66
arenal-alcala	166	60,29	5.85

pasos estrangulados x,y <1,20 m		entre familias
0.50	68,-9	PLANTER+PODS+VEGETATION
0.50	18,-5	PLANTER+VEGETATION
0.50	33,-1	PLANTER+STRUCTURE+VEGETA
0.50	30,0	STRUCTURE+VEGETATION
0.50	26,2	VEGETATION
0.50	29,2	STRUCTURE+VEGETATION
0.50	34,3	PLANTER+VEGETATION
0.50	31,4	VEGETATION
0.50	13,4	FURNITURE+PLANTER+VEGETA
0.50	33,5	VEGETATION
0.50	-50,5	PLANTER+VEGETATION
0.50	-61,7	FURNITURE+PODS+VEGETATIO
0.50	16,7	PLANTER+VEGETATION
0.50	6,7	PLANTER+VEGETATION+WATER
0.50	12,7	PLANTER+VEGETATION
0.50	19,8	PLANTER+VEGETATION
0.50	11,11	PLANTER+VEGETATION
0.50	15,12	PLANTER+VEGETATION+WATER
0.50	-3,12	FURNITURE+PLANTER+VEGETA
0.50	17,14	VEGETATION
0.50	2,16	VEGETATION+WATER
0.50	67,17	PODS
0.50	-0,18	PLANTER+VEGETATION
0.50	-41,21	STRUCTURE+WATER

26 pasos por debajo de 1,20 m de holgura en todo el ámbito (deduplicados a 2 m).



CRITERIO: se mide la geometría, no la norma. El umbral 1,80 m se usa como referencia de trabajo (cruce de dos personas / silla + peatón) y 3,00 m como umbral de holgura para un espacio público de esta intensidad de uso. La determinación normativa aplicable (Orden VIV/561/2010 y ordenanza municipal) queda pendiente de la fase de verificación normativa: aquí sólo se localiza y cuantifica.