
ESTRUCTURA URBANA Y PARCELA

Ribera de Curtidores 31 como bisagra entre mercado, vivienda y patios interiores

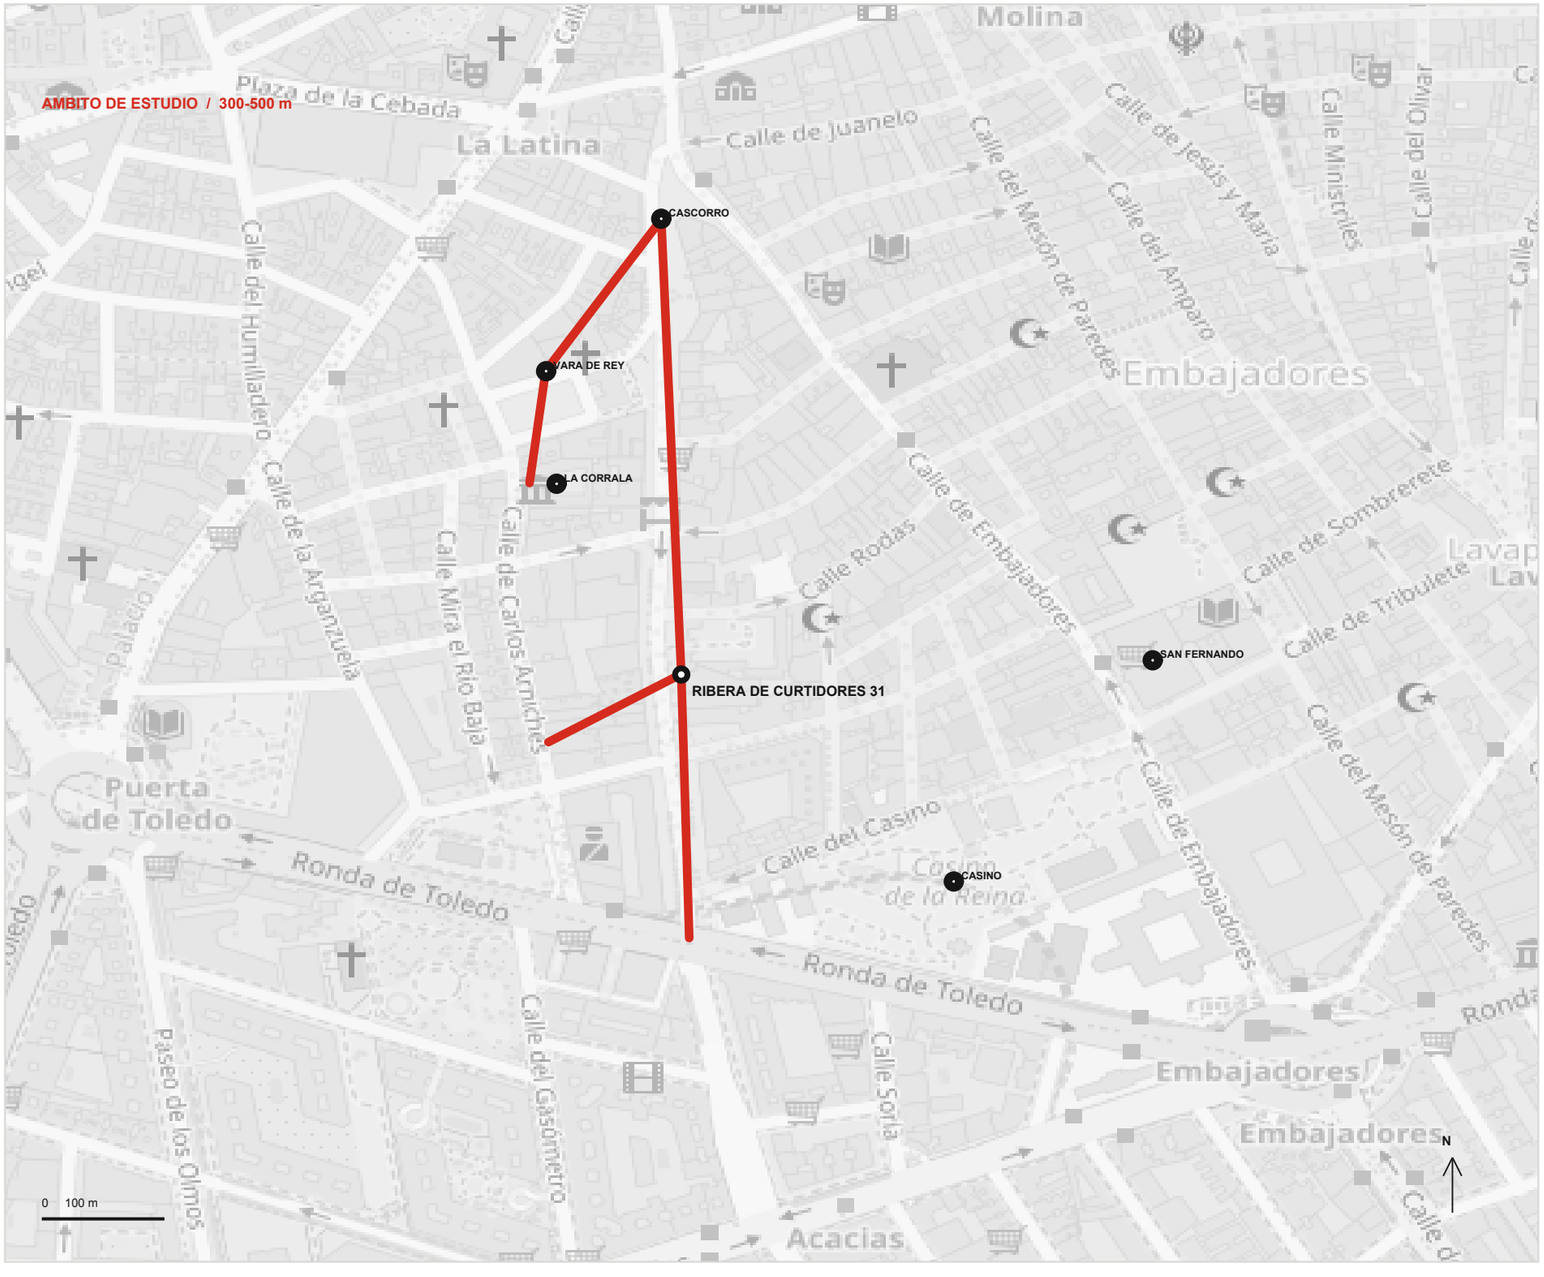

La parcela se sitúa sobre el eje principal del Rastro. La lectura útil no termina en el perímetro: debe incluir calle, medianeras, patios, accesos y el ciclo dominical.

1.500 m²
superficie aproximada del edificio
Dato del enunciado

20 / 40
unidades aproximadas / habitantes
Dato del enunciado

651 m²
parcela indicada por fuente secundaria
Verificar en Catastro

37,5 m²
superficie bruta por habitante
1.500 m² / 40

LECTURAS ESPACIALES

1. La fachada pertenece al mercado y a la vivienda.
2. El acceso residencial debe permanecer legible cuando la calle se satura.
3. La profundidad de parcela exige trabajar con patio y sección.
4. Las medianeras y las alturas vecinas condicionan luz, ventilación y volumen.

DATOS A CONFIRMAR EN LEVANTAMIENTO

- Límite y cotas exactas de parcela.
- Alturas, cornisas y medianeras.
- Accesos, acometidas y protección.
- Anchura real de calle y posición de puestos.
- Geometría y soleamiento de patios.

CONSECUENCIA

El primer dibujo de proyecto debe ser una sección completa desde la calle hasta el patio, no una planta aislada.