MOB-01 · MOVILIDAD Y ACCESIBILIDAD

La red peatonal

Anchuras, cuellos, continuidad y fragmentación del suelo pisable con el refugio construido: lo que la auditoría geométrica garantiza y lo que los escenarios de afluencia añaden.

SUELO PISABLE	PEOR CUELLO	CONTINUIDAD 1,80 M	EJES BLOQUEADOS
9.827 m²	3.8 m	84 %	0 de 6

MOB-01 · MOVILIDAD

Una plaza que sigue siendo plaza

¿El refugio estrangula el movimiento? Anchuras reales, cuellos entre accesos y fragmentación de la red a cada exigencia de ancho.

A·MEDIDO / CALCULADO

MÉTODO


Rásters de la auditoría v006 (celda 0,25 m, banda de cuerpo 0,05–2,10 m): anchura local 2×DT, cuello máximo entre los 45 pares de accesos por barrido de umbral, fragmentación por componentes conexas a cada ancho exigido.

DATOS

_reaudit9/_data/a1_paths .json + width.npy (0 RED en build 12).

LIMITACIONES

La holgura 2×DT es isótropa (subestima pasos diagonales); los umbrales 1,80/3,00 m son criterio de proyecto, no normativa de obligado cumplimiento.

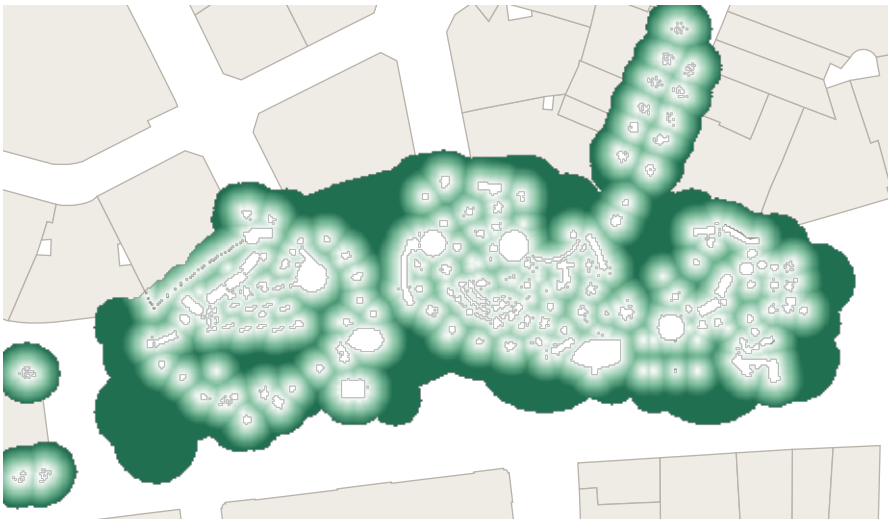

FUENTE: _reaudit9/_data (v006 build 12) + mob_engine.py · celda 0,25 m

CONTINUIDAD


Exigiendo 1,80 m continuos, la red mantiene el 84 %% del suelo en una sola pieza; a 3,00 m, el 73 %% en dos.

CUELLOS

El peor par de accesos conserva 3.8 m de paso: no existe cuello relevante a escala de multitud.

BOLSAS

0 cul-de-sac >8 m² imputables al proyecto (auditoría A1): las bolsas de v002 se reclasificaron o resolvieron en v003-v006.

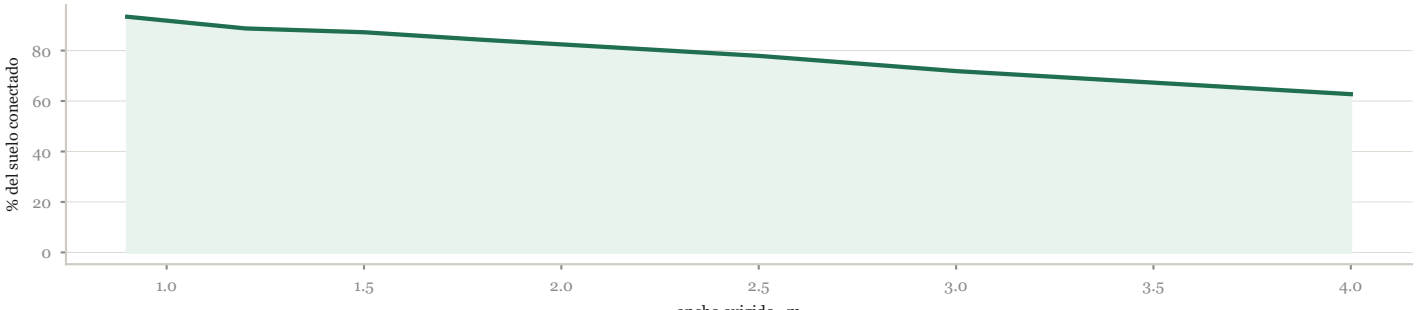

Cobertura de red frente a exigencia de ancho. La curva cae suave: no hay umbral catastrófico — la red degrada con elegancia.

FUENTE: _reaudit9/_data (v006 build 12) + mob_engine.py · celda 0,25 m