

PATH_WIDTH_MAP Â· anchura libre de la red peatonal

Anchura libre local = 2 Ã— distancia al obstÃ¡culo mÃ¡s prÃ³ximo en la banda de cuerpo 0,05â€“2,10 m. Rejilla 0,25 m. ClasificaciÃ³n provisional del propio anÃ¡lisis (sin norma aplicada todavÃa).

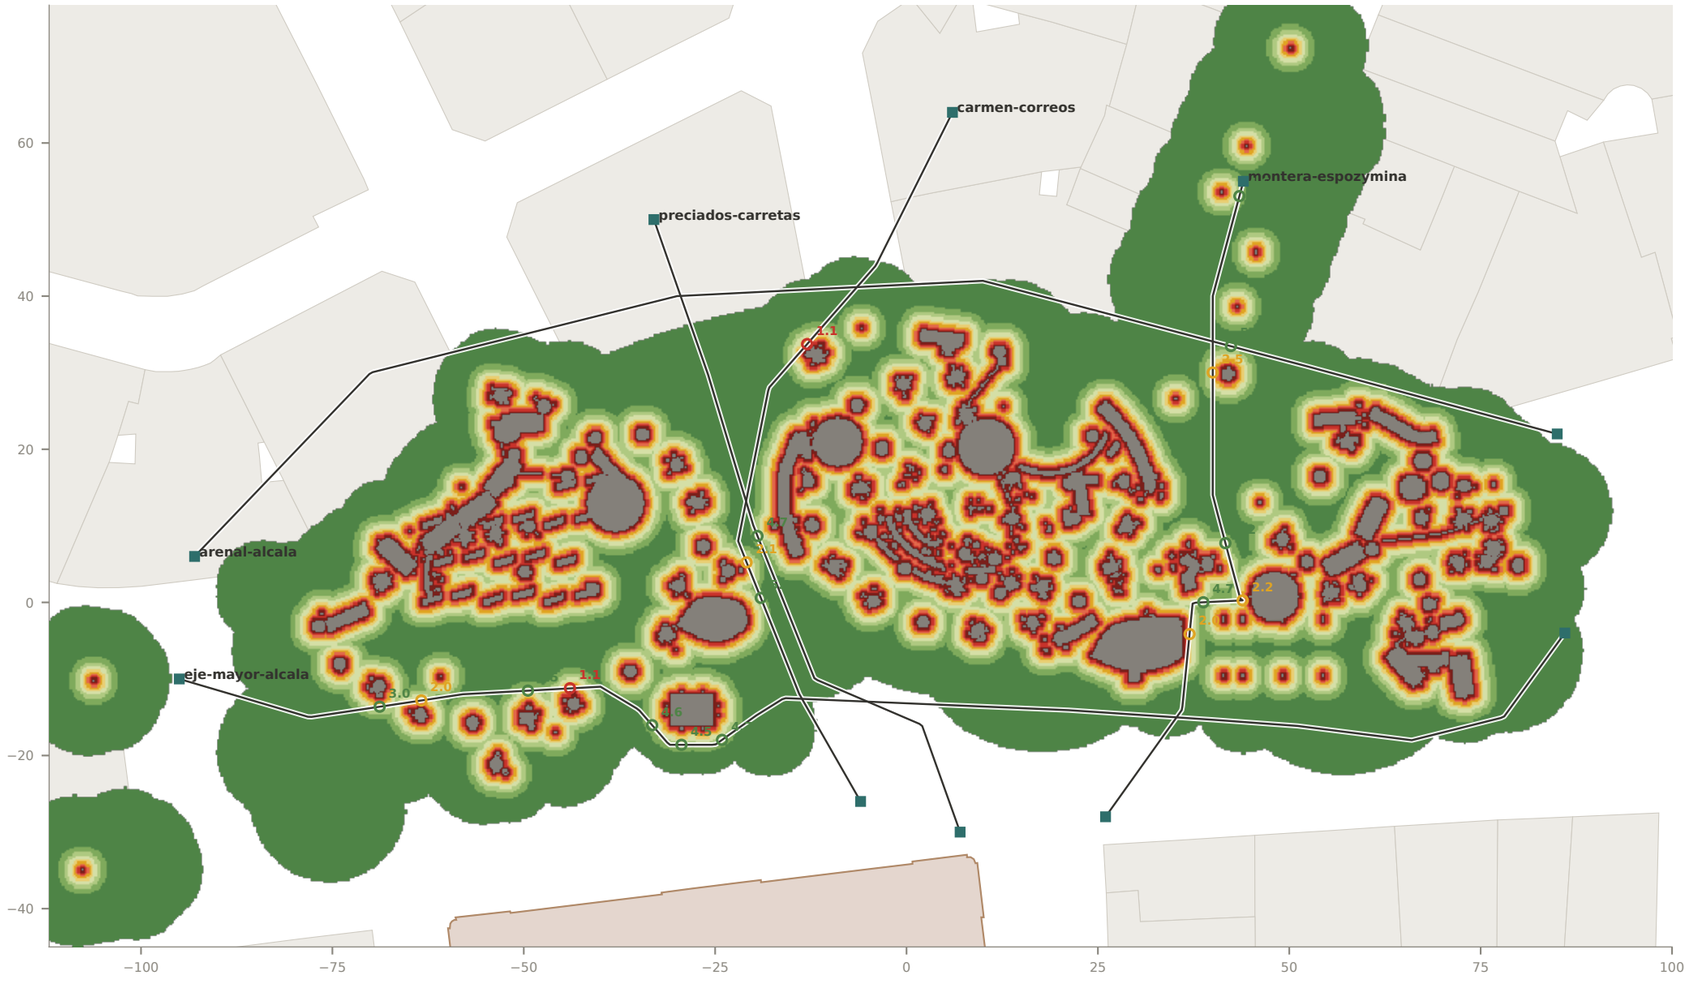

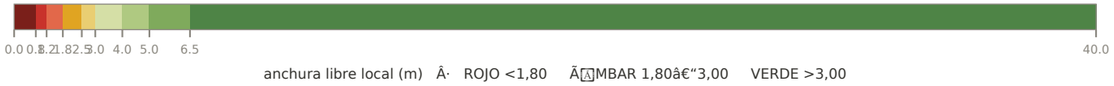

recorrido	L(m)	mÃn	p05	p50	holg.mÃn
eje-mayor-alcala	192	13.50	21.00	41.5	1.12
preciados-carretas	94	6.50	10.09	47.1	4.72
carmen-correos	102	6.50	10.26	43.2	1.12
montera-espozymina	94	7.50	11.45	48.2	1.50
arenal-alcala	192	15.25	34.00	48.5	5.52


ANCHURA TRANSVERSAL medida por rayos perpendiculares al eje declarado; Â«holg. mÃnÂ» = anchura libre local mÃnima sobre el eje.

umbral	comp>20mÂ²	mayor	% suelo
0.90 m	1	9757 mÂ²	94 %
1.20 m	1	9348 mÂ²	90 %
1.50 m	1	9220 mÂ²	89 %
1.80 m	2	8908 mÂ²	87 %
2.00 m	3	8739 mÂ²	85 %
2.50 m	2	8357 mÂ²	81 %
3.00 m	1	7849 mÂ²	77 %
4.00 m	2	7053 mÂ²	69 %

FRAGMENTACIÃ“N: nÃºmero de componentes conectadas del suelo libre al exigir esa anchura mÃnima continua.

cuello de botella entre los 10 accesos	peor par	mejor par
libre (puede rodear por la calle)	6.50 m	40.00 m
obligando a cruzar el Ã¡mbito	6.50 m	20.50 m


Maximin sobre la rejilla: anchura del punto mÃ¡s estrecho del mejor camino posible entre cada par de accesos. La red estÃ¡ holgadamente conectada; el problema no es la capacidad global sino los puntos locales listados en la pÃ¡gina 2.

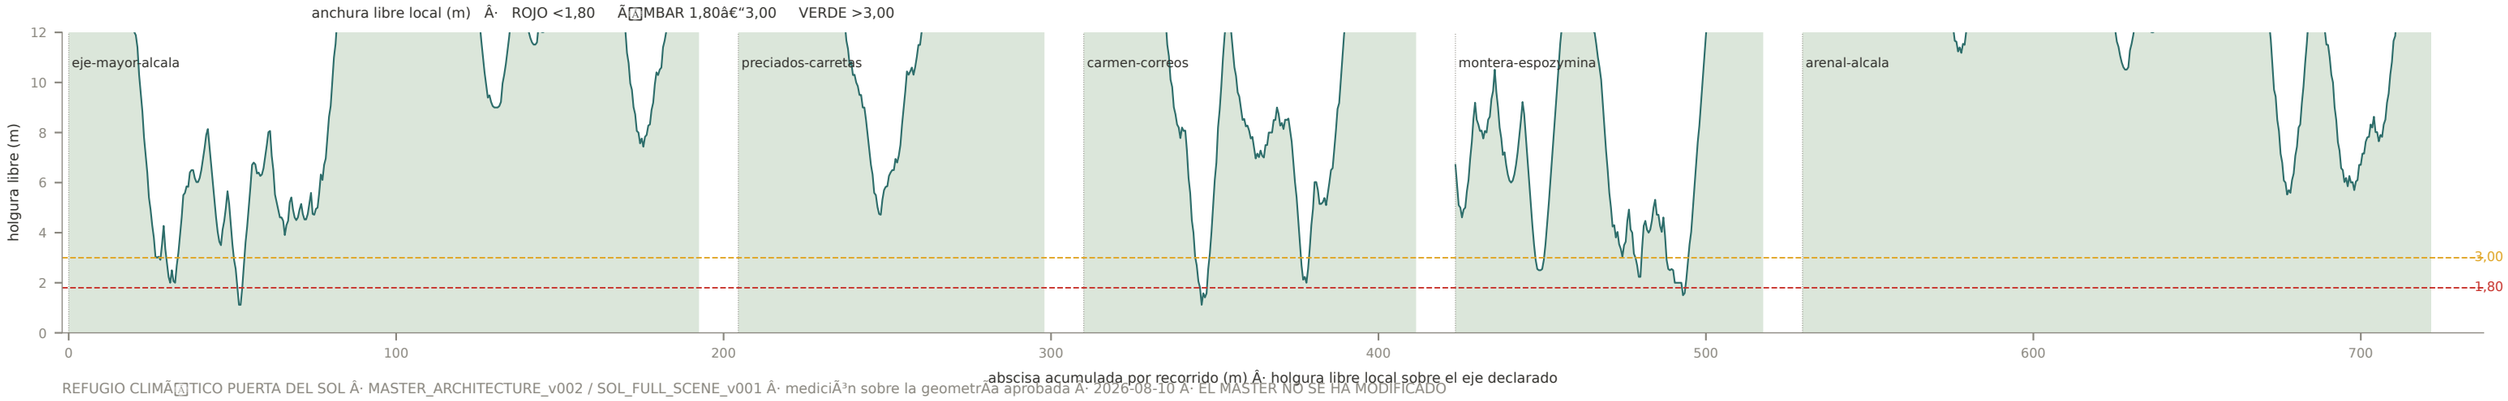

PATH_WIDTH_MAP Â· estrechamientos sobre los ejes, pasos estrangulados y bolsas

sobre el eje declarado	s(m)	x,y	holgura
eje-mayor-alcal	52	-44,-11	1.12
carmen-correos	36	-13,34	1.12
eje-mayor-alcal	32	-63,-13	2.00
montera-espozym	67	37,-4	2.00
carmen-correos	67	-21,5	2.12
montera-espozym	56	44,0	2.24
montera-espozym	26	40,30	2.50
eje-mayor-alcal	27	-69,-14	3.00
eje-mayor-alcal	46	-49,-12	3.50
montera-espozym	48	42,8	4.24
eje-mayor-alcal	70	-29,-19	4.50
eje-mayor-alcal	64	-33,-16	4.61
montera-espozym	2	43,53	4.61
eje-mayor-alcal	75	-24,-18	4.72
preciados-carre	44	-19,9	4.72
montera-espozym	62	39,0	4.72
carmen-correos	72	-19,1	5.15
arenal-alcala	148	42,33	5.52
arenal-alcala	166	60,29	5.85

pasos estrangulados x,y <1,20 m		entre familias
0.50	18,-5	PLANTER+VEGETATION
0.50	-76,-2	PLANTER+STRUCTURE+VEGETA
0.50	-29,1	VEGETATION+WATER
0.50	-4,2	PLANTER+VEGETATION
0.50	55,3	PLANTER+PODS+VEGETATION
0.50	6,5	FURNITURE+PLANTER+VEGETA
0.50	-50,5	PLANTER+VEGETATION
0.50	13,6	FURNITURE+PLANTER+VEGETA
0.50	35,6	PLANTER+VEGETATION
0.50	4,6	FURNITURE+PLANTER+VEGETA
0.50	15,7	PLANTER+VEGETATION
0.50	37,7	PLANTER+VEGETATION
0.50	14,9	PLANTER+VEGETATION
0.50	9,13	VEGETATION
0.50	14,13	VEGETATION+WATER
0.50	72,14	PLANTER+PODS+VEGETATION
0.50	-0,16	VEGETATION
0.50	67,17	PODS
0.50	59,25	PLANTER+VEGETATION+WATER
0.50	5,32	STRUCTURE+VEGETATION

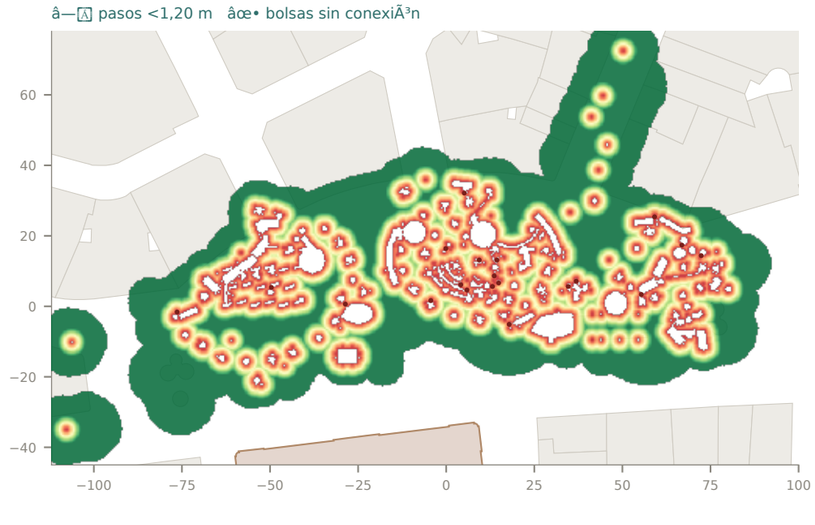

20 pasos por debajo de 1,20 m de holgura en todo el Ã¡mbito (deduplicados a 2 m).

CRITERIO: se mide la geometrÃa, no la norma. El umbral 1,80 m se usa como referencia de trabajo (cruce de dos personas / silla + peatÃ³n) y 3,00 m como umbral de holgura para un espacio pÃºblico de esta intensidad de uso. La determinaciÃ³n normativa aplicable (Orden VIV/561/2010 y ordenanza municipal) queda pendiente de la fase de verificaciÃ³n normativa: aquÃ sÃ³lo se localiza y cuantifica.