
ACCESSIBILITY_PRECHECK Â· quÃ© itinerarios pueden funcionar como accesibles


PRE-CHEQUEO GEOMÃ‰TRICO. No es un certificado normativo: identifica quÃ© trazas tienen geometrÃa compatible con un itinerario accesible y cuÃ¡les claramente no.

verde â‰¥1,80 m Â· Ã¡mbar 1,20â€“1,80 Â· rojo <1,20 Â· rosa = cinta +6,00 (â–² escaleras)

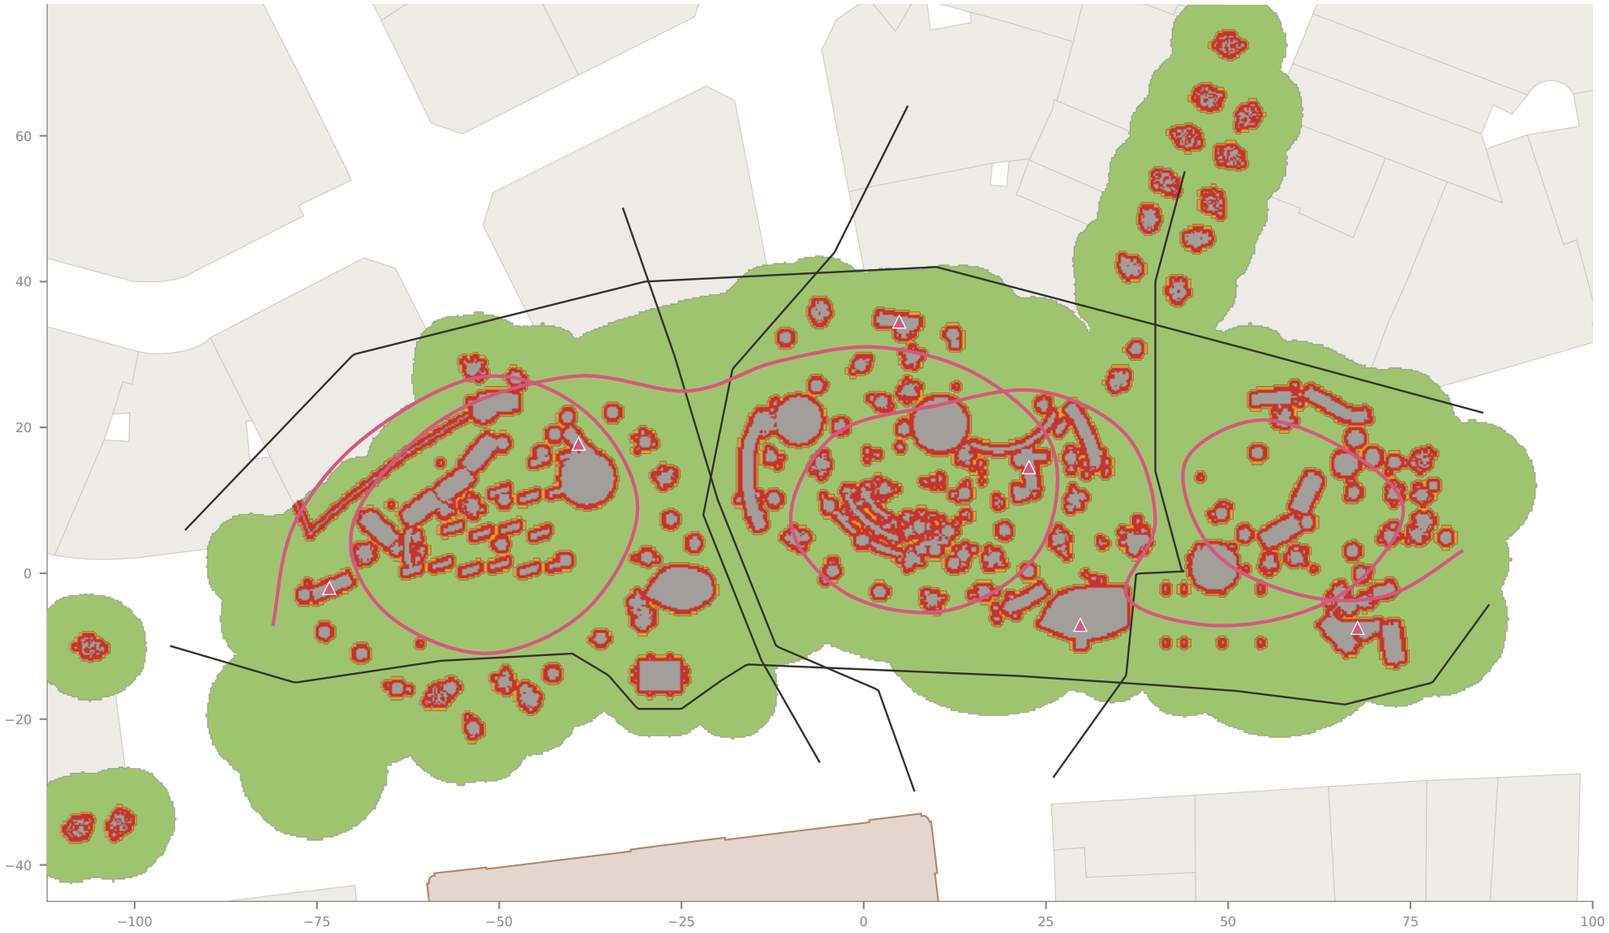

itinerario	ancho mÃn	% â‰¥1,80	pend %	veredicto
eje-mayor-alcala	3.54	100%	0.0	APTO
preciados-carretas	4.72	100%	0.0	APTO
carmen-correos	3.61	100%	0.0	APTO
montera-espozymina	0.71	97%	0.0	CONDICIONADO
arenal-alcala	3.54	100%	0.0	APTO
CINTA +6.00	2.31	100%	0.0	APTO CON ASCEN

escalera de la cinta tal como estÃ¡ construida: CH 0.162 Â· H 0.290 Â· 56%

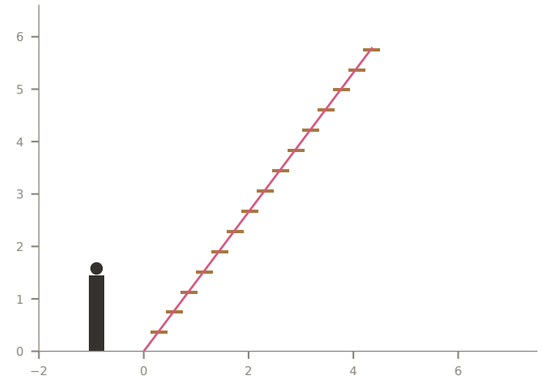

LECTURA. El plano de plaza es horizontal en todo el Ã¡mbito (cota 0,00 en toda la superficie construida): no hay pendientes que evaluar a nivel de suelo, y la accesibilidad a cota 0 depende exclusivamente de anchura, obstÃ¡culos y giros. El Ãºnico cambio de nivel del proyecto es la cinta a +6,00, resuelto con 6 escaleras de contrahuella 0,385 m y pendiente 91 % (42Â°), sin barandilla, sin meseta y sin ningÃºn medio alternativo: geomÃ©tricamente la cota +6,00 no es accesible y, tal como estÃ¡, tampoco es una escalera utilizable.

Bordes sin protecciÃ³n detectados: 4 estanques con bordillo de 0,60 m sin barandilla ni cambio de textura, y la barandilla de la cinta (1,05 m) sin travesaÃ±o intermedio ni rodapiÃ©.

CÃrculo de giro: se comprueba Ã˜1,50 m sobre el eje de cada recorrido (columna Â«% â‰¥1,80Â» y el mapa verde). La banda Ã¡mbar admite un peatÃ³n pero no el cruce con silla de ruedas.