
PATH_WIDTH_MAP Â· anchura libre de la red peatonal

Anchura libre local = 2 Ã— distancia al obstÃ¡culo mÃ¡s prÃ³ximo en la banda de cuerpo 0,05â€“2,10 m. Rejilla 0,25 m. ClasificaciÃ³n provisional del propio anÃ¡lisis (sin norma aplicada todavÃa).

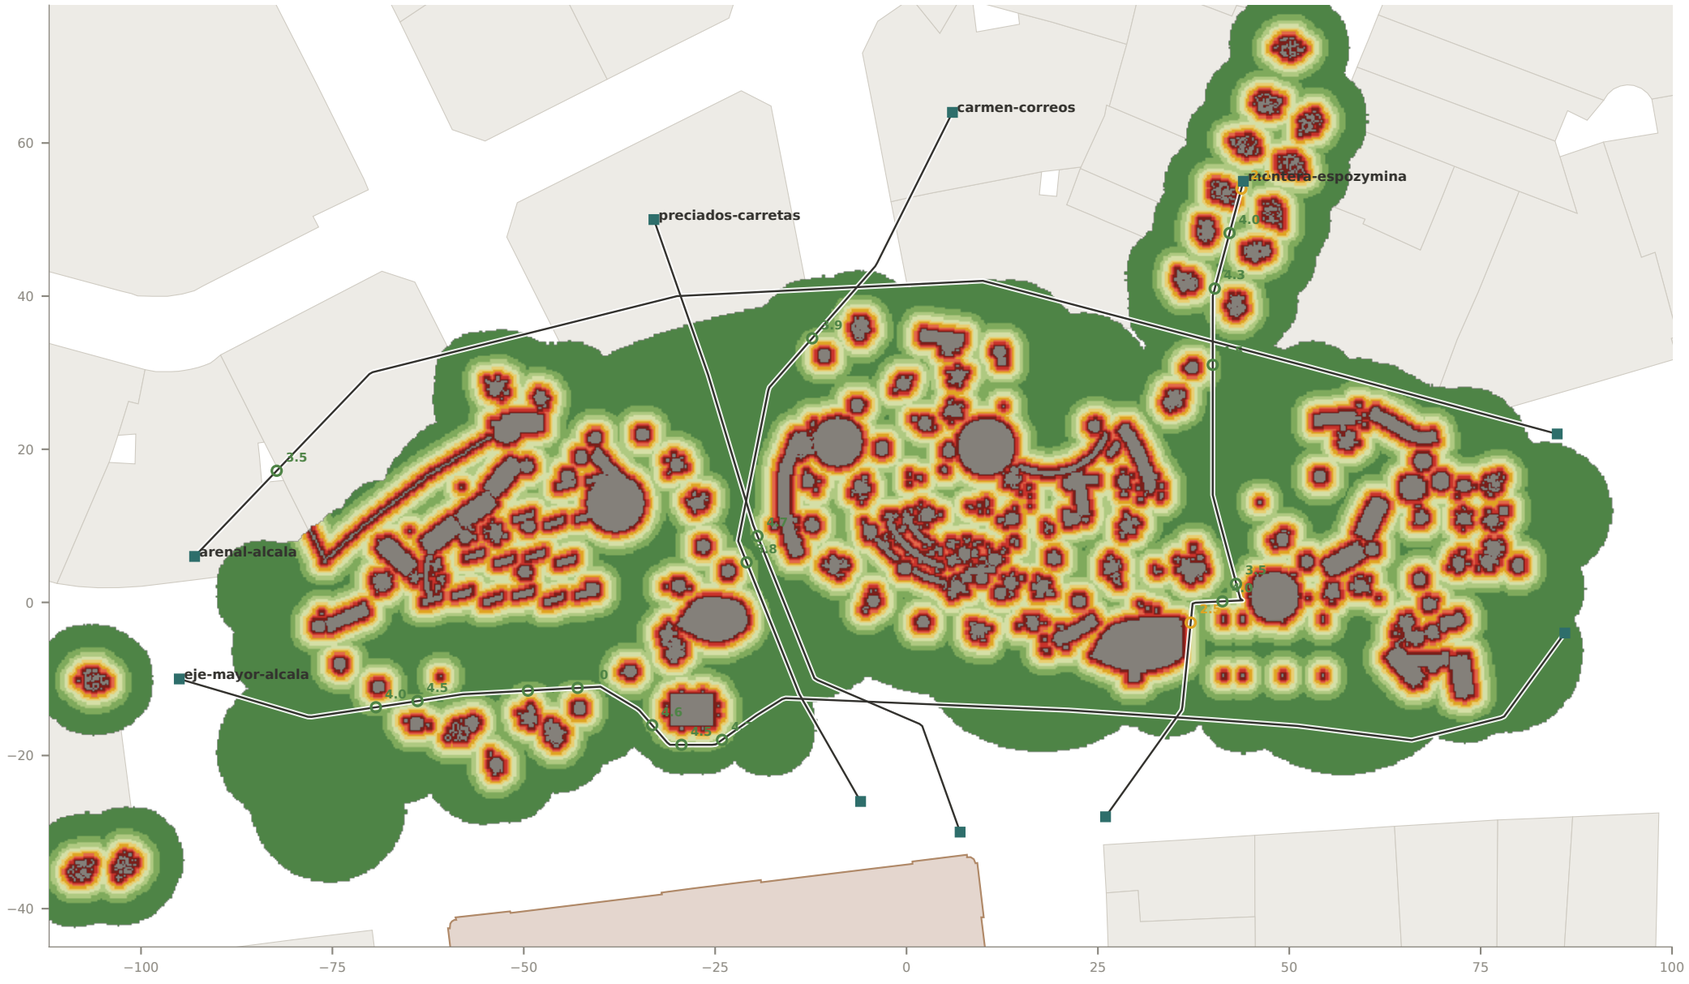

recorrido	L(m)	mÃn	p05	p50	holg.mÃn
eje-mayor-alcala	192	6.75	16.81	41.1	3.54
preciados-carretas	94	7.25	11.09	47.2	4.72
carmen-correos	102	7.50	11.79	41.9	3.61
montera-espozymina	94	3.75	5.55	34.5	0.71
arenal-alcala	192	13.75	25.00	44.5	3.54


ANCHURA TRANSVERSAL medida por rayos perpendiculares al eje declarado; Â«holg. mÃnÂ» = anchura libre local mÃnima sobre el eje.


umbral	comp>20mÂ²	mayor	% suelo
0.90 m	1	9167 mÂ²	93 %
1.20 m	1	8716 mÂ²	89 %
1.50 m	1	8569 mÂ²	87 %
1.80 m	1	8275 mÂ²	84 %
2.00 m	2	8068 mÂ²	82 %
2.50 m	1	7626 mÂ²	78 %
3.00 m	3	6960 mÂ²	72 %
4.00 m	3	6024 mÂ²	63 %

FRAGMENTACIÃ“N: nÃºmero de componentes conectadas del suelo libre al exigir esa anchura mÃnima continua.

cuello de botella entre los 10 accesos	peor par	mejor par
libre (puede rodear por la calle)	3.75 m	40.00 m
obligando a cruzar el Ã¡mbito	3.75 m	20.50 m

Maximin sobre la rejilla: anchura del punto mÃ¡s estrecho del mejor camino posible entre cada par de accesos. La red estÃ¡ holgadamente conectada; el problema no es la capacidad global sino los puntos locales listados en la pÃ¡gina 2.

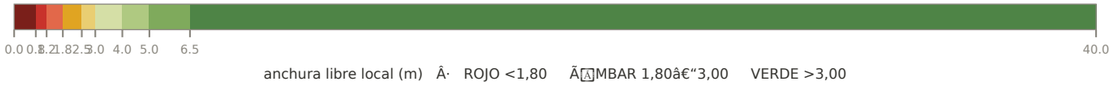

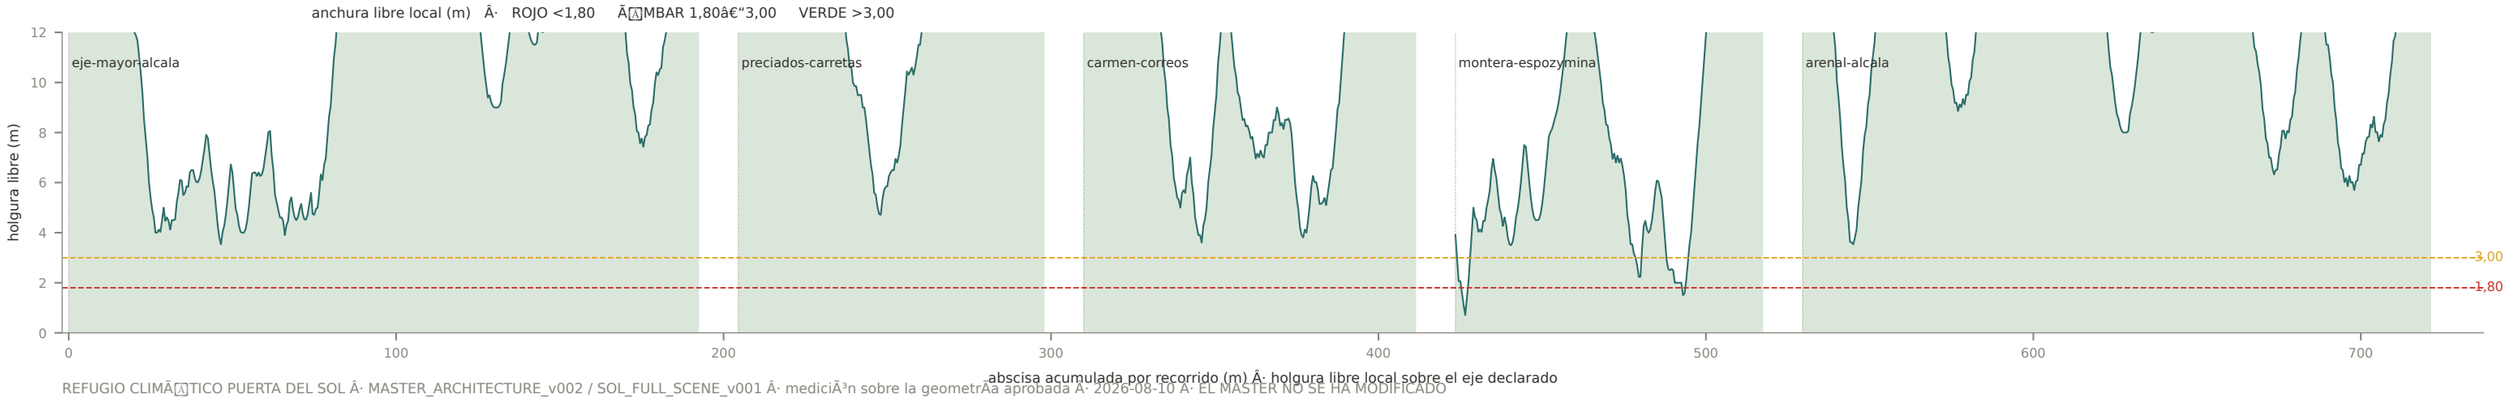


PATH_WIDTH_MAP Â· estrechamientos sobre los ejes, pasos estrangulados y bolsas

sobre el eje declarado	s(m)	x,y	holgura
montera-espozym	1	44,54	2.06
montera-espozym	66	37,-3	2.50
eje-mayor-alcal	46	-49,-12	3.54
montera-espozym	54	43,2	3.54
arenal-alcala	16	-82,17	3.54
carmen-correos	67	-21,5	3.81
carmen-correos	35	-12,34	3.91
eje-mayor-alcal	26	-69,-14	4.00
eje-mayor-alcal	53	-43,-11	4.00
montera-espozym	59	41,0	4.00
montera-espozym	7	42,48	4.03
montera-espozym	14	40,41	4.27
eje-mayor-alcal	32	-64,-13	4.50
eje-mayor-alcal	70	-29,-19	4.50
montera-espozym	24	40,31	4.50
eje-mayor-alcal	64	-33,-16	4.61
eje-mayor-alcal	75	-24,-18	4.72
preciados-carre	44	-19,9	4.72
carmen-correos	30	-9,39	5.00
carmen-correos	72	-19,1	5.15
arenal-alcala	166	60,29	5.85

pasos estrangulados	x,y
0.50	18,-5
0.50	-76,-2
0.50	33,-1
0.50	-31,2
0.50	55,3
0.50	-50,5
0.50	37,7
0.50	72,14
0.50	16,15
0.50	0,16
0.50	67,17
0.50	-48,25
0.50	59,25
0.50	-54,27

â— pasos <1,20 m âœ• bolsas sin conexiÃ³n

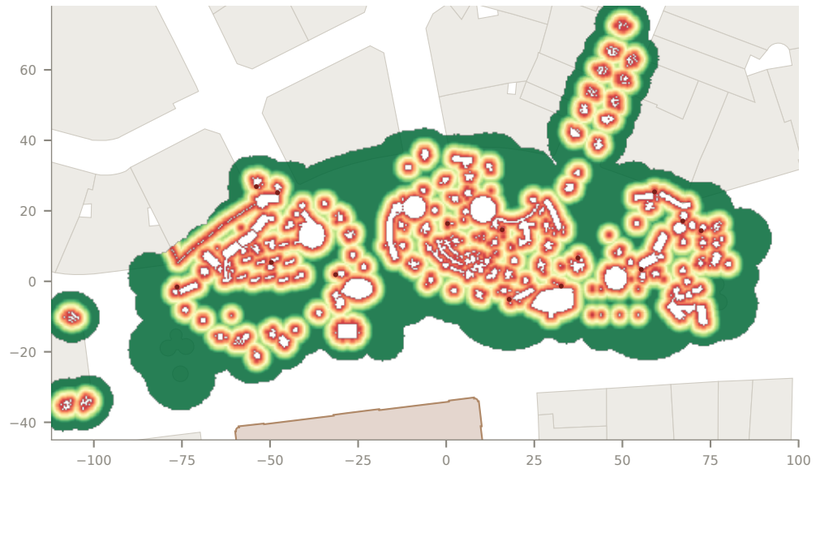

14 pasos por debajo de 1,20 m de holgura en todo el Ã¡mbito (deduplicados a 2 m).

CRITERIO: se mide la geometrÃa, no la norma. El umbral 1,80 m se usa como referencia de trabajo (cruce de dos personas / silla + peatÃ³n) y 3,00 m como umbral de holgura para un espacio pÃºblico de esta intensidad de uso. La determinaciÃ³n normativa aplicable (Orden VIV/561/2010 y ordenanza municipal) queda pendiente de la fase de verificaciÃ³n normativa: aquÃ sÃ³lo se localiza y cuantifica.