RIBERA 31

una calle que baja 37 m · un solar que no está vacío · un sol de invierno que solo llega arriba

A · **650,9 m²** superficie de parcela

A · **49,48 m** de fondo: una corrala

A · **14,93 m** de frente a Ribera

A · **6,8 %** de pendiente frente al 31

B · **0,17 h** de sol en el suelo el 21-dic

A · **25,8 m** de ancho de calle

A · **3.204** viviendas catastrales en 200 m

A · **339 m** a la boca de metro más próxima

B · **30/39** huecos con balcón propio

A · **418** comercios OSM en 500 m

B · **−37 m** de Cascorro a la Ronda

FICHA

PARCELA	Ribera de Curtidores 31 · 28005 Madrid
SITUACIÓN	El Rastro · Embajadores · Centro
ENCARGO	Vivienda temporal para jóvenes
CURSO	G3 · Proyectos · UEM · 2026-27
AUTOR	Adam Ihab
SRC	ETRS89 · UTM 30N (EPSG:25830)

ÍNDICE

01 MAPEADOS · 7 capas
02 RADIO · 500 m
03 LA CALLE QUE BAJA
04 PATRONES · P01–P11
05 SOL · TIEMPO · CRITERIOS


CERTEZA


A medido: catastro, OSM, SV, MER
B inferido: lectura visual, modelo
C hipótesis de proyecto

01 MAPEADOS · SIETE CAPAS SOBRE UN PUNTO

A · MEDIDO

MAPPEADOS/ · QGIS 3.40 GeoPDF · inventario OSM 600 m · MER 2021 · georreferencia exacta por GPTS

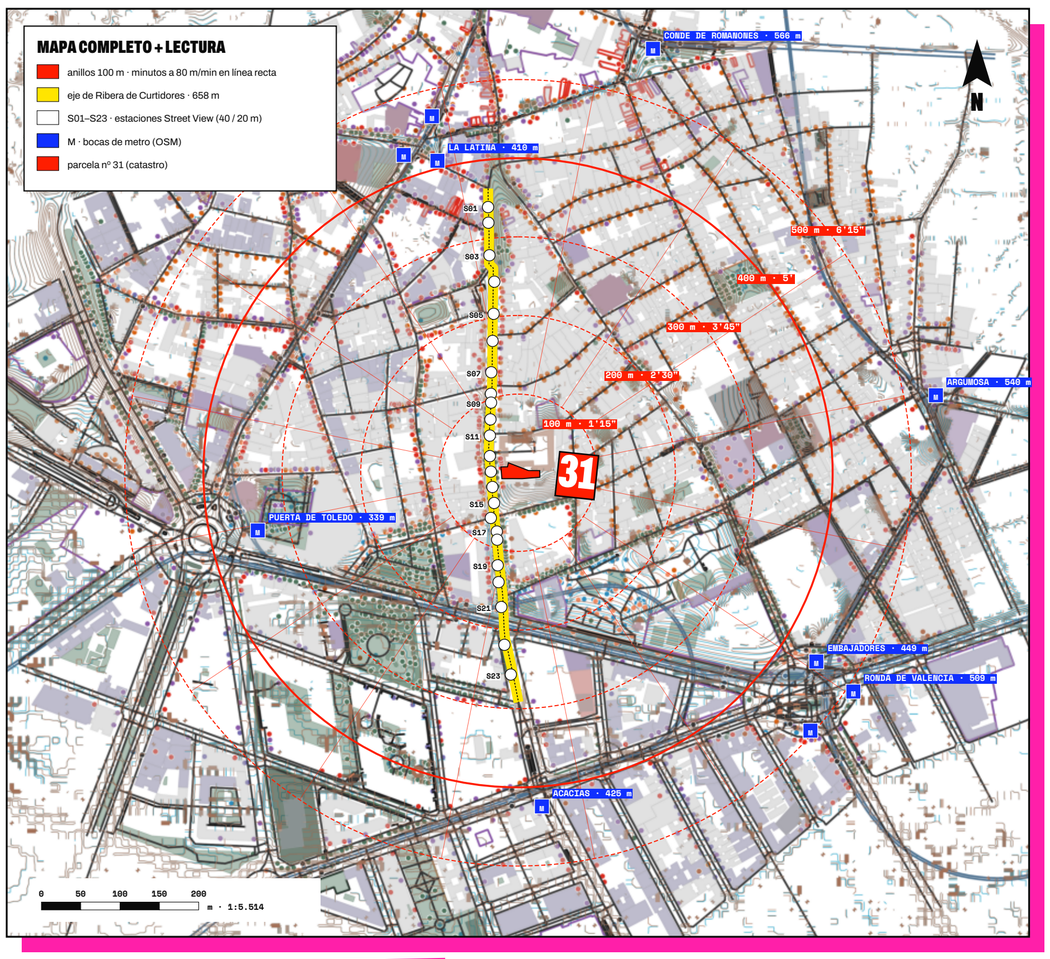

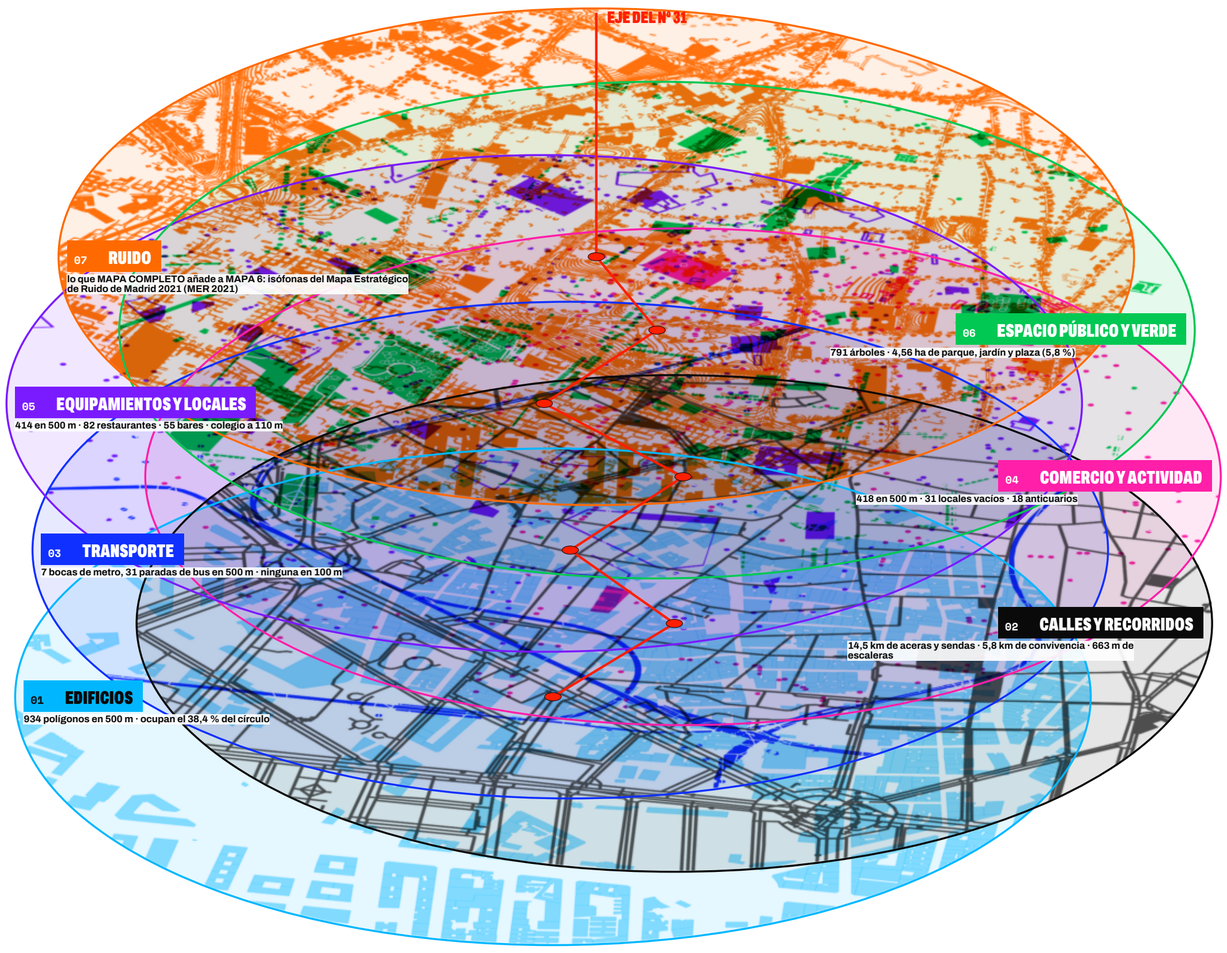


Láminas = diferencia píxel a píxel entre MAPA 1…6 y COMPLETO (220 ppp), r = 560 m, dimétrica −32° · ×0,46, superpuestas en multiplicación.

02 RADIO · QUÉ HAY A 500 M

A · MEDIDO

INVENTARIO_FISICO_600M.gpkg (OSM, 8.021 elementos) · centro: centroide de la parcela

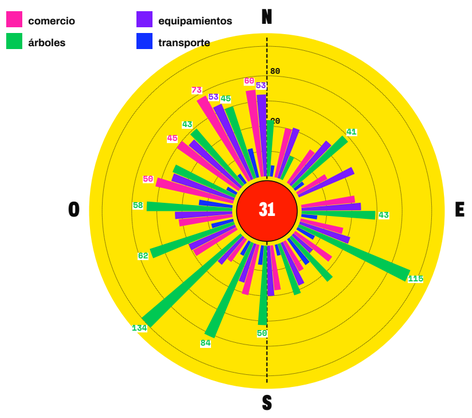


ROSA · 16 sectores × 4 temas · 0–500 m · radio = raiz de n
discontinua: eje de Ribera (N–S)

DENSIDAD · elementos por hectárea en cada anillo

		0–100 m	100–200 m	200–300 m	300–400 m	400–500 m
comercio	418	8,3	6,6	4,3	4,9	5,5
equipamientos	414	0,6	3,0	5,2	5,6	6,3
árboles	791	16,9	19,1	11,3	9,8	5,8
bancos	161	1,3	5,3	1,6	2,5	0,9
paradas / bocas	43	0,0	0,1	0,2	0,6	0,9
portales	1186	18,5	19,3	10,3	15,3	15,8
farolas	372	5,4	12,1	4,6	3,8	3,0
patrimonio	68	1,3	1,0	1,0	0,6	0,9
barreras	155	0,6	0,4	1,1	2,1	3,0
edificios	934	11,1	14,3	11,1	11,5	11,9

Marco negro = anillo de máxima densidad de la fila; tono relativo a la fila.

A CUÁNTO ESTÁ · línea recta desde el centroide de la parcela

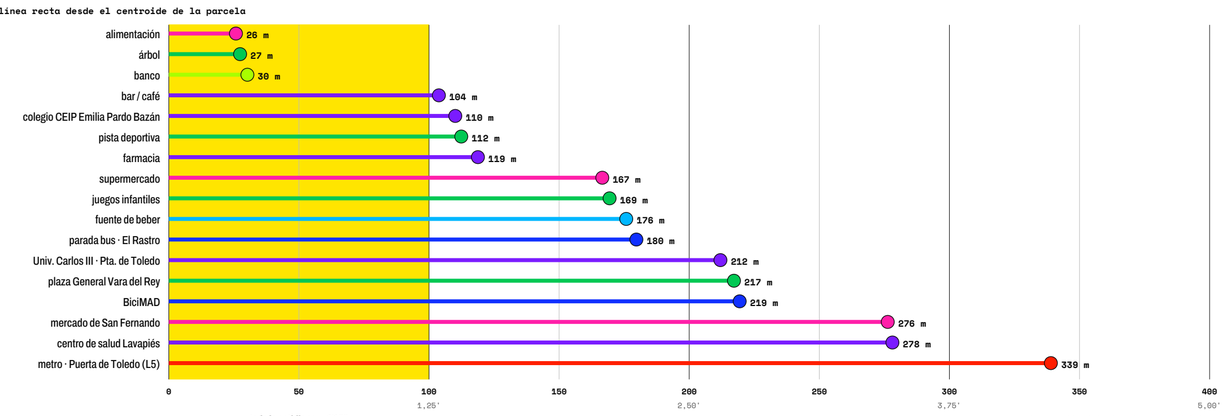


todo lo cotidiano: < 1'15"

minutos a 80 m/min sin rodeos = cota inferior

03 LA CALLE QUE BAJA · 580 M DE RIBERA DESPLEGADOS SOBRE SU PENDIENTE

A/B · MEDIDO + INFERIDO

alzados rectificados de 23 panorámicas SV 2021-22 · cotas de cámara SV − 2,5 m (B)

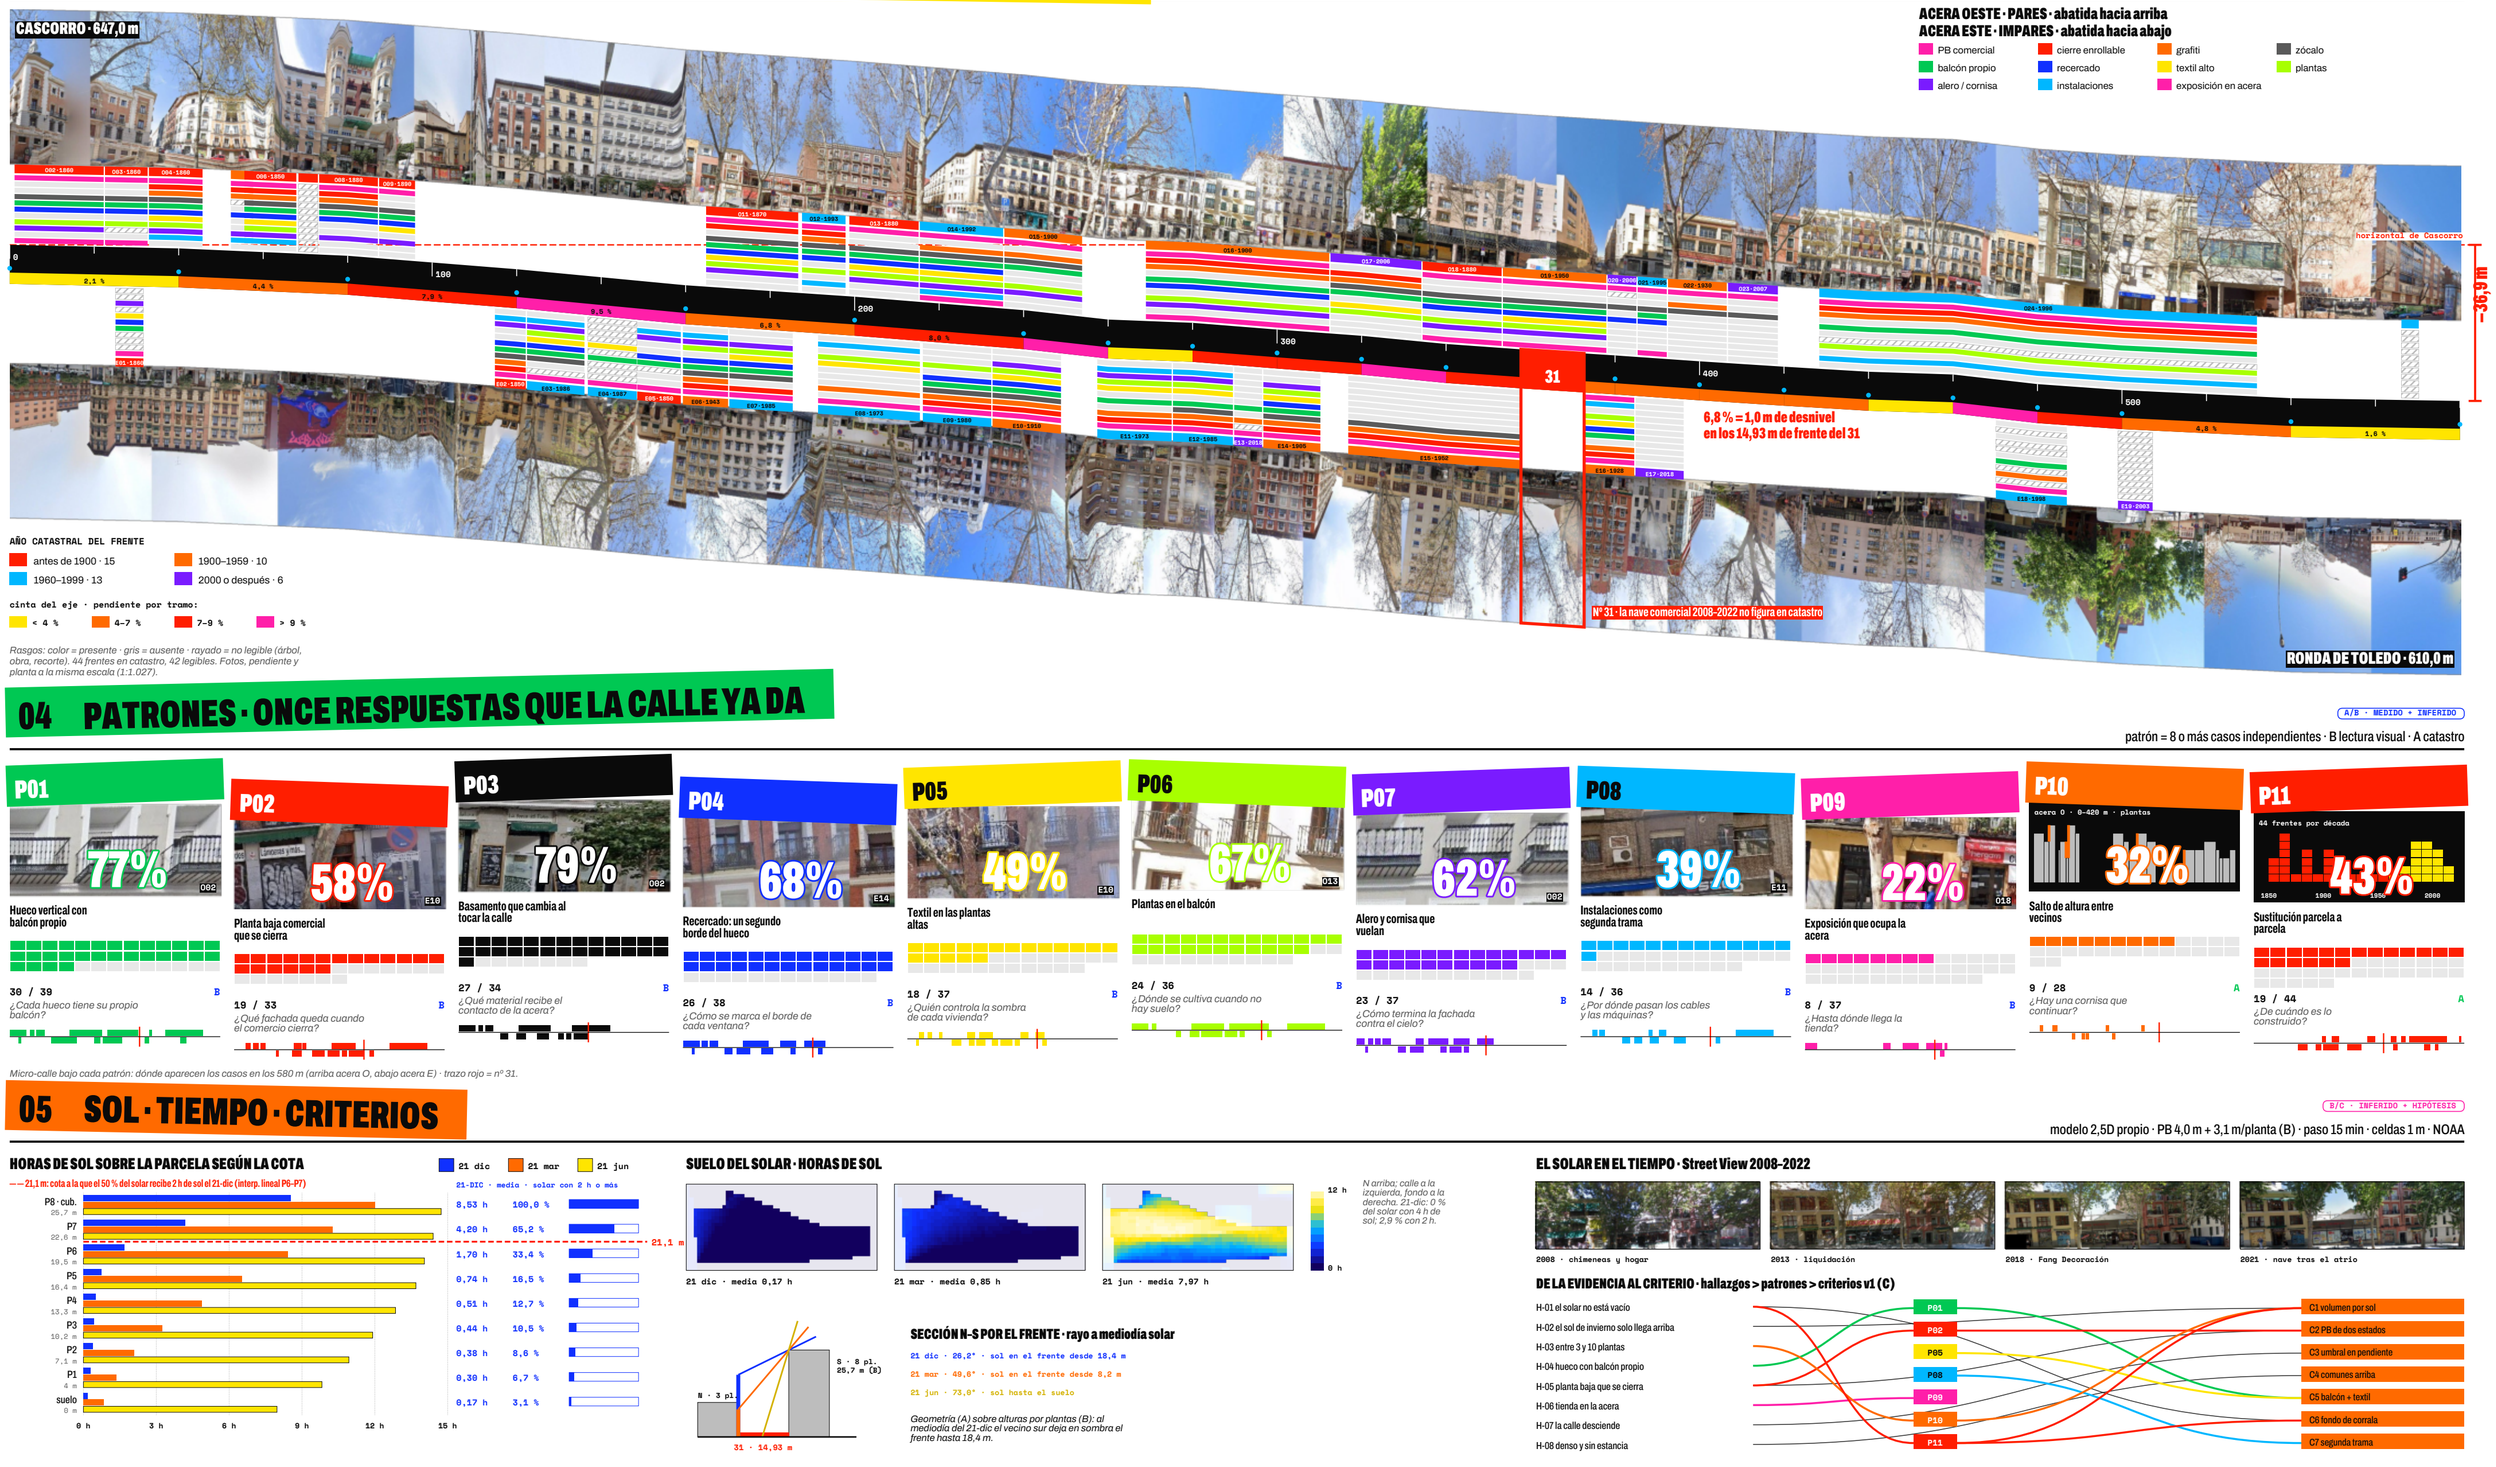

AÑO CATASTRAL DEL FRENTE
antes de 1900 · 15
1900–1959 · 10
1960–1999 · 13
2000 o después · 6

cinta del eje · pendiente por tramo:
< 4 %
4–7 %
7–9 %
> 9 %

Rasgos: color = presente · gris = ausente · rayado = no legible (árbol, obra, recorte). 44 frentes en catastro, 42 legibles. Fotos, pendiente y planta a la misma escala (1:1.027).

04 PATRONES · ONCE RESPUESTAS QUE LA CALLE YA DA

A/B · MEDIDO + INFERIDO

patrón = 8 o más casos independientes · B lectura visual · A catastro

Micro-calle bajo cada patrón: dónde aparecen los casos en los 580 m (arriba acera O, abajo acera E) · trazo rojo = nº 31.

05 SOL · TIEMPO · CRITERIOS

B/C · INFERIDO + HIPÓTESIS

modelo 2,5D propio · PB 4,0 m + 3,1 m/planta (B) · paso 15 min · celdas 1 m · NOAA

HORAS DE SOL SOBRE LA PARCELA SEGÚN LA COTA

SUELO DEL SOLAR · HORAS DE SOL

N arriba; calle a la izquierda, fondo a la derecha. 21-dic: 0 % del solar con 4 h de sol; 2,9 % con 2 h.

SECCIÓN N-S POR EL FRENTE · rayo a mediodía solar

21 dic · 26,2° · sol en el frente desde 18,4 m
21 mar · 49,6° · sol en el frente desde 8,2 m
21 jun · 73,6° · sol hasta el suelo

Geometría (A) sobre alturas por plantas (B): al mediodía del 21-dic el vecino sur deja en sombra el frente hasta 18,4 m.

EL SOLAR EN EL TIEMPO · Street View 2008–2022

DE LA EVIDENCIA AL CRITERIO · hallazgos > patrones > criterios v1 (C)

FUENTES · Catastro INSPIRE WFS + OVC (23-09-2026) · MAPPEADOS/ e INVENTARIO_FISICO_600M.gpkg (OpenStreetMap vía QGIS, 21/22-09-2026) · MER 2021 (Ayto. de Madrid) · Google Street View 2008–2022 (23 estaciones + 11 fechas del nº 31) · modelo de sombras y alzados rectificados propios.

Distancias en línea recta; recuentos OSM = lo que el inventario contiene (A). Alturas por plantas catastrales con PB 4,0 m + 3,1 m (B). Cotas de calle desde la altitud de cámara SV (B).