RIBERA 31

Una calle que baja 37 metros en 580, un solar que no está vacío y un sol de invierno que solo llega arriba. Siete mapeados, 42 fachadas, 23 panorámicas y un modelo de sombras leídos a la vez.

FICHA

PARCELA	Ribera de Curtidores 31 · 28005 Madrid
SITUACIÓN	El Rastro · Embajadores · Centro
ENCARGO	Vivienda temporal para jóvenes
CURSO	G3 · Proyectos · UEM · 2026-27
AUTOR	Adam Ihab
FECHA	24-09-2026
SRC	ETRS89 · UTM 30N (EPSG:25830)

ÍNDICE

01 MAPEADOS · 7 capas
02 RADIO · 500 m a pie
03 LA CALLE DESPLEGADA
04 PATRONES · P01-P11
05 SOL · TIEMPO · CRITERIOS

CERTEZA

A medido: catastro, OSM, SV
B inferido: lectura visual, modelo
C hipótesis de proyecto


Cada dato del panel lleva su nivel.


650,9 m² superficie de parcela (A)	**14,93 m** frente a Ribera (A)	**49,48 m** fondo: una corrala (A)	**25,8 m** ancho de calle en el 31 (A)	**6,8 %** pendiente frente al 31 (A)	**0,17 h** sol medio en suelo · 21-dic (B)	**3.204** viviendas catastrales en 200 m (A)	**339 m** a la boca de metro más próxima (A)	**418** comercios OSM en 500 m (A)	**30/39** huecos con balcón propio (B)

01 MAPEADOS · SIETE CAPAS SOBRE EL MISMO PUNTO

A · MEDIDO

Fuente: MAPPEADOS/ (QGIS 3.40, GeoPDF) · inventario OSM 600 m · georreferencia exacta por GPTS

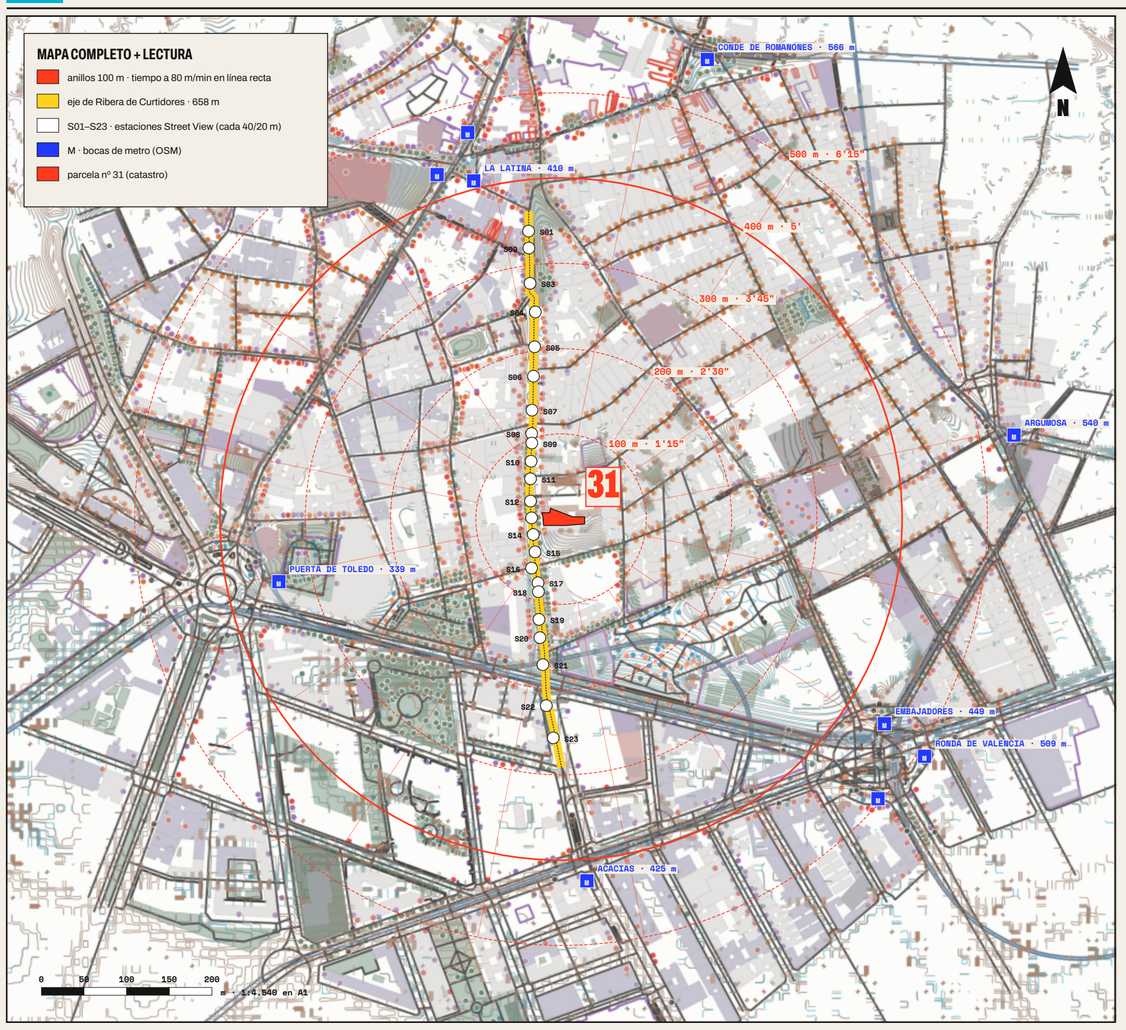

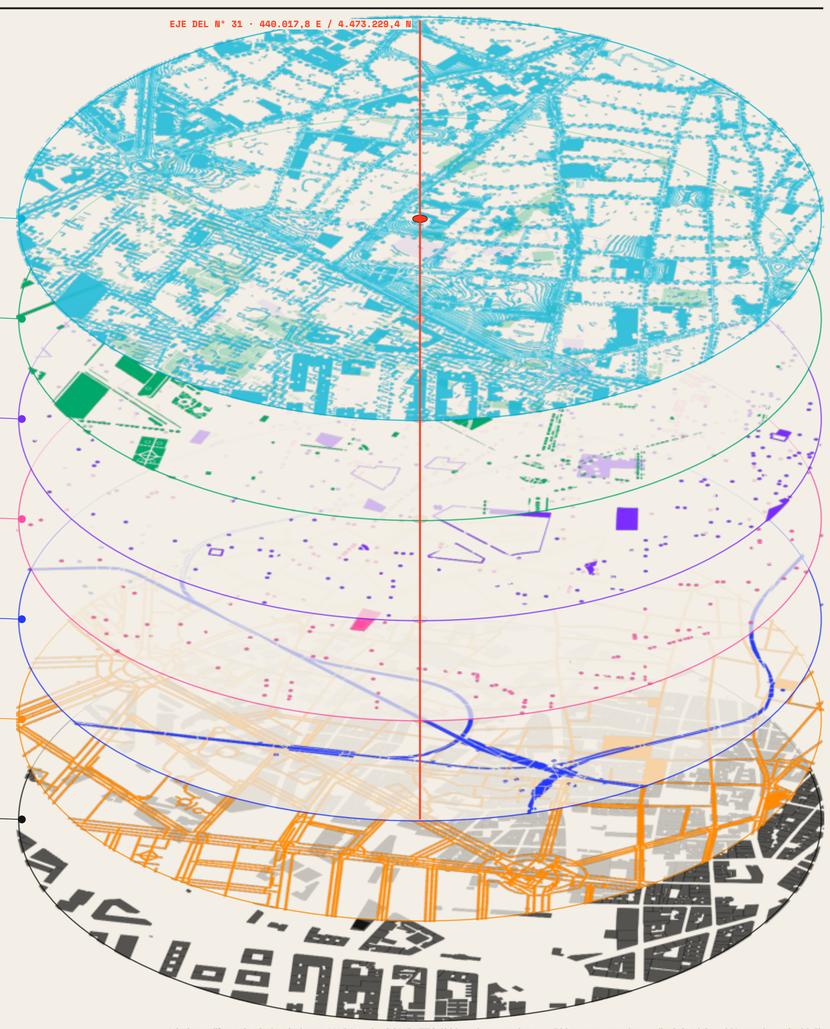


Láminas: diferencia píxel a píxel entre MAPA 1…6 y COMPLETO (220 ppp), recortadas a r = 560 m y proyectadas en dimétrica (giro −32°, escala vertical 0,5).

02 RADIO · LO QUE HAY A 500 M, EN 16 DIRECCIONES Y 5 ANILLOS

A · MEDIDO

Fuente: INVENTARIO_FISICO_600M.gpkg (OSM, 8.021 elementos) · centro: centroide de la parcela

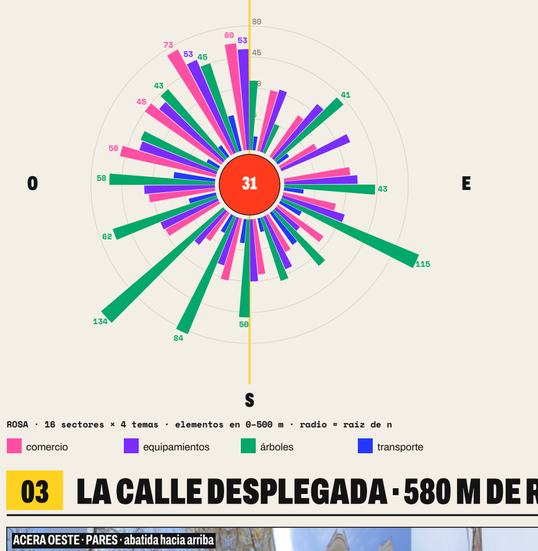

ROSA · 16 sectores × 4 temas · elementos en 0–500 m · radio = raíz de n


comercio · equipamientos · árboles · transporte

DENSIDAD · elementos por hectárea en cada anillo

	n	0–100	100–200	200–300	300–400	400–500
comercio	418	8,3	6,6	4,3	4,9	5,5
equipamientos	414	0,6	3,0	5,2	5,6	6,3
árboles	791	16,9	19,1	11,3	9,8	5,8
bancos	161	1,3	5,3	1,6	2,5	0,9
paradas / bocas	43	0,0	0,1	0,2	0,6	0,9
portales	1186	18,5	19,3	10,3	15,3	15,8
farolas	372	5,4	12,1	4,6	3,8	3,0
patrimonio	68	1,3	1,0	1,0	0,6	0,9
barreras	155	0,6	0,4	1,1	2,1	3,0
edificios	934	11,1	14,3	11,1	11,5	11,9

Recuadro = anillo de máxima densidad de cada fila. Tono relativo a la fila.

A CUÁNTO ESTÁ · distancia en línea recta desde el centroide de la parcela

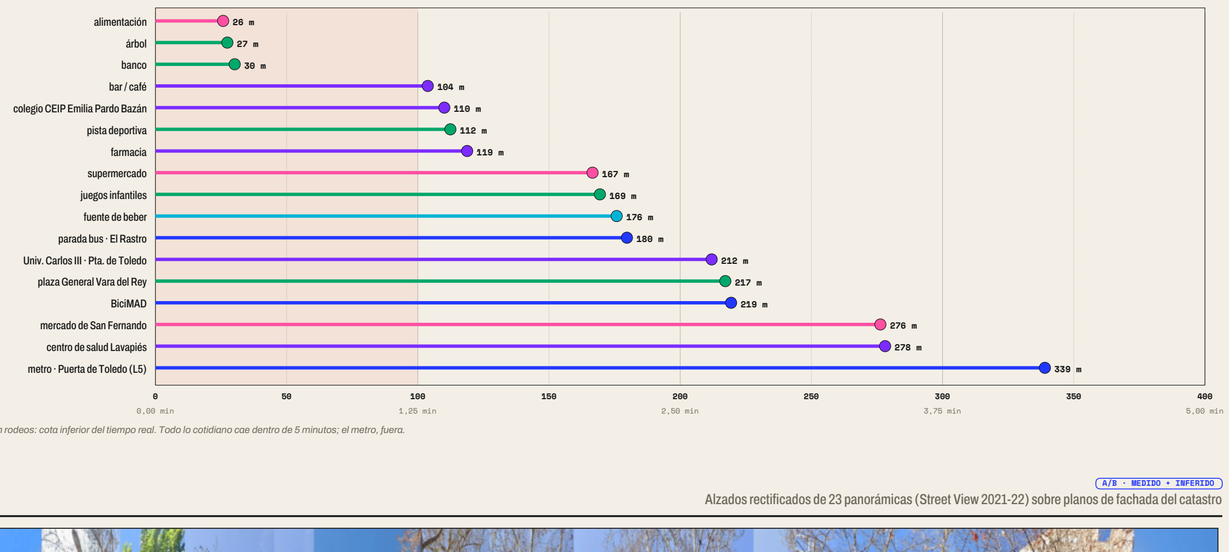


Minutos a 80 m/min sin rodeos: cota inferior del tiempo real. Todo lo cotidiano cae dentro de 5 minutos; el metro, fuera.

03 LA CALLE DESPLEGADA · 580 M DE RIBERA, AMBAS ACERAS ABATIDAS

A/B · MEDIDO + INFERIDO

Alzados rectificados de 23 panorámicas (Street View 2021-22) sobre planos de fachada del catastro

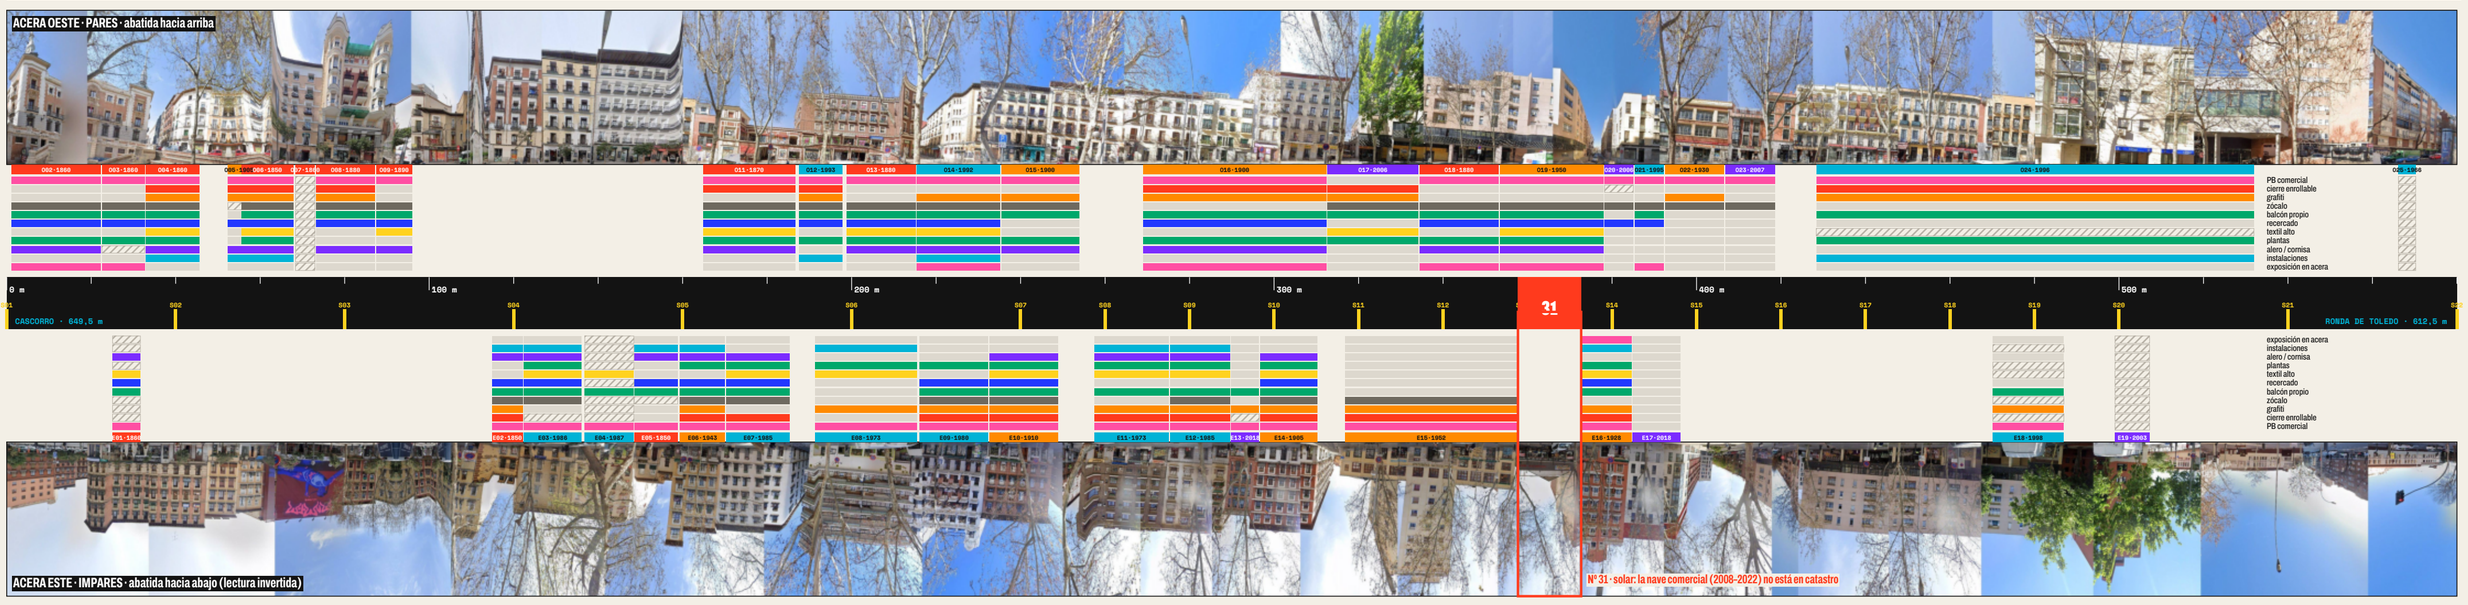

AÑO CATASTRAL DEL FRENTE — antes de 1900 · 15 | 1900–1959 · 10 | 1960–1999 · 13 | 2000 o después · 6

RASGOS · color = presente · gris = ausente · rayado = no legible (árbol, obra, recorte). Frentes = 44 (catastro); legibles = 42.


Escala horizontal y vertical iguales · 1:1.030 en A1

04 PATRONES · ONCE RESPUESTAS QUE LA CALLE YA DA

A/B · MEDIDO + INFERIDO

Regla: patrón = 8 o más casos independientes · nivel B lectura visual · nivel A catastro

P01 · 77%	P02 · 58%	P03 · 79%	P04 · 68%	P05 · 49%	P06 · 67%	P07 · 62%	P08 · 39%	P09 · 22%	P10 · 32%	P11 · 43%
Hueco vertical con balcón propio	Planta baja comercial que se cierra	Basamento que cambia al tocar la calle	Recercado: un segundo borde del hueco	Textil en las plantas altas	Plantas en el balcón	Alero y cornisa que vuelan	Instalaciones como segunda trama	Exposición que ocupa la acera	Salto de altura entre vecinos	Sustitución parcela a parcela
30 / 39 B	19 / 33 B	27 / 34 B	26 / 38 B	18 / 37 B	24 / 36 B	23 / 37 B	14 / 36 B	8 / 37 B	9 / 28 A	19 / 44 A
¿Cada hueco tiene su propio balcón?	*¿Qué fachada queda cuando el comercio cierra?*	*¿Qué material recibe el contacto de la acera?*	*¿Cómo se marca el borde de cada ventana?*	*¿Quién controla la sombra de cada vivienda?*	*¿Dónde se cultiva cuando no hay suelo?*	*¿Cómo termina la fachada contra el cielo?*	*¿Por dónde pasan los cables y las máquinas?*	*¿Hasta dónde llega la tienda?*	*¿Hay una cornisa que continuar?*	*¿De cuándo es lo construido?*

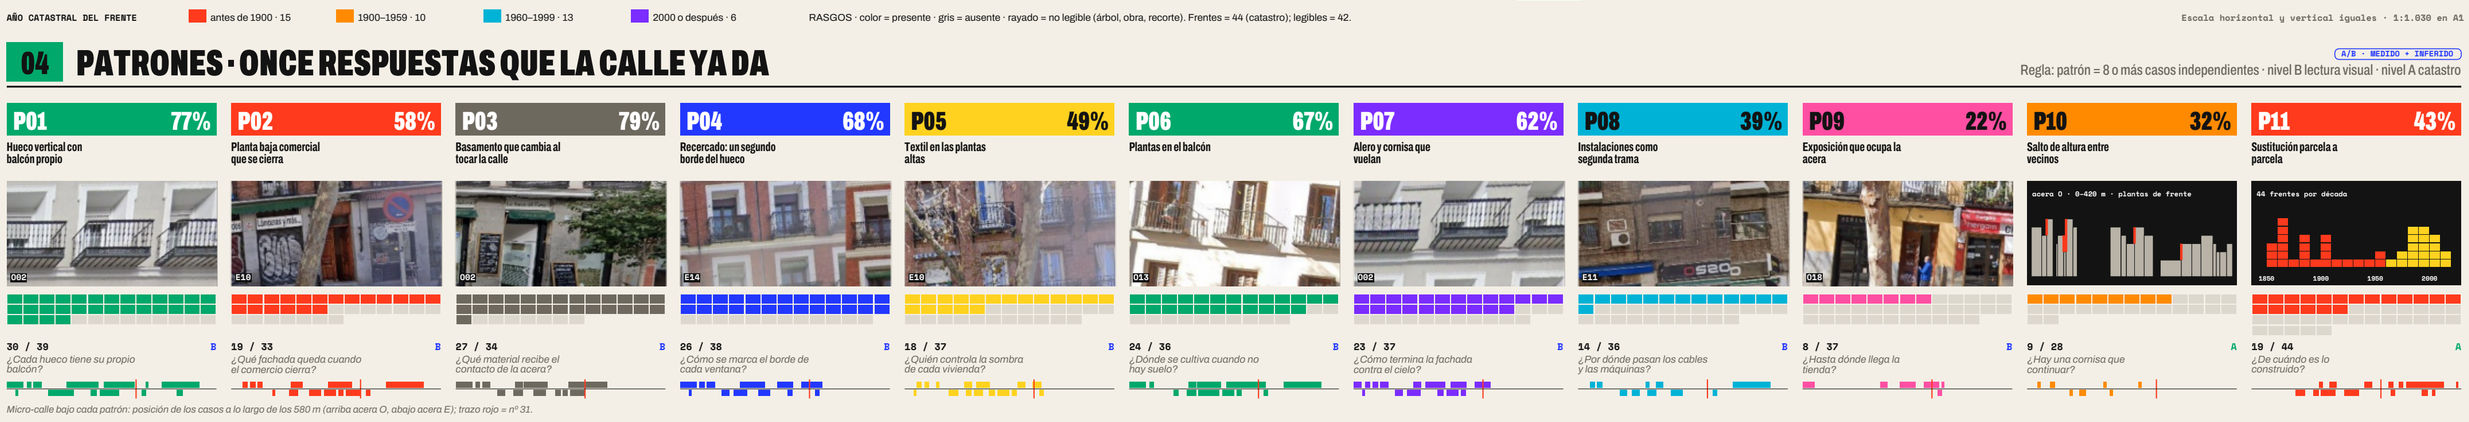


Micro-calle bajo cada patrón: posición de los casos a lo largo de los 580 m (arriba acera O, abajo acera E); trazo rojo = nº 31.

05 SOL · TIEMPO · CRITERIOS

B/C · INFERIDO + HIPÓTESIS


Modelo 2,5D propio: PB 4,0 m + 3,1 m/planta (B) · paso 15 min · celdas 1 m · NOAA

HORAS DE SOL SOBRE LA PARCELA SEGÚN LA COTA

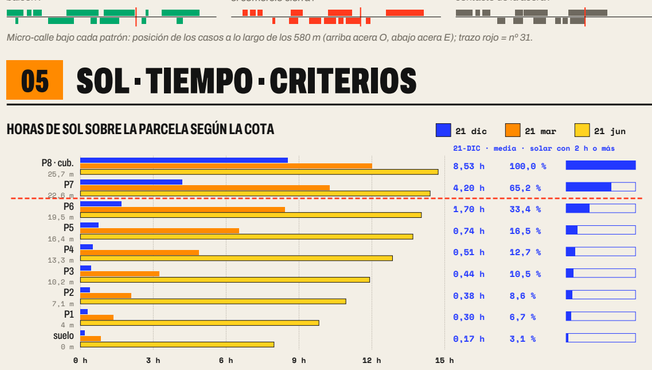

cota a la que el 50 % del solar recibe 2 h de sol el 21-dic: 21,1 m (interpolación lineal entre P6 y P7)

SUELO DEL SOLAR · HORAS DE SOL

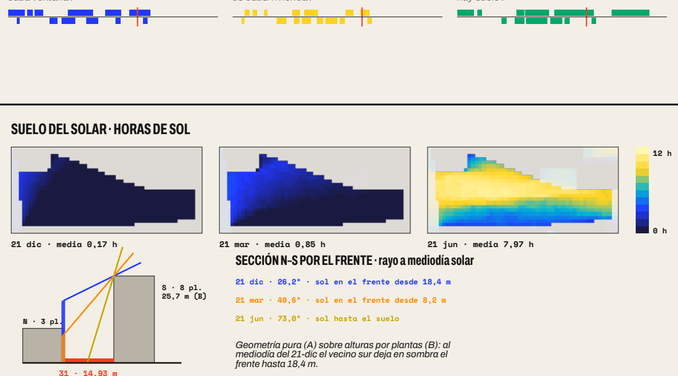

SECCIÓN N-S POR EL FRENTE · rayo a mediodía solar

21 dic · 26,2° · sol en el frente desde 18,4 m
21 mar · 49,6° · sol en el frente desde 8,2 m
21 jun · 73,6° · sol hasta el suelo


Geometría pura (A) sobre alturas por plantas (B): al mediodía del 21-dic el vecino sur deja en sombra el frente hasta 18,4 m.

EL SOLAR EN EL TIEMPO · Street View 2008–2022



DE LA EVIDENCIA AL CRITERIO · hallazgos > patrones > criterios v1 (C)

H-01 el solar no está vacío
H-02 el sol de invierno solo llega arriba
H-03 entre 3 y 10 plantas
H-04 hueco con balcón propio
H-05 planta baja que se cierra
H-06 tienda en la acera
H-07 la calle desciende
H-08 denso y sin estancia

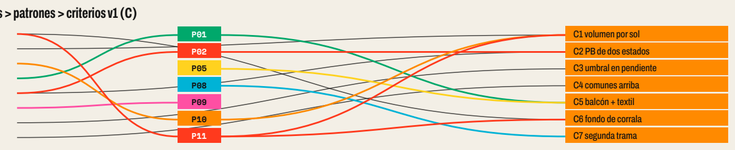

FUENTES · Catastro INSPIRE WFS + OVC (consulta 23-09-2026) · MAPPEADOS/ e INVENTARIO_FISICO_600M.gpkg (OpenStreetMap vía QGIS, 21/22-09-2026) · Google Street View 2008–2022 (23 estaciones + 11 fechas del nº 31) · modelo de sombras y alzados rectificados propios (scripts en 00_INVESTIGACION_COMPLETA/SCRIPTS).

Las distancias son en línea recta; los recuentos OSM dependen de la completitud del mapa (A = lo que el inventario contiene). Alturas por plantas catastrales con hipótesis PB 4,0 m + 3,1 m (B).